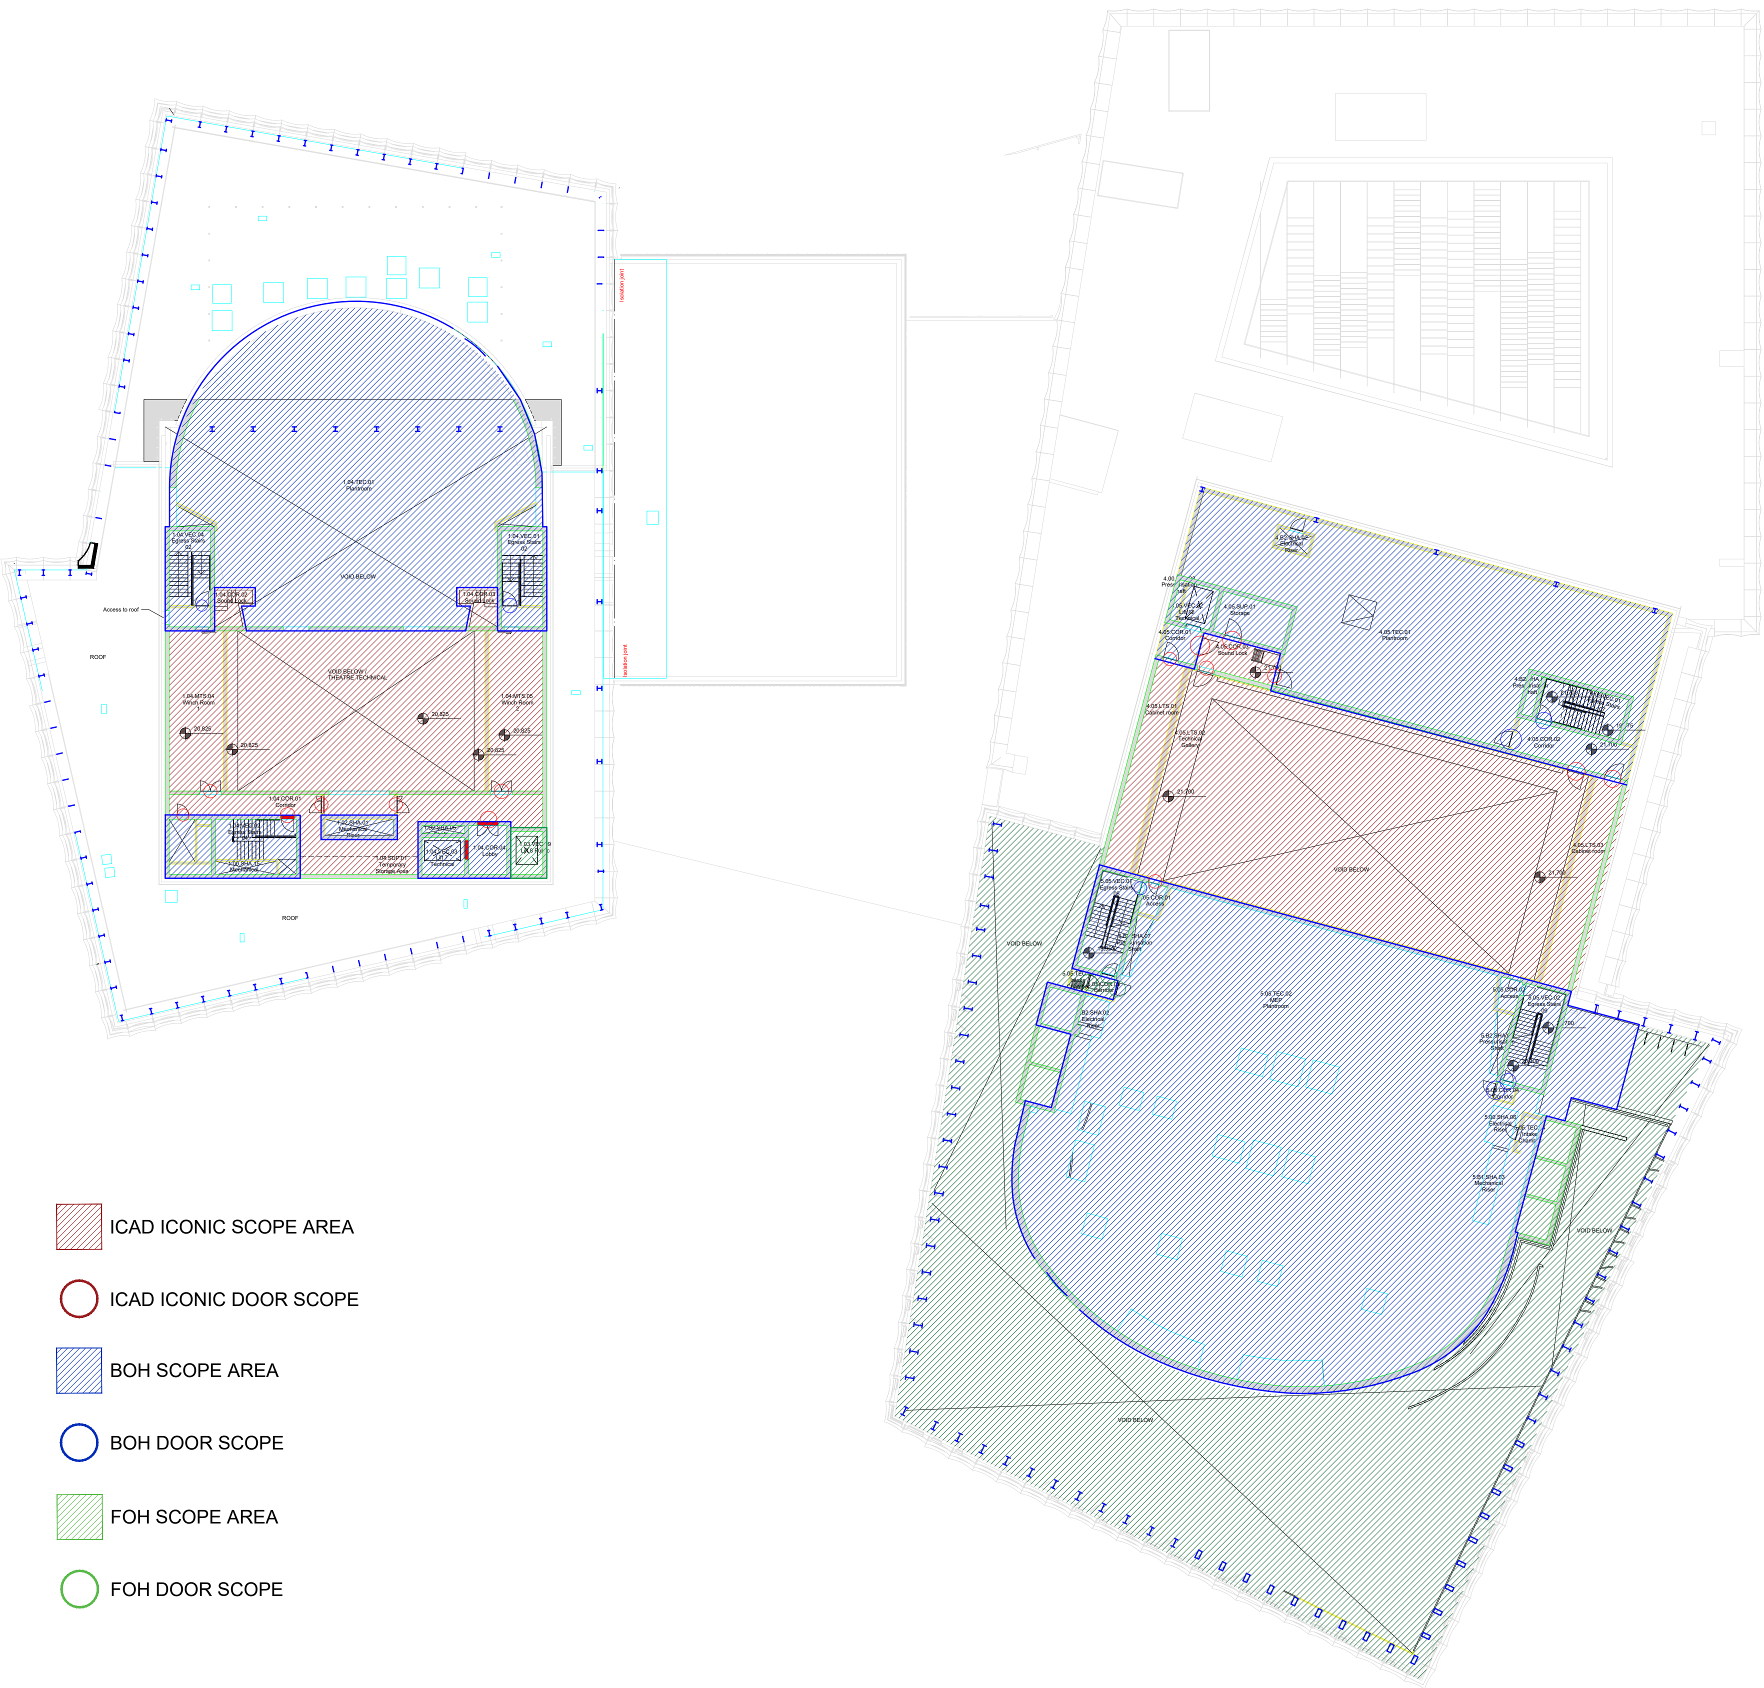
1.04.TEC.01
Plantroom
VOID BELOW
1.04.VEC.04
Egress Stairs
02
1.04.VEC.01
Egress Stairs
02
1.04.COR.02
Sound Lock
1.04.COR.03
Sound Lock
Access to roof
ROOF
VOID BELOW /
THEATRE TECHNICAL
1.04.MTS.04
Winch Room
1
1.04.MTS.05
Winch Room
2
20.825
1.04.COR.01
Corridor
1.04.VEC.02
Egress Stairs
04
1.02.SHA.01
Mechanical
Riser
1.00.SHA.15
Mechanical
1.04.SUP.01
Temporary
Storage Area
1.04.VEC.03
Lift 7
Technical
1.04.COR.04
Lobby
ROOF
Isolation joint
4.B2.SHA.02
Electrical
Riser
4.05.VEC.02
Lift 12
Technical
4.05.SUP.01
Storage
4.05.TEC.01
Plantroom
4.05.COR.01
Corridor
4.05.COR.03
Sound Lock
21.700
4.05.COR.02
Corridor
4.05.LTS.01
Cabinet room
4.05.LTS.02
Technical
Gallery
4.05.LTS.03
Cabinet room
VOID BELOW
5.05.VEC.01
Egress Stairs
08
5.05.COR.01
Access
5.05.TEC.02
MEP
Plantroom
B2.SHA.02
Electrical
Riser
5.05.COR.02
Access
5.05.VEC.02
Egress Stairs
09
5.05.COR.04
Corridor
5.00.SHA.06
Electrical
Riser
5.B1.SHA.03
Mechanical
Riser
VOID BELOW

- 🟥 ICAD ICONIC SCOPE AREA
- ○ ICAD ICONIC DOOR SCOPE
- 🟦 BOH SCOPE AREA
- ○ BOH DOOR SCOPE
- 🟩 FOH SCOPE AREA
- ○ FOH DOOR SCOPE

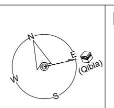

DO NOT SCALE

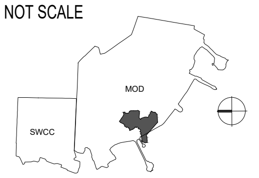

INDEX PLAN

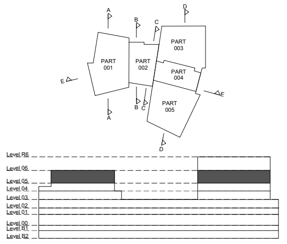
A
B
C
D
E
PART 001
PART 002
PART 003
PART 004
PART 005
Level R6
Level 06
Level 05
Level 04
Level 03
Level 02
Level 01
Level 00
Level B1
Level B2

BUILDING KEY PLAN

GENERAL NOTES:

LEGEND & ABBREVIATIONS:

Strutural Floor Expansion Joint

Interior Joint Details:
- JOH-HLA-S4-01-056-XXX-ZZ-DR-AR-015800

See facade detail package for exterior joints

- The line serves as an indicative guide, and the partial plans should be used for accurately establishing the joint line in the finishes.

F00	31-01-2024	BB	Issued for Construction	LFN	NF
REV	**DATE**	**BY**	**DESCRIPTION**	**CHK**	**APR**

DRAWING STATUS:
Issued for Construction

CLIENT:
C:\Users\TZKA\OneDrive - Ramboll\Desktop\Temp\JOH-HLA-S4-01-056-XXX-ZZ-M3-AR-019300-JCDCLogo-26987616.jpg

LEAD DESIGN CONSULTANTS:

LEAD ENGINEERING CONSULTANT:
C:\Users\TZKA\OneDrive - Ramboll\Desktop\Temp\JOH-HLA-S4-01-056-XXX-ZZ-M3-AR-019300-BHLogo-26987620.png

GENERAL CONTRACTOR:
GENERAL CONTRACTOR

PROJECT:
JEDDAH OPERA HOUSE

TITLE:
ARCHITECT
PLAN
LEVEL 05

SCALE A0 (841x1189)	CHECKED	APPROVED	MODEL FILE REF
1:200	LFN	NF	JOH-HLA-S4-01-056-XXX-ZZ-M3-AR-019300
PROJECT No:	DESIGNED	DRAWN	DATE:
1960020123	HLA	VCS	31-01-2024

DRAWING NO.
JOH-HLA-S4-01-056-XXX-05-DR-AR-011150

REV:
F00

©JCDC