

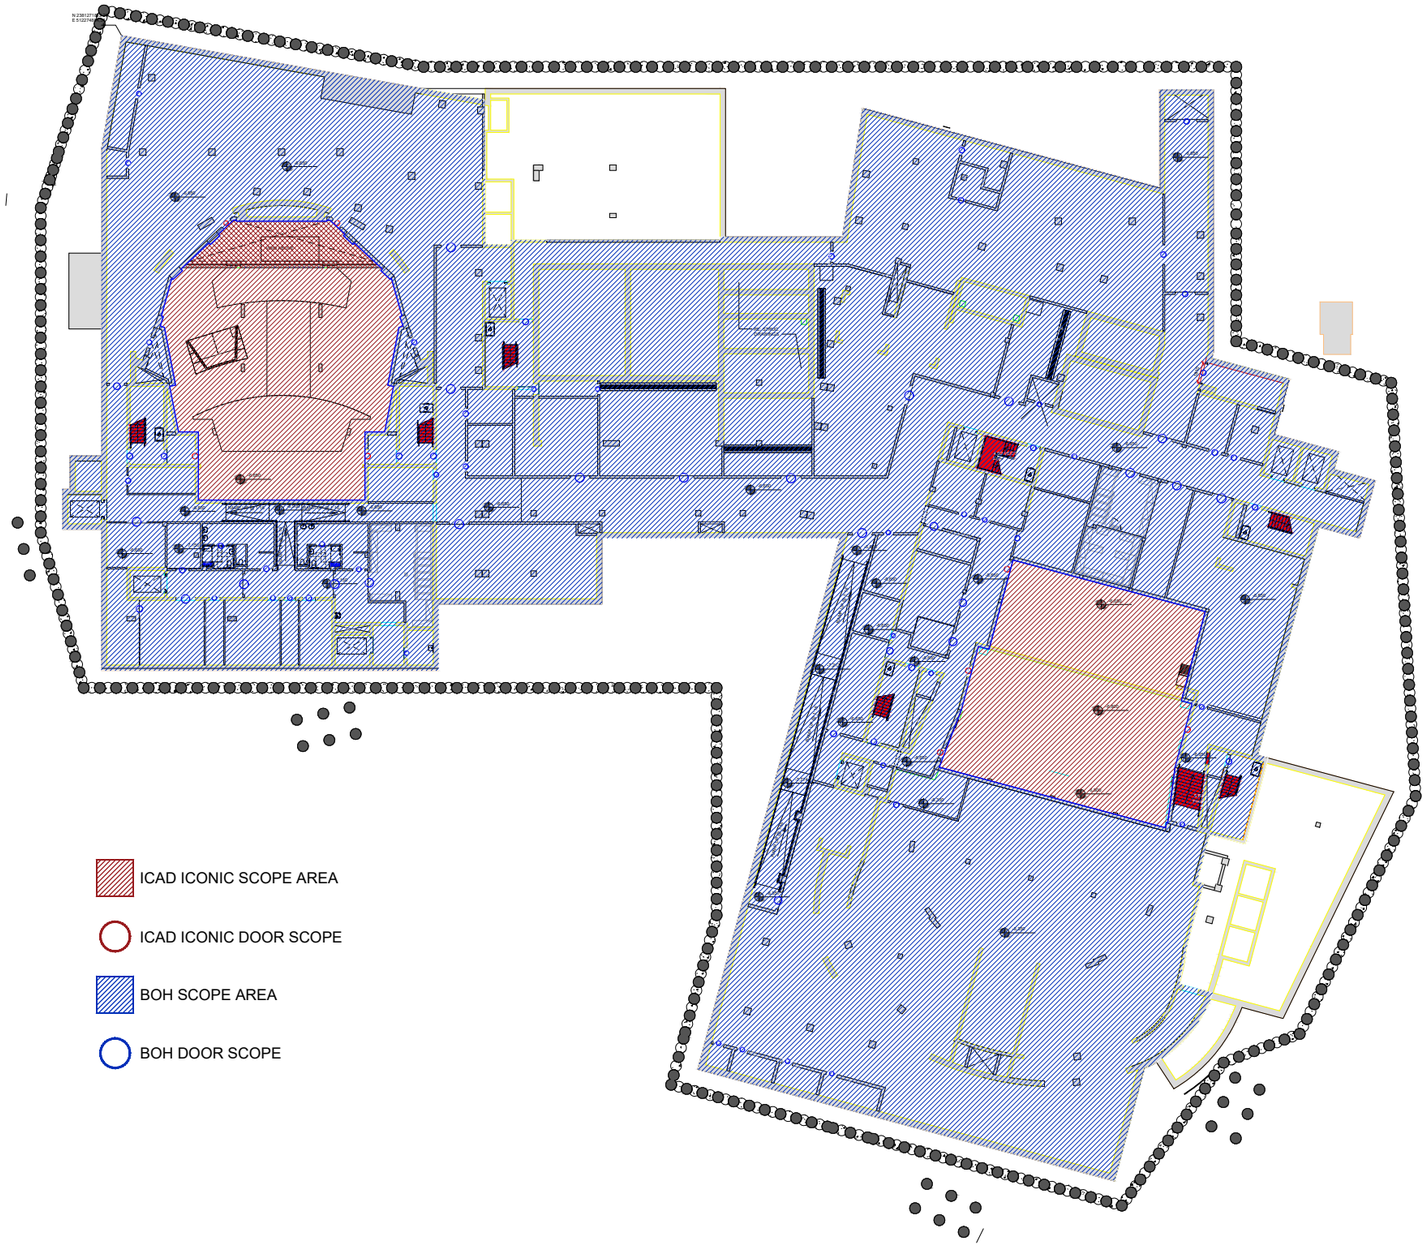


DO NOT SCALE

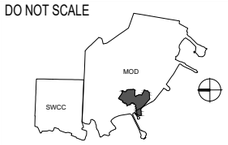

INDEX PLAN

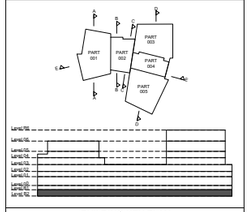

BUILDING KEY PLAN

GENERAL NOTES:

LEGEND & ABBREVIATIONS:

REV	DATE	BY	DESCRIPTION	CHK	APR
F03	31-01-2024	BB	Issued for Construction	LFN	NF

DRAWING STATUS:
Issued for Construction

CLIENT:

LEAD DESIGN CONSULTANTS:

LEAD ENGINEERING CONSULTANT:

GENERAL CONTRACTOR:
GENERAL CONTRACTOR

PROJECT:
JEDDAH OPERA HOUSE

TITLE:
ARCHITECT
PLAN
LEVEL B2

SCALE A0 (841x1189)	CHECKED	APPROVED	MODEL FILE REF
1:200	LFN	NF	JOH-HLA-S4-01-056-XXX-ZZ-M3-AR-011000
PROJECT No:	DESIGNED	DRAWN	DATE:
1960020123	HLA	VCS	31-01-2024

DRAWING NO.: JOH-HLA-S4-01-056-XXX-B2-DR-AR-011190 REV: F00

©JCDC