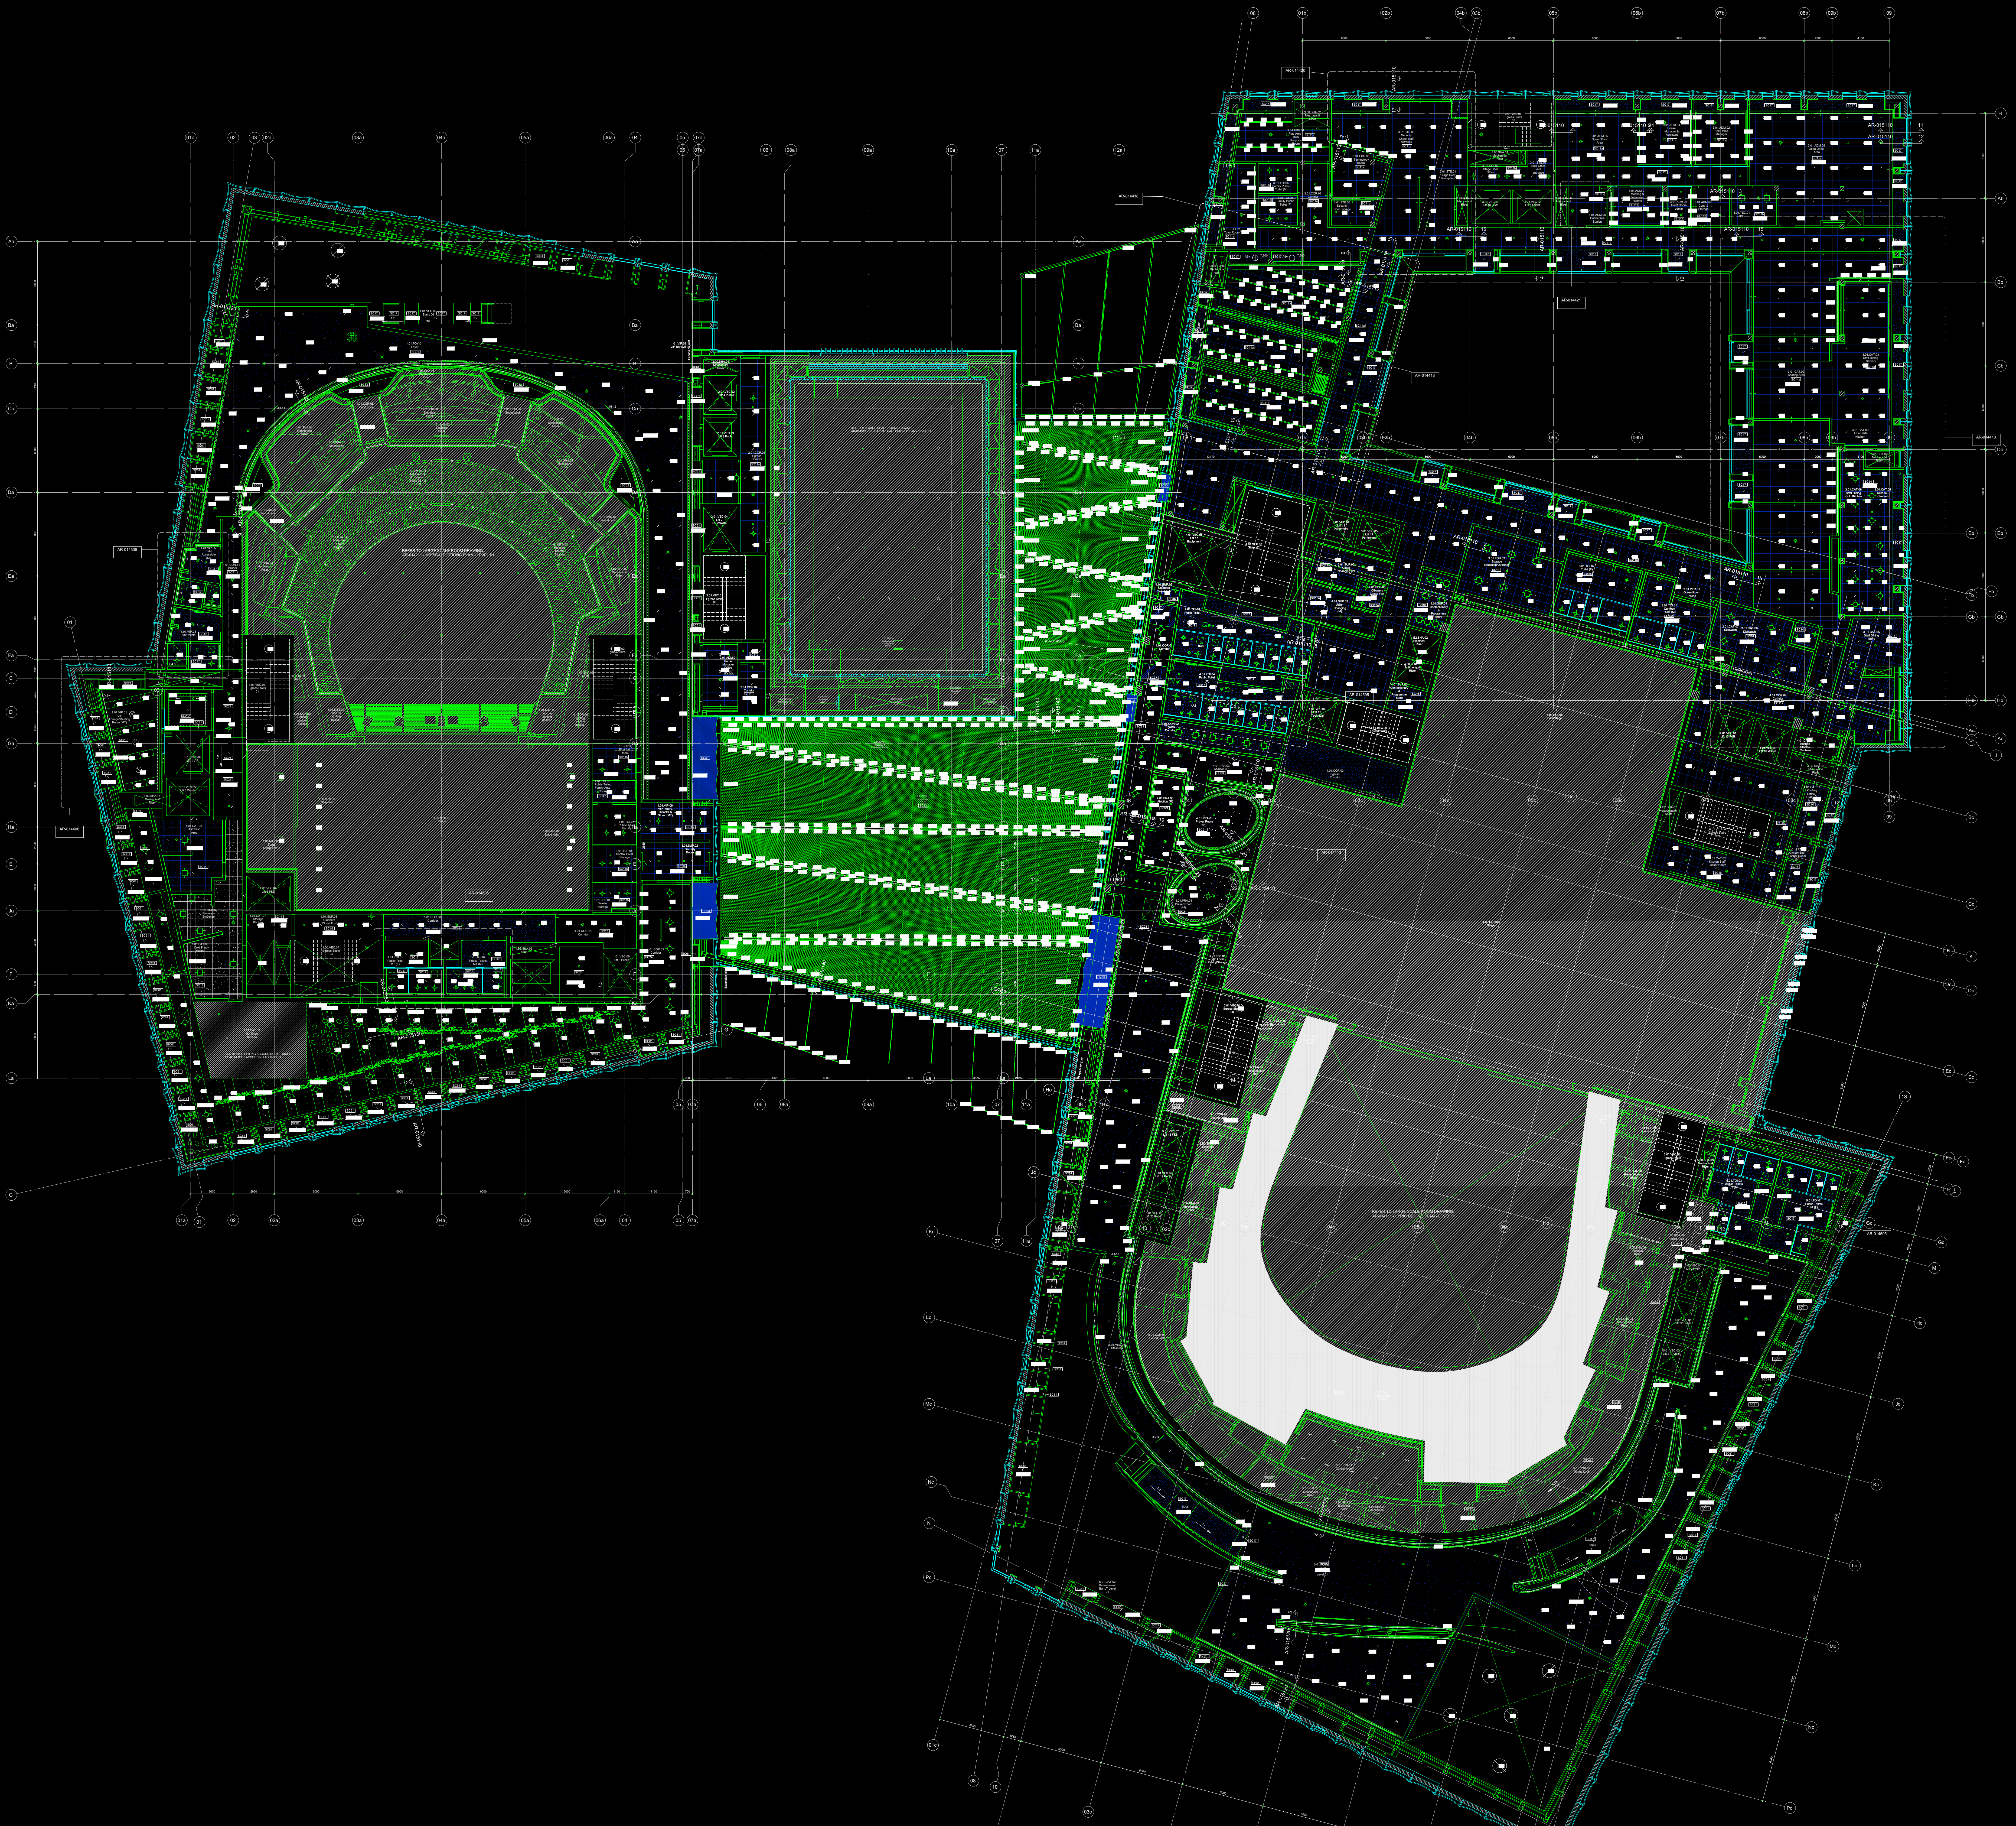
REFER TO LARGE SCALE ROOM DRAWING:
AR-014211 - MIDSCALE CEILING PLAN - LEVEL 01
1.01.MTA.03
MT Balcony
01Premium
seats 32 + 2
PRM
1.01.MTA.01
Midscale
Theatre
Seating
1.01.MTA.02
Midscale
Theatre
Seating
1.01.SHA.05
Mechanical
Riser
1.01.SHA.04
Mechanical
Riser
1.00.SHA.09
Shaft
1.00.SHA.06
Shaft
REFER TO LARGE SCALE ROOM DRAWING:
AR-014312 - REHEARSAL HALL CEILING PLAN - LEVEL 01
Da
REFER TO LARGE SCALE ROOM DRAWING:
AR-014111 - LYRIC CEILING PLAN - LEVEL 01
04c
05c
06c
Hc