LEVEL 02 - DC11 CEILING LOCATIONS			
RED SOLID = DC11 CEILING / PURPLE OUTLINE = LOCATION			
No.	Room No.	Room Name	DC11 Area (m2)
1	1.01.COR.12	Corridor	shared area
2	1.02.SUP.02	Storage	50.53
3	2.02.REH.01	Rehearsal Hall Technical floor	670.03
4	4.02.COR.03	Corridor	shared area
5	4.02.COR.04	Corridor	shared area
6	4.02.FBS.01	F&B Pantry, Waste Store (LT)	190.83
7	4.02.VEC.02	Egress Stairs 07	6.47
		TOTAL	985.52

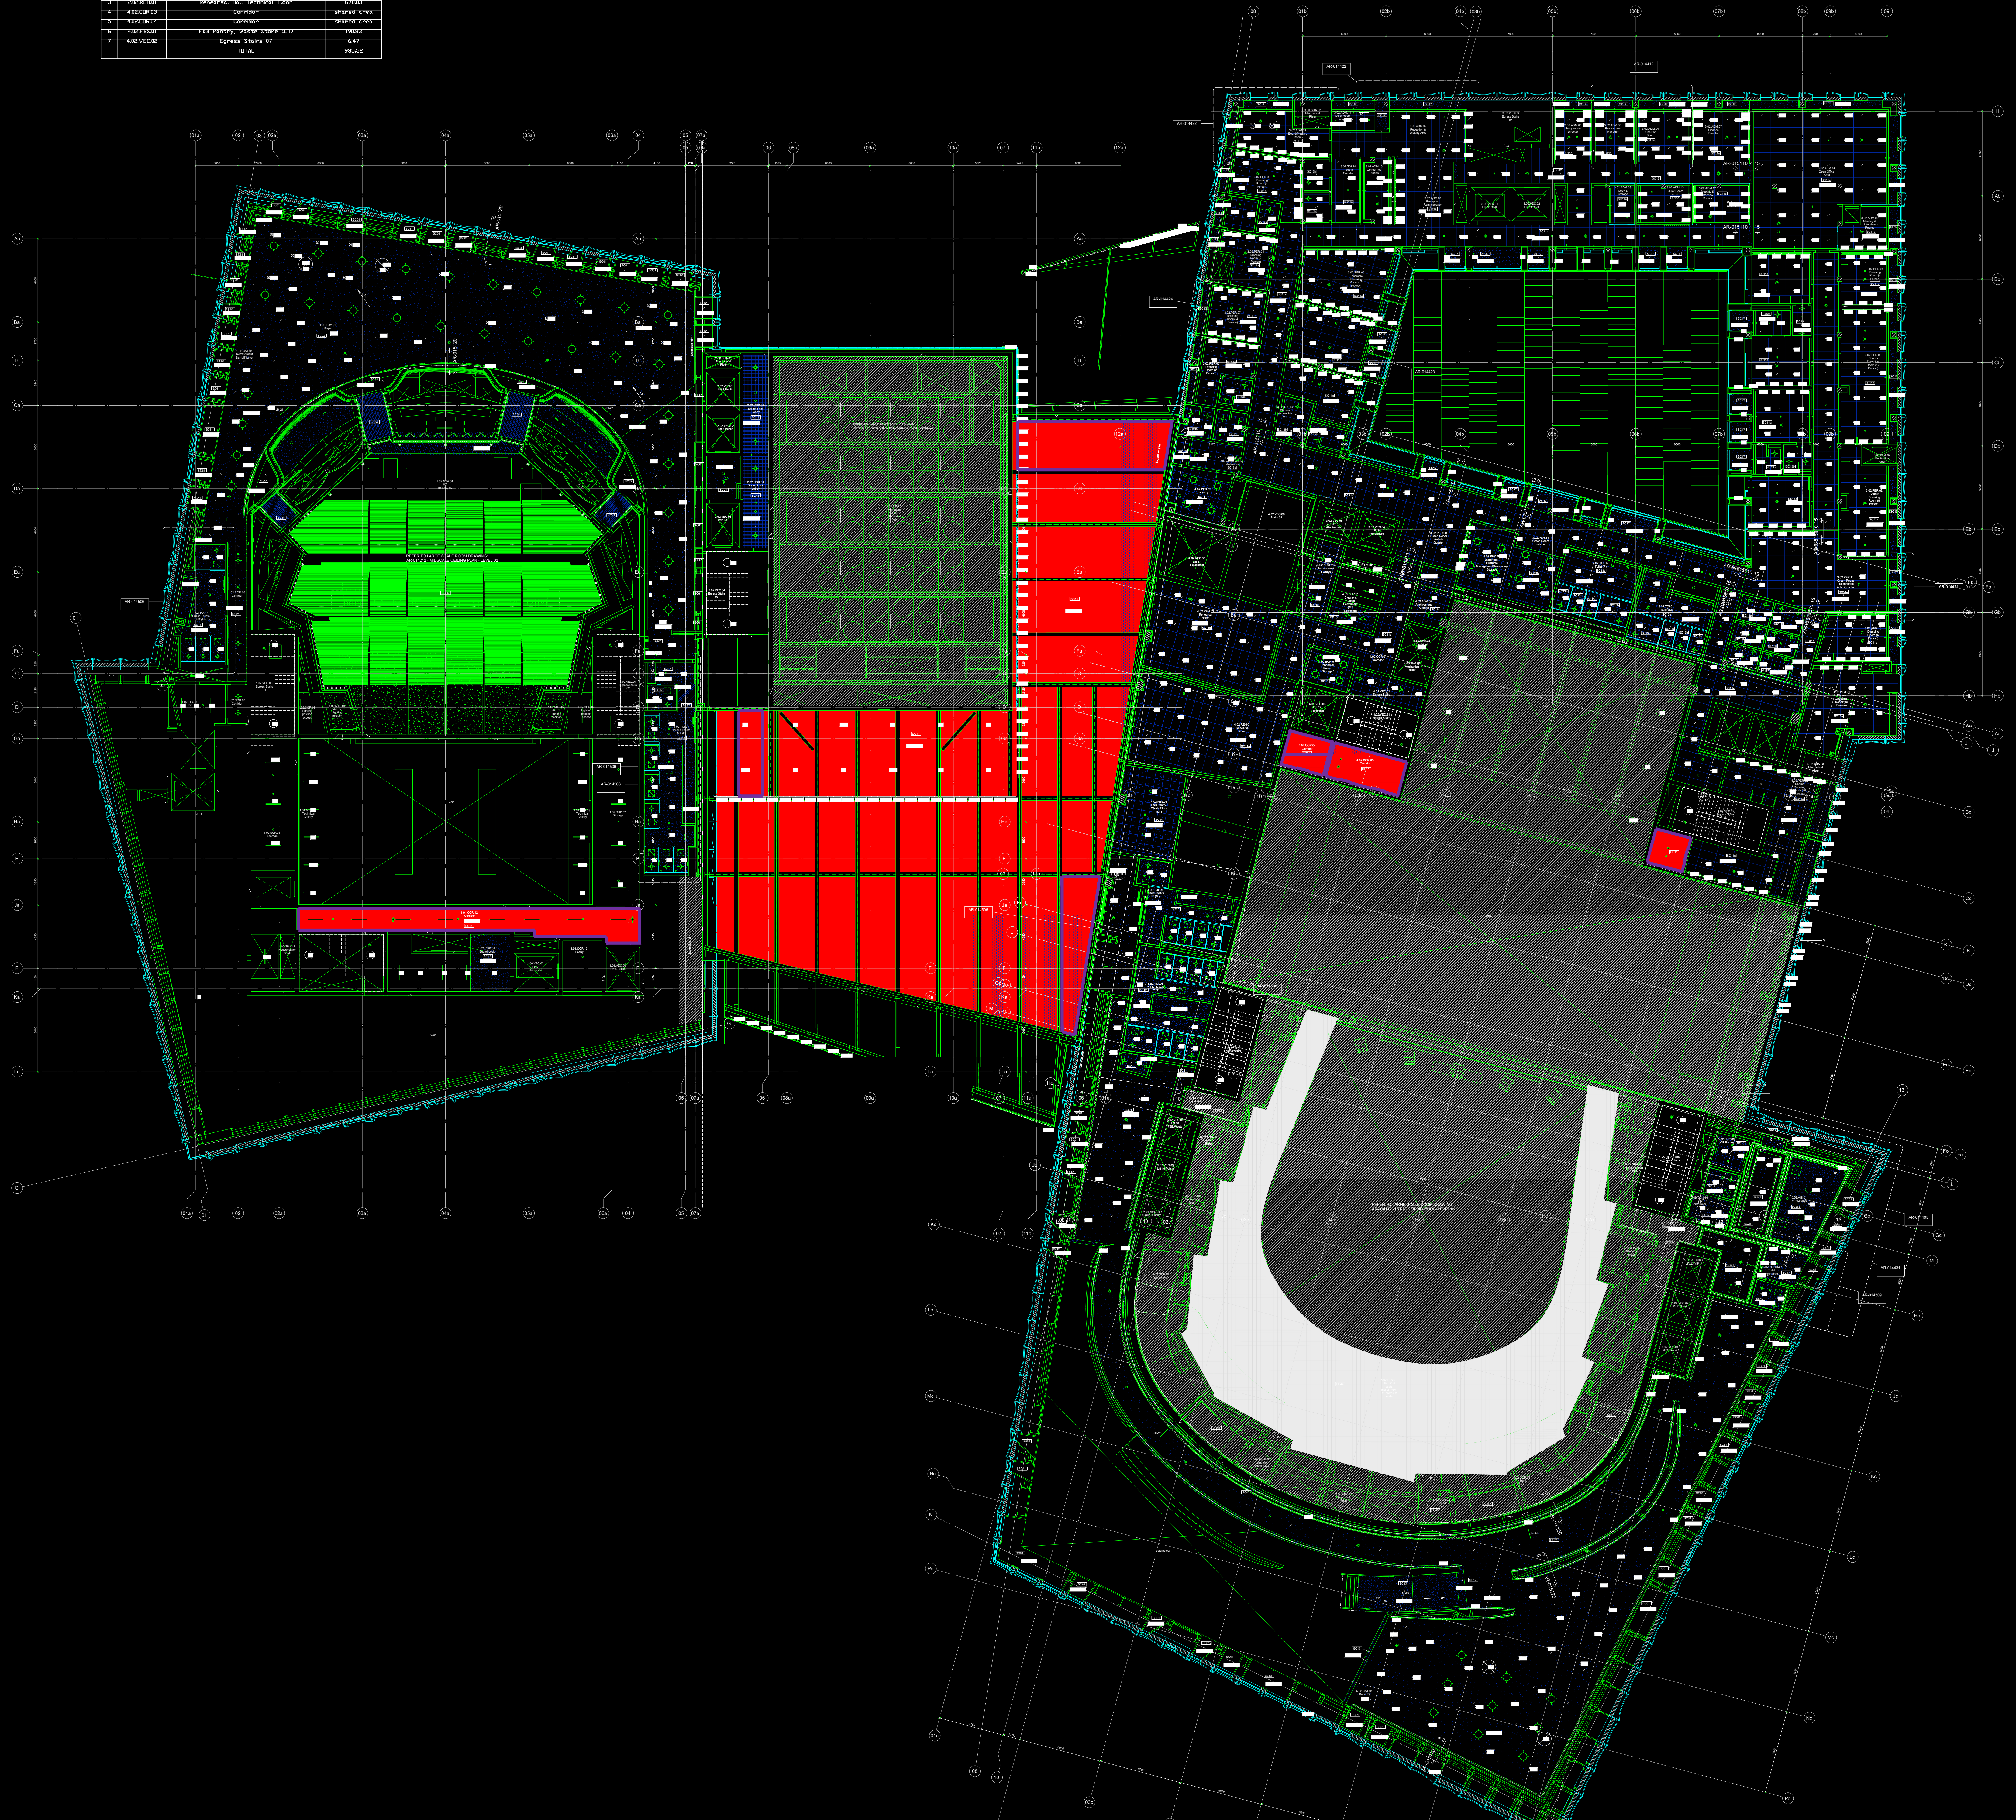
1.02.MTA.01
MT
Balcony 02
REFER TO LARGE SCALE ROOM DRAWING:
AR-014212 - MIDSCALE CEILING PLAN - LEVEL 02
SC35
Void
REFER TO LARGE SCALE ROOM DRAWING:
AR-014112 - LYRIC CEILING PLAN - LEVEL 02
04c
05c
06c
01a
02
03
02a
03a