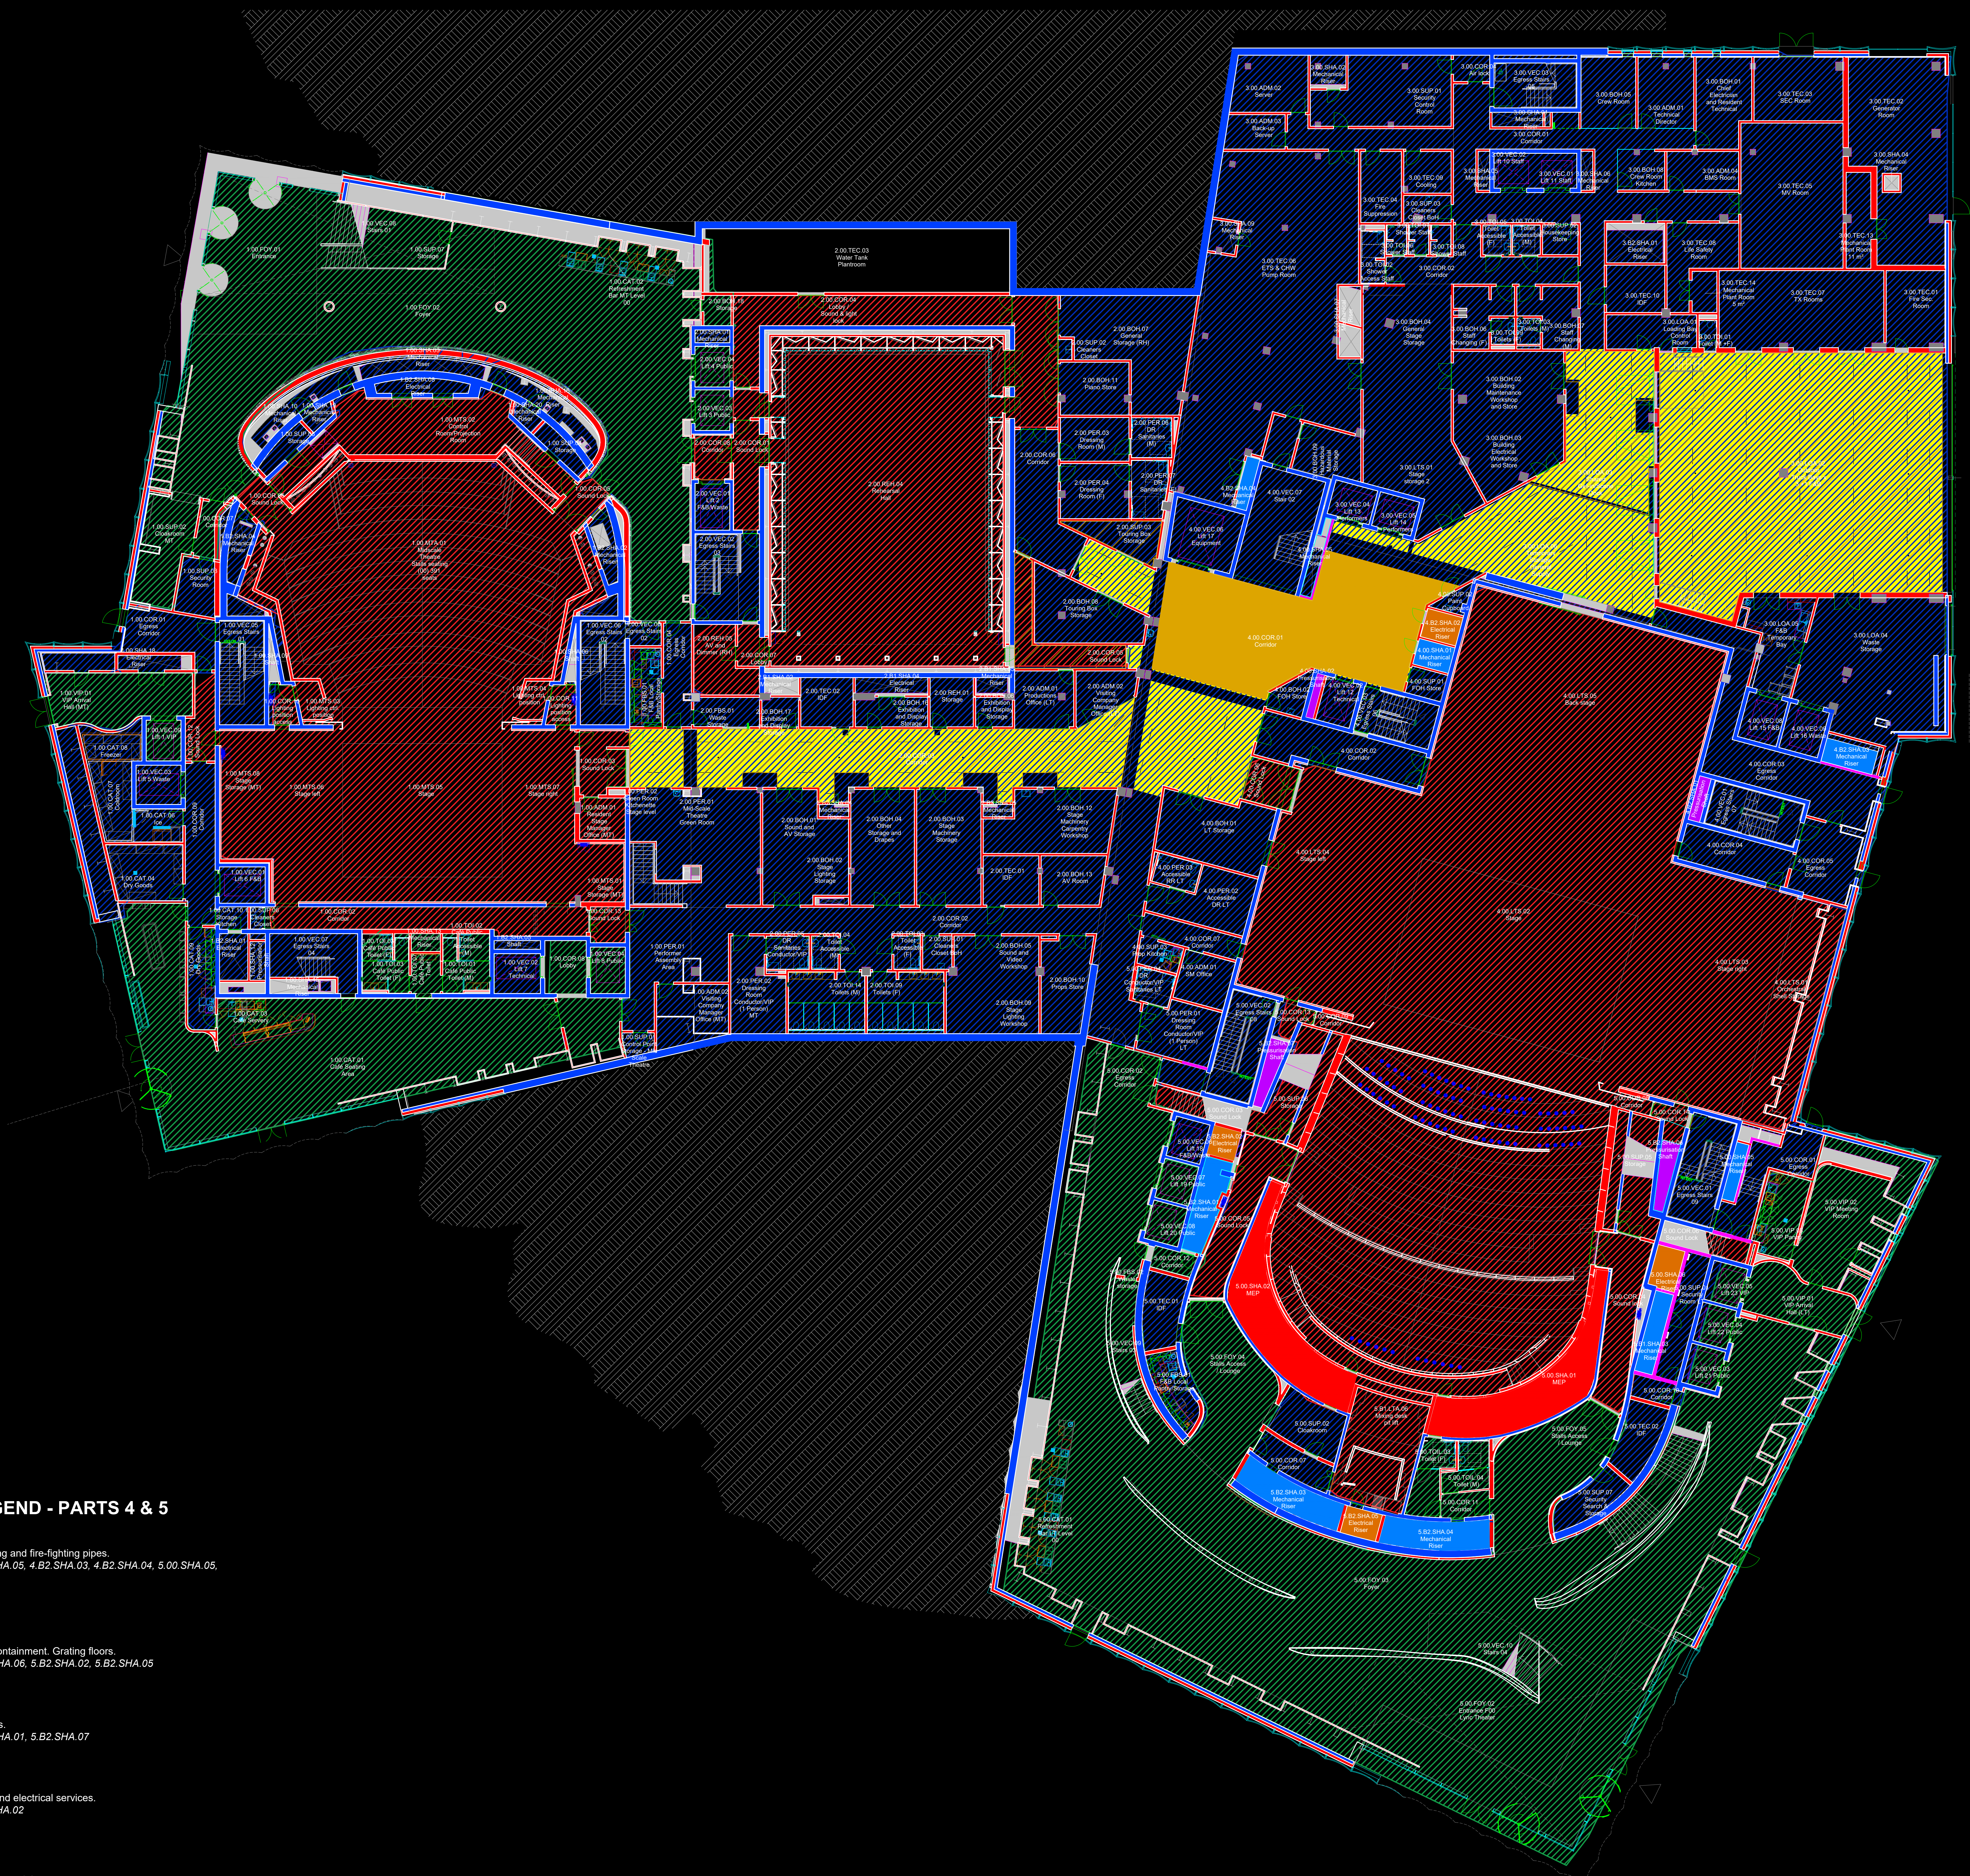

SHAFTS & RISERS LEGEND - PARTS 4 & 5

🟦	**MECHANICAL RISER** HVAC ducts, chilled water, plumbing and fire-fighting pipes. *On this plan: 4.00.SHA.01, 4.00.SHA.05, 4.B2.SHA.03, 4.B2.SHA.04, 5.00.SHA.05,*
🟧	**ELECTRICAL RISER** LV trays, busbars, DBs and ELV containment. Grating floors. *On this plan: 4.B2.SHA.02, 5.00.SHA.06, 5.B2.SHA.02, 5.B2.SHA.05*
🟪	**PRESSURISATION SHAFT** Stair / lift lobby pressurisation ducts. *On this plan: 4.00.SHA.02, 4.B2.SHA.01, 5.B2.SHA.07*
🟥	**MEP SHAFT (COMBINED)** Combined mechanical, plumbing and electrical services. *On this plan: 5.00.SHA.01, 5.00.SHA.02*
🟨	**DC11 CEILING - ACOUSTIC ROCK WOOL** Acoustic rock wool, mineral fibre panel.

JOH-HLA-S4-01-056-XXX-00-DR-AR-011100