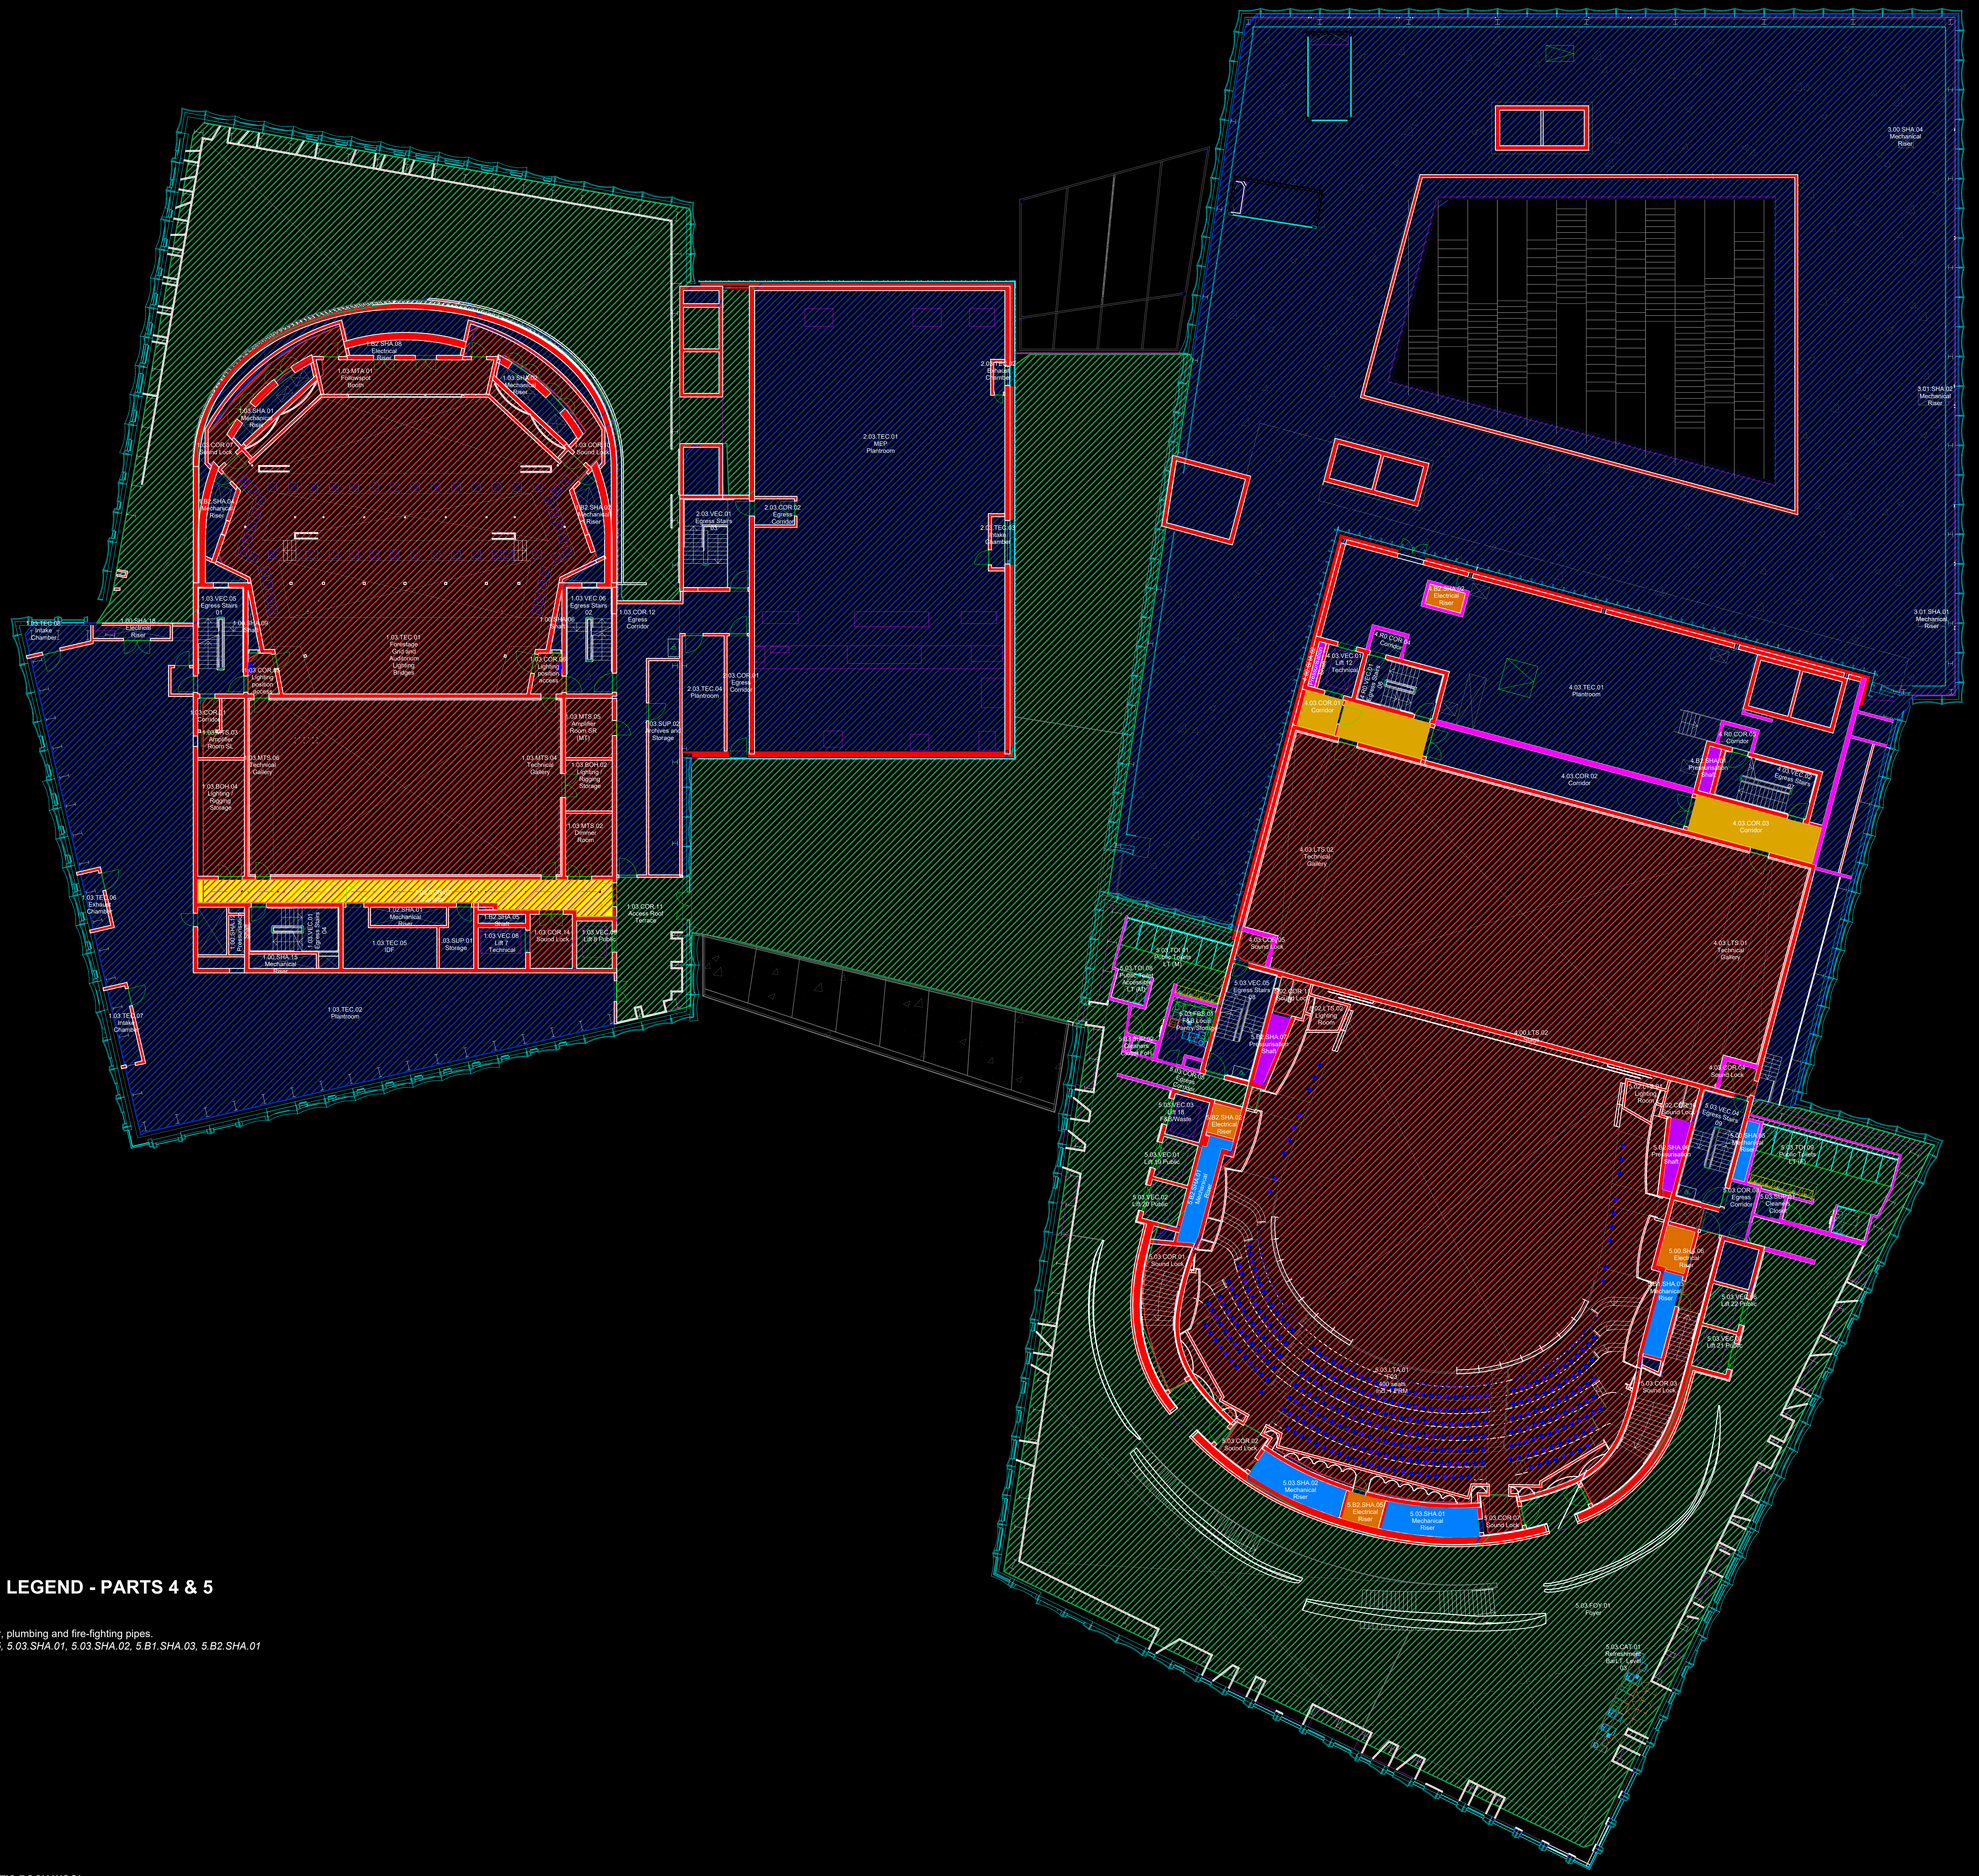
5.03.LTA.01
F03
400 seats
incl. 1 PRM
5.03.COR.02
Sound Lock
5.03.SHA.02
Mechanical
Riser
5.B2.SHA.05
Electrical
Riser
5.03.SHA.01
Mechanical
Riser
5.03.COR.07
Sound Lock
5.03.FOY.01
Foyer
5.03.CAT.01
Refreshment

SHAFTS & RISERS LEGEND - PARTS 4 & 5

🟦 **MECHANICAL RISER**
HVAC ducts, chilled water, plumbing and fire-fighting pipes.
On this plan: 5.00.SHA.05, 5.03.SHA.01, 5.03.SHA.02, 5.B1.SHA.03, 5.B2.SHA.01

🟧

🟪

🟨 **DC11 CEILING - ACOUSTIC ROCK WOOL**
Acoustic rock wool, mineral fibre panel.

JOH-HLA-S4-01-056-XXX-03-DR-AR-011130