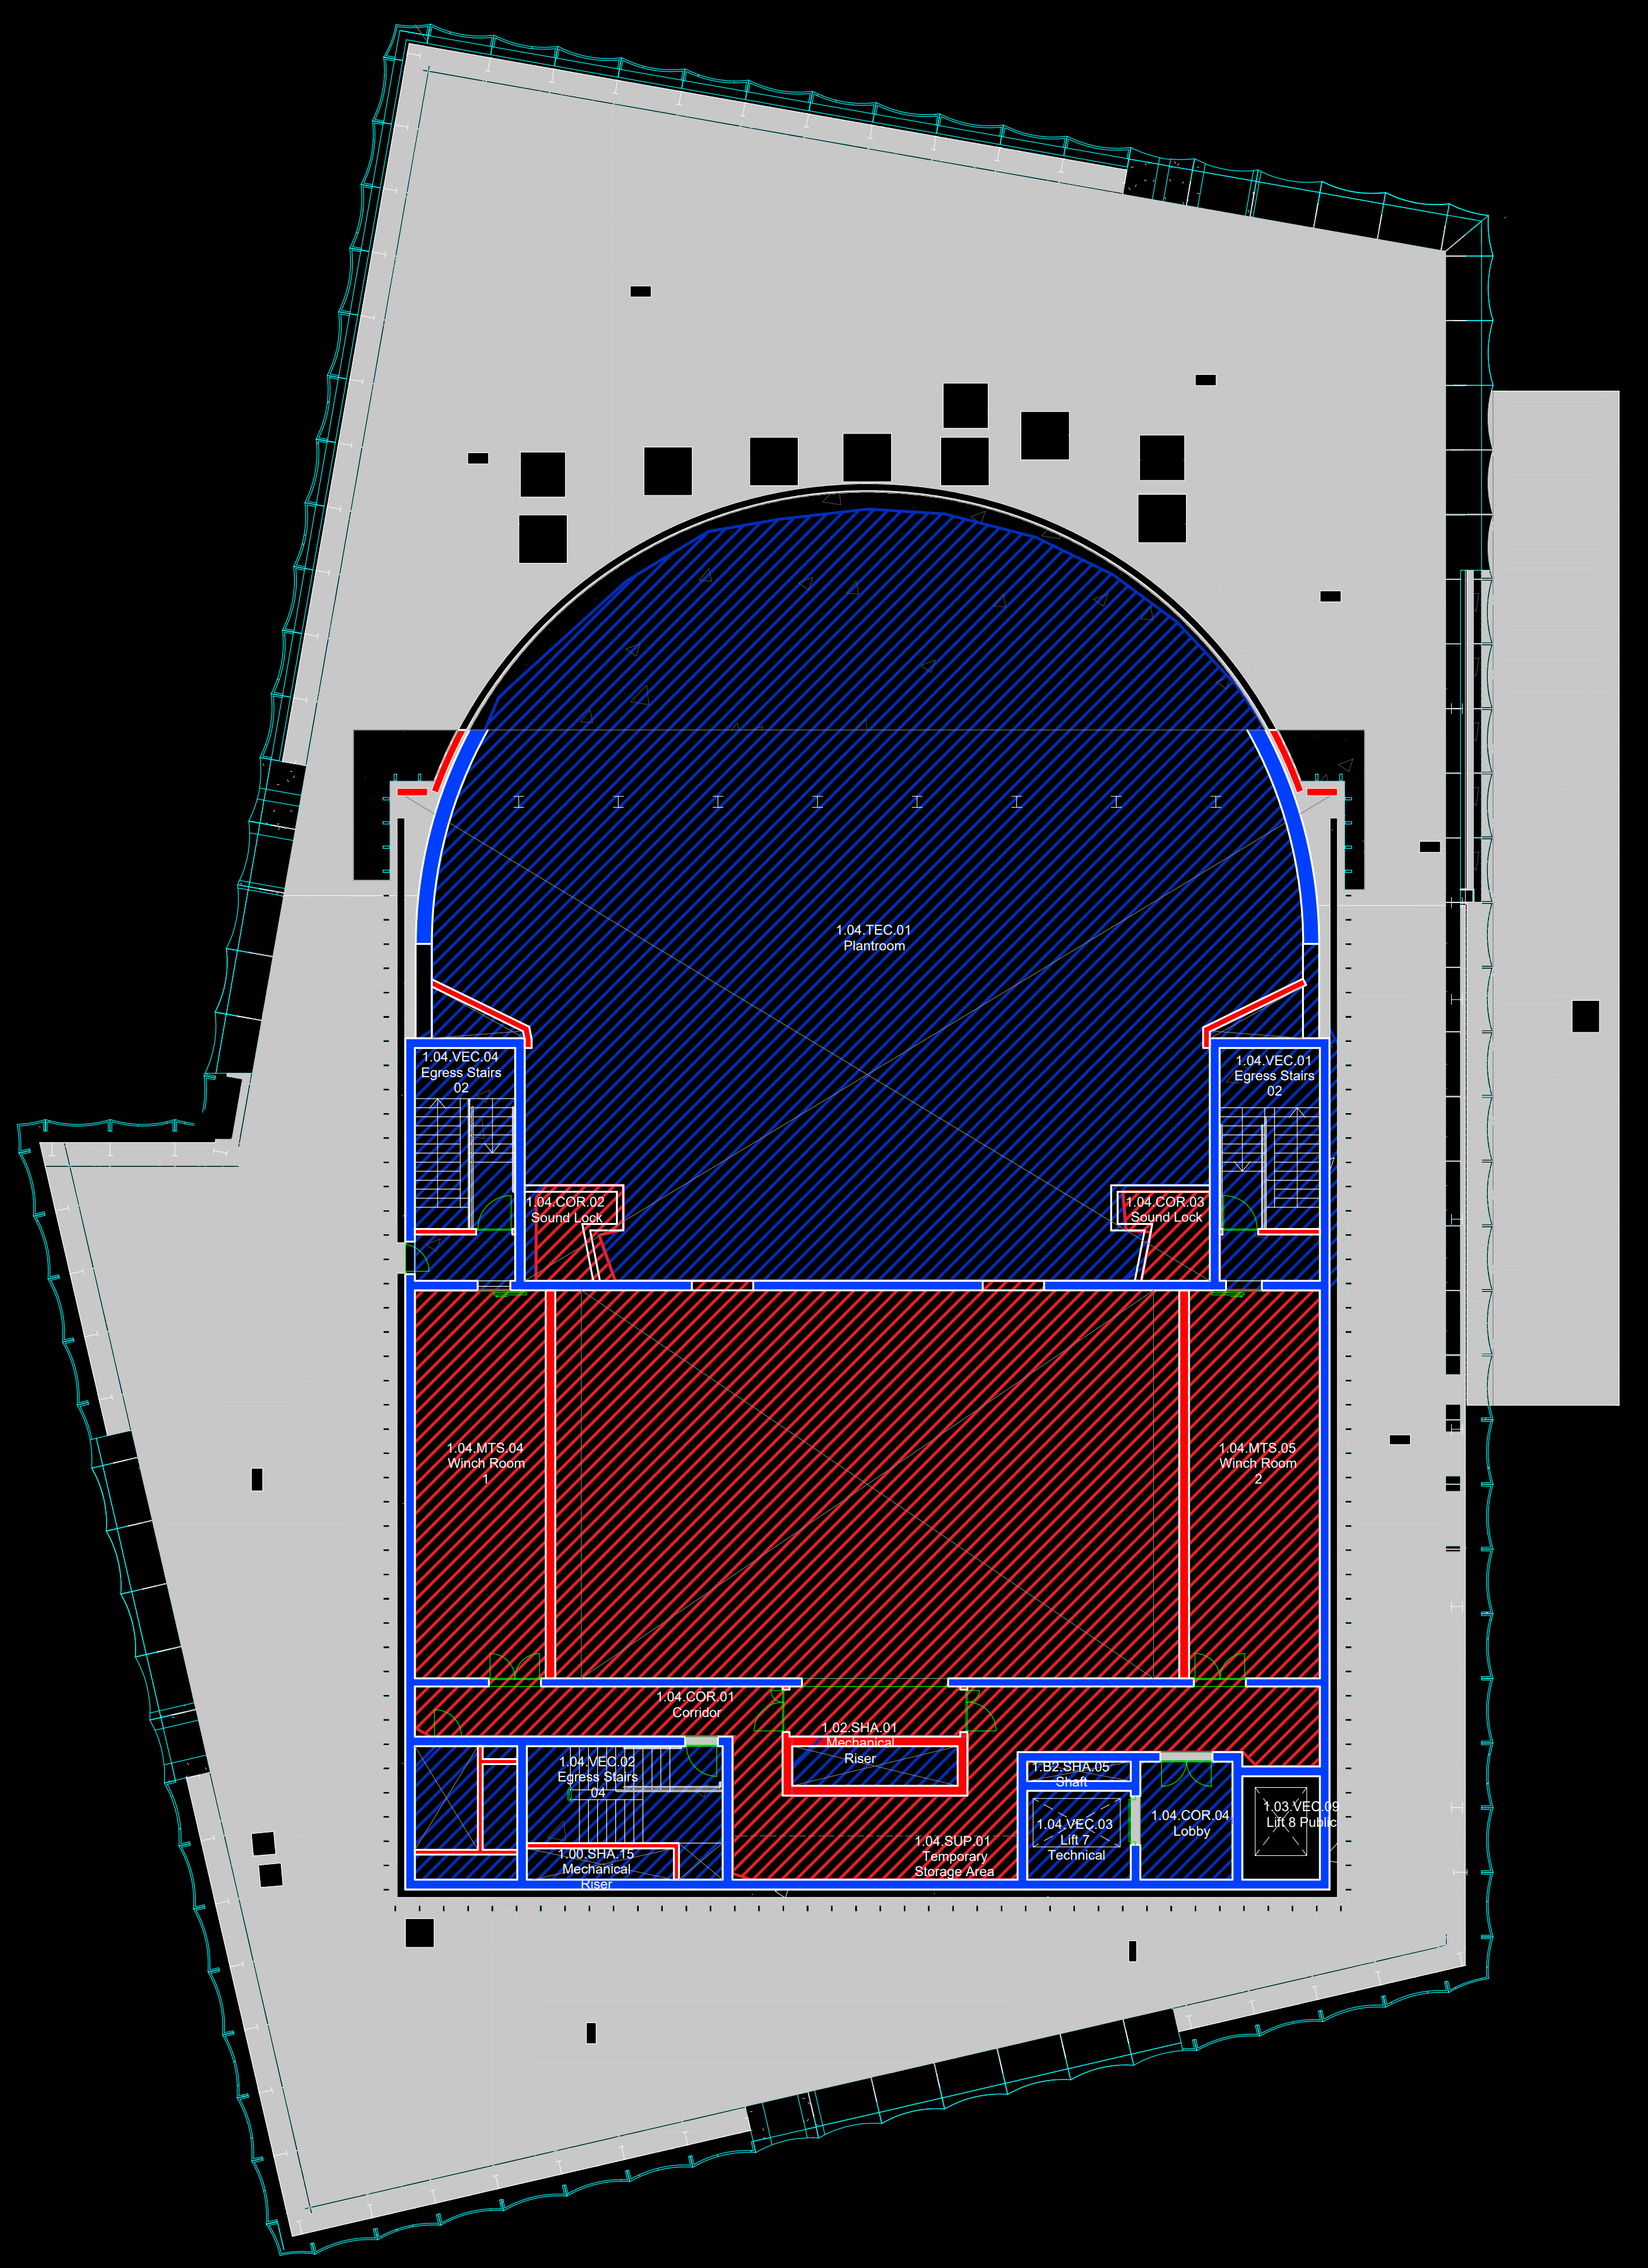

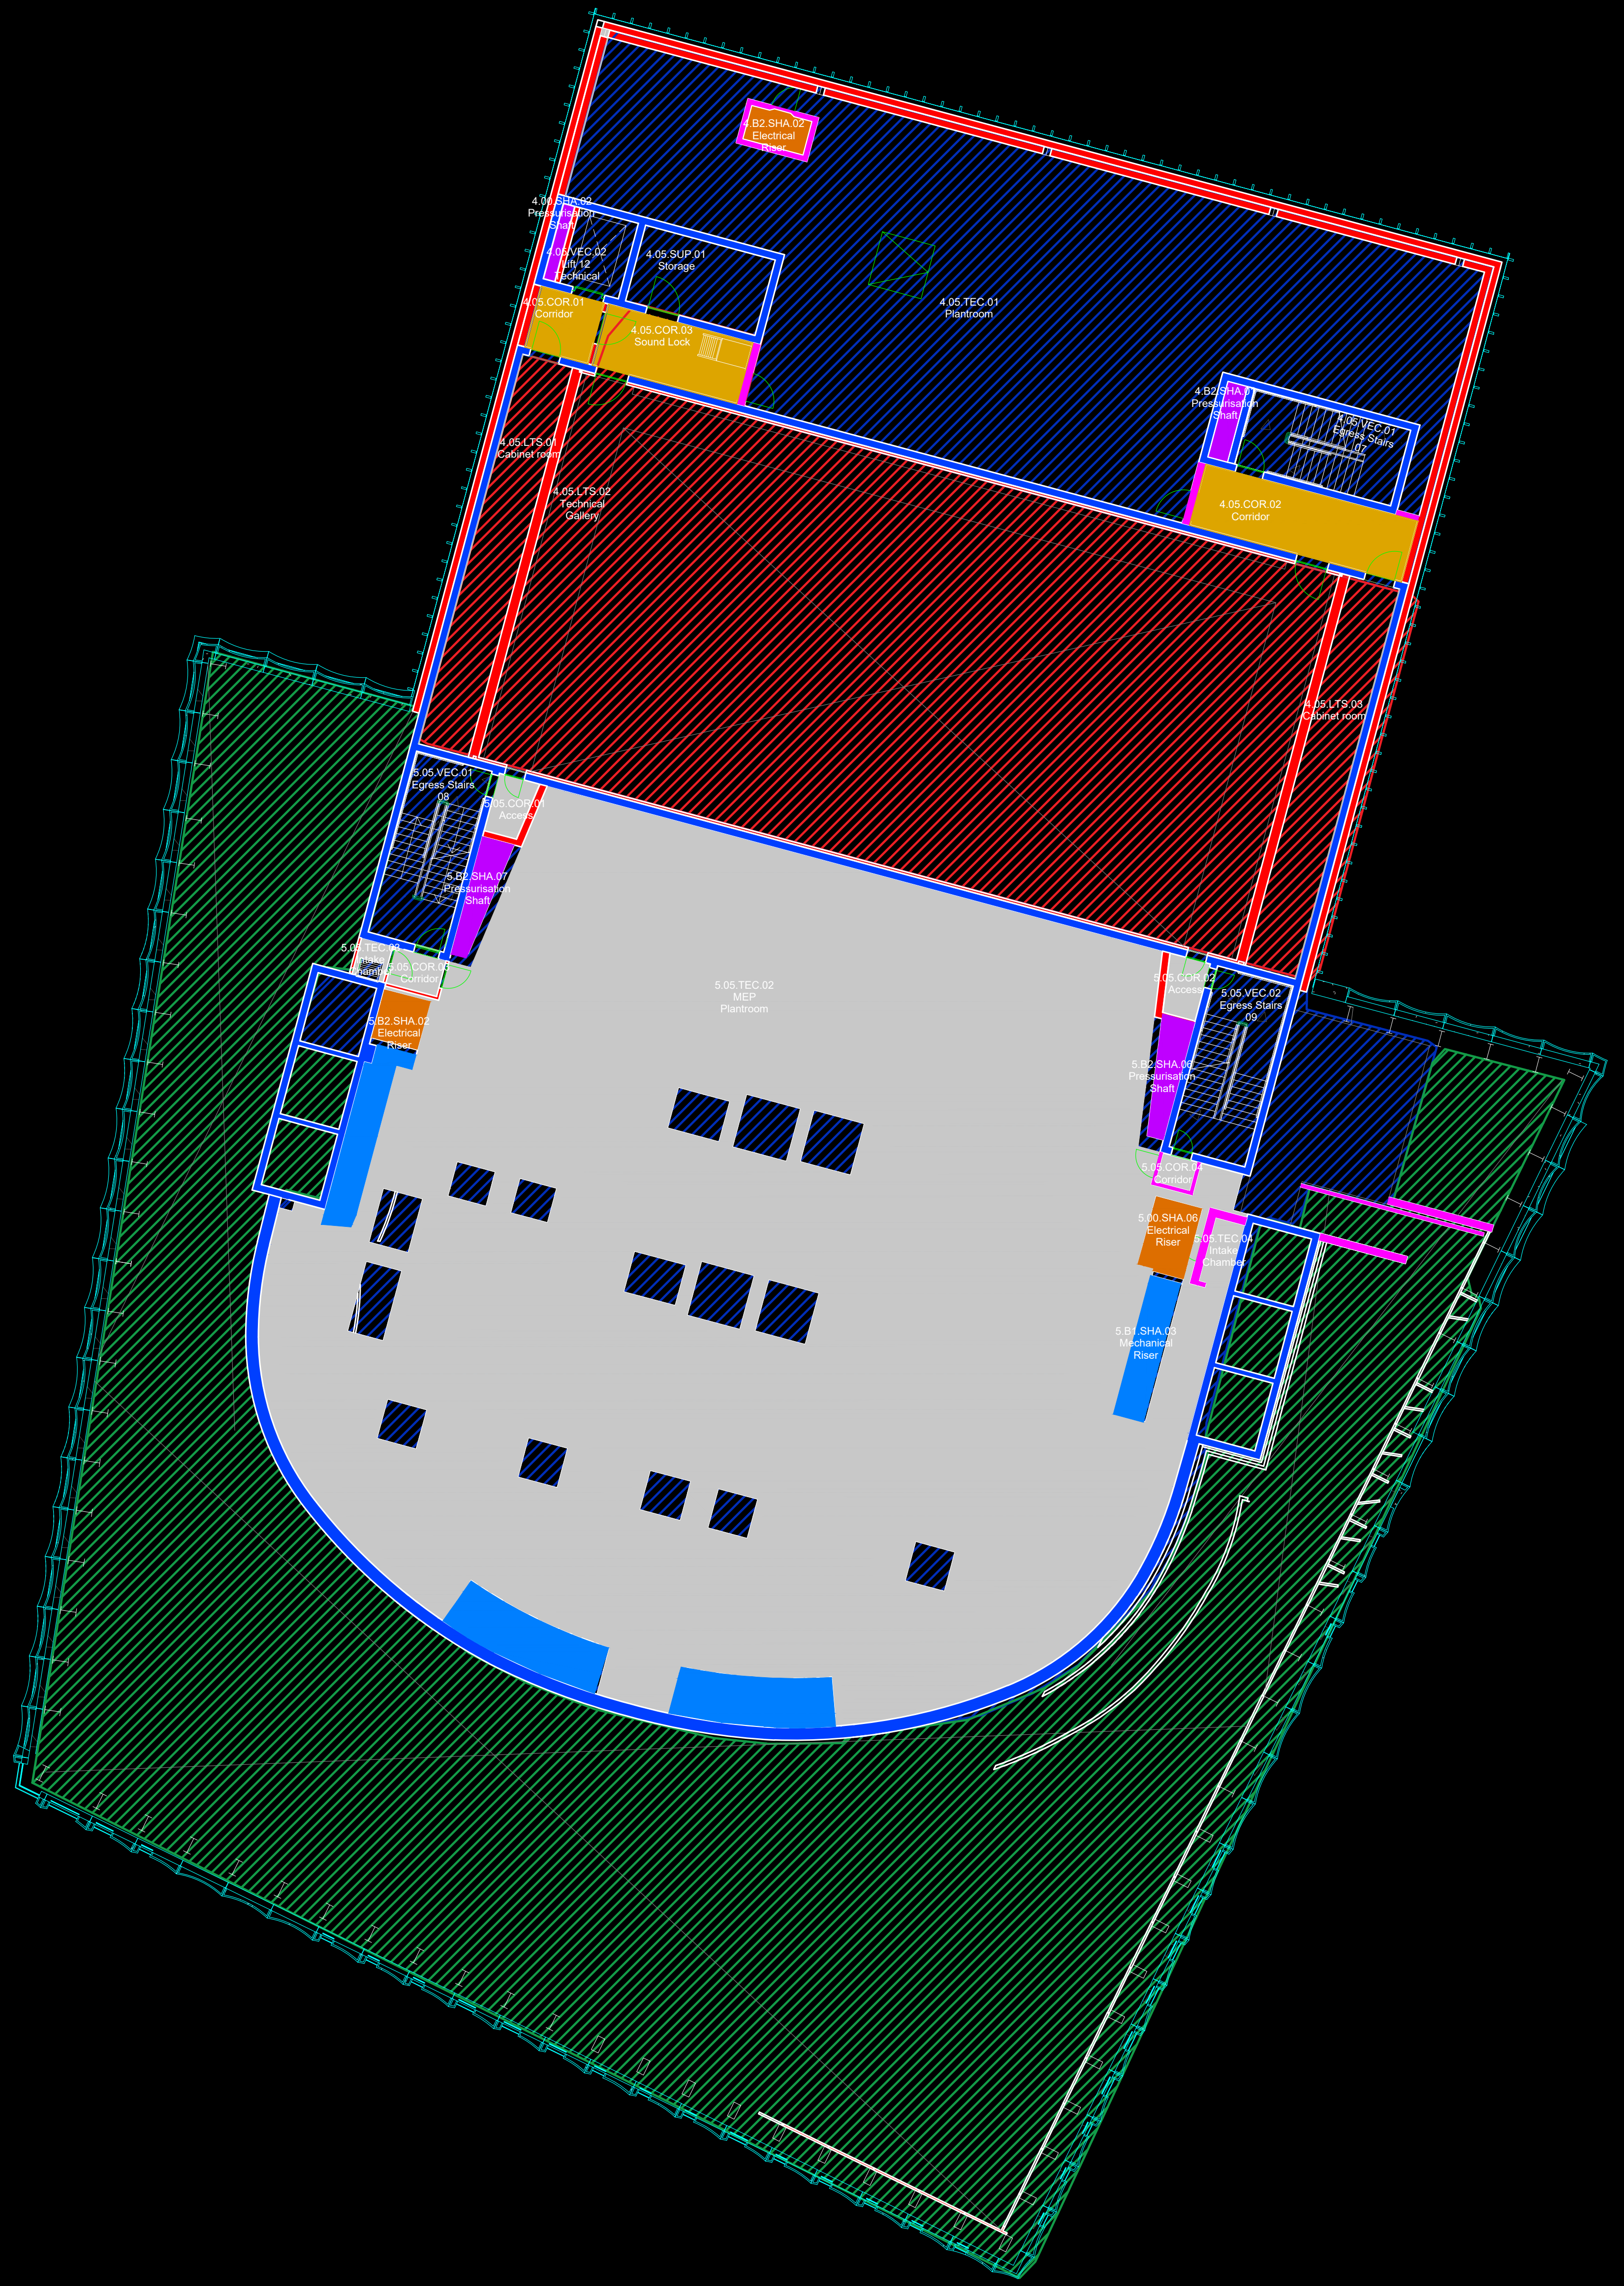

SHAFTS & RISERS LEGEND - PARTS 4 & 5

🟦 **MECHANICAL RISER**
HVAC ducts, chilled water, plumbing and fire-fighting pipes.
On this plan: 5.B1.SHA.03

🟧 **ELECTRICAL RISER**
LV trays, busbars, DBs and ELV containment. Grating floors.
On this plan: 4.B2.SHA.02, 5.B2.SHA.02

🟪 **PRESSURISATION SHAFT**
Stair / lift lobby pressurisation ducts.
On this plan: 4.00.SHA.02, 4.B2.SHA.01

🟨 **DC11 CEILING - ACOUSTIC ROCK WOOL**
Acoustic rock wool, mineral fibre panel.

JOH-HLA-S4-01-056-XXX-05-DR-AR-011150