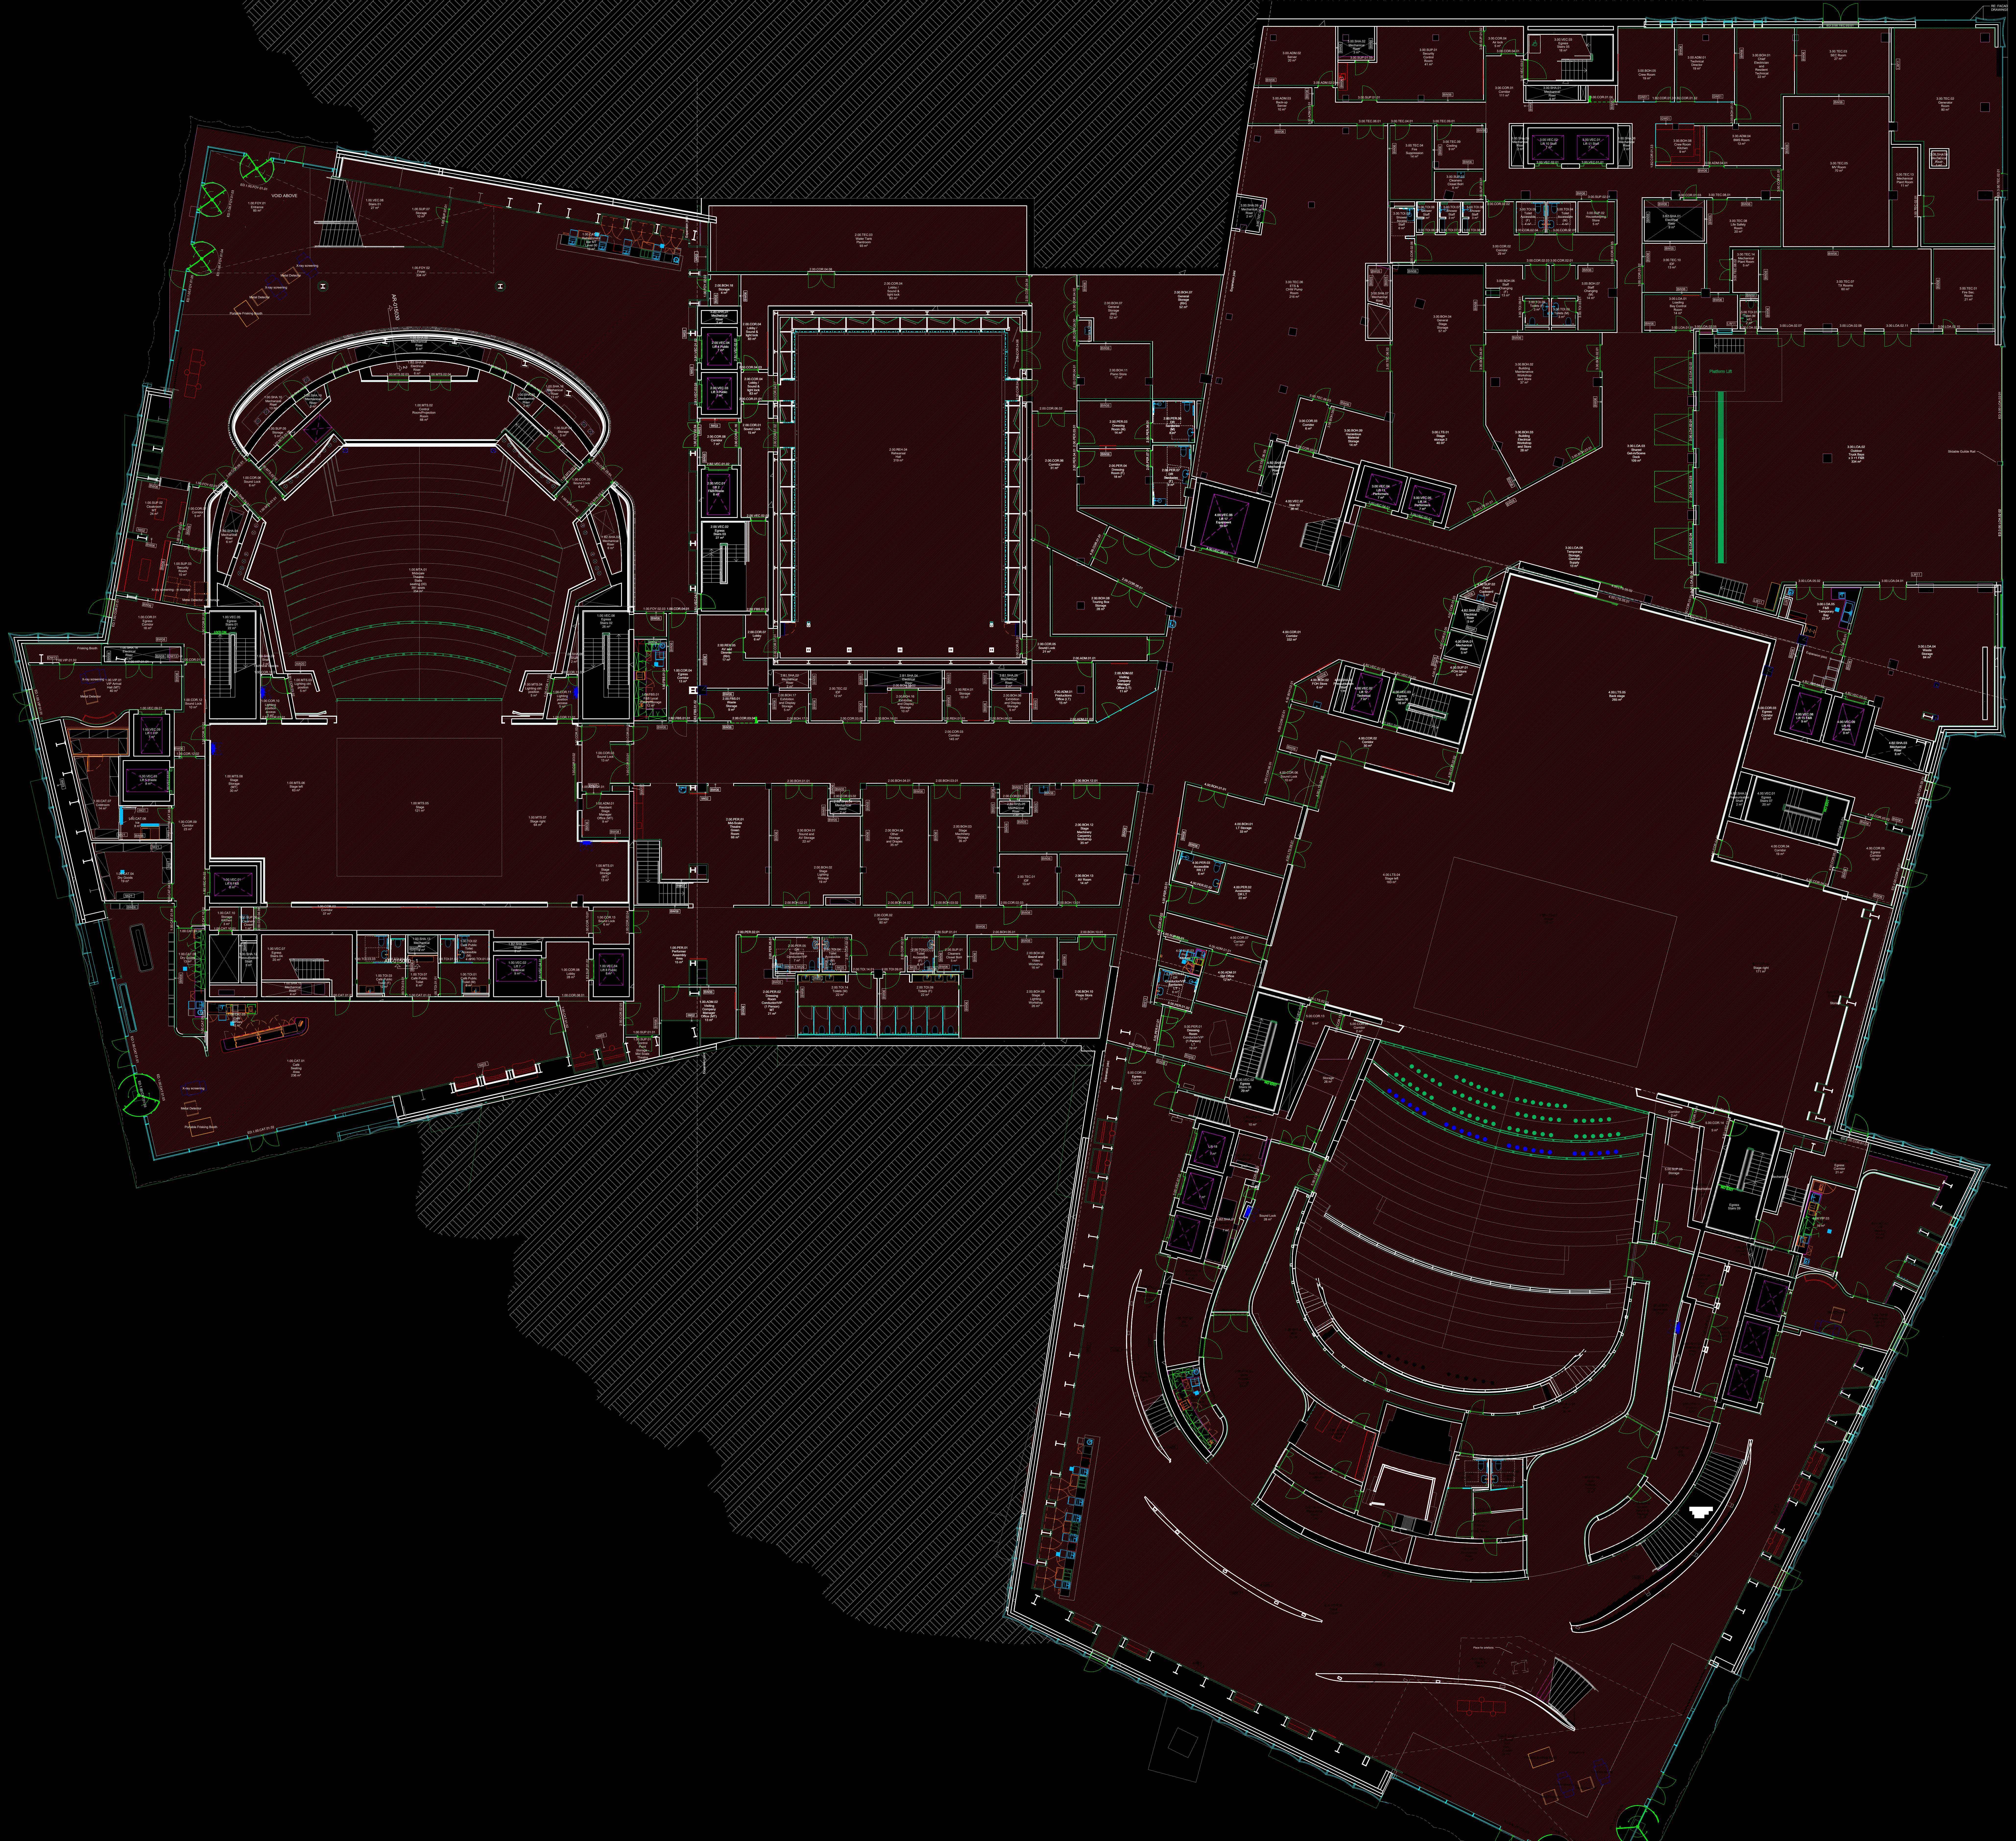
VOID ABOVE
ED.1.00.FOY.01.01
1.00.FOY.01 Entrance 85 m²
ED.1.00.FOY.01.03
ED.1.00.FOY.01.04
ED.1.00.FOY.01.05
1.00.VEC.08 Stairs 01 27 m²
1.00.SUP.07 Storage 10 m²
1.00.SUP.07.01
1.00.CAT.02 Refreshment Bar MT Level 00 19 m²
Expansion joint
1.00.FOY.02 Foyer 334 m²
X-ray screening
Metal Detector
Portable Frisking Booth
AR-015030
1.00.SHA.03 Mechanical Riser 8 m²
1.B2.SHA.08 Electrical Riser 6 m²
1.00.MTS.02.03
1.00.MTS.02.04
1.00.SHA.10 Mechanical Riser 13 m²
1.00.SHA.19 Mechanical Riser 2 m²
1.00.SHA.16 Mechanical Riser 13 m²
1.00.SHA.20 Mechanical Riser 2 m²
1.00.MTS.02 Control Room/Projection Room 68 m²
1.00.SUP.05 Storage 5 m²
1.00.SUP.04 Storage 5 m²
1.00.COR.06 Sound Lock 6 m²
1.00.COR.05 Sound Lock 6 m²
1.00.SUP.02 Cloakroom MT 24 m²
1.00.COR.07 Corridor 5 m²
1.00.SUP.03 Security Room 10 m²
X-ray screening - in storage
Metal Detector - in storage
1.B2.SHA.04 Mechanical Riser 6 m²
1.B2.SHA.02 Mechanical Riser 6 m²
1.00.MTA.01 Midscale Theatre Stalls seating (00) 391 seats 354 m²
1.00.VEC.05 Egress Stairs 01 22 m²
1.00.VEC.06 Egress Stairs 02 26 m²
NO EXIT
1.00.SHA.09 Shaft 2 m²
1.00.SHA.06 Shaft 2 m²
Technical Spaces
1.00.MTS.03 Lighting ctrl. position 5 m²
1.00.MTS.04 Lighting ctrl. position 5 m²
1.00.COR.10 Lighting position access 5 m²
1.00.COR.11 Lighting position access 5 m²
1.00.COR.12 Sound Lock 10 m²
1.00.VEC.09 Lift 1 VIP 7 m²
1.00.VEC.03 Waste 8 m²
1.00.MTS.08 Stage Storage (MT) 30 m²
1.00.MTS.06 Stage left 63 m²
1.00.MTS.05 Stage 121 m²
1.00.MTS.07 Stage right 64 m²
1.00.MTS.01 Stage Storage (MT) 13 m²
1.00.COR.09 Corridor 23 m²
1.00.VEC.01 Lift 6 F&B 8 m²
1.00.COR.02
1.00.COR.03 Sound Lock 13 m²
1.00.ADM.01 Resident Stage Manager Office (MT) 9 m²
1.00.FBS.01 F&B Local Pantry/Storage 12 m²
1.00.COR.04 Egress Corridor 13 m²
2.00.BOH.18 Storage 4 m²
2.00.SHA.01 Mechanical Riser 2 m²
2.00.VEC.04 Lift 4 Public 7 m²
2.00.VEC.03 Lift 3 Public 7 m²
2.00.COR.08 Corridor 7 m²
2.00.VEC.01 Lift 2 F&B/Waste 8 m²
2.00.VEC.02 Egress Stairs 03 27 m²
2.00.REH.05 AV and Dimmer (RH) 17 m²
2.00.FBS.01 Waste Storage 9 m²
2.00.PER.01 Mid-Scale Theatre Green Room 66 m²
Get-in/Scene Dock 109 m²
Truck Bays x 3 +1 F&B 334 m²
4.B2.SHA.04 Mechanical Riser 3 m²
4.00.VEC.06 Lift 17 Equipment 19 m²
4.00.VEC.07 Stair 02 36 m²
3.00.VEC.04 Lift 13 Performers 7 m²
3.00.VEC.05 Lift 14 Performers 7 m²
3.00.LOA.06 Temporary Storage, General Supply 13 m²
4.00.SUP.02 Paint Cupboard 3 m²
4.B2.SHA.02 Electrical Riser 5 m²
4.00.SHA.01 Mechanical Riser 5 m²
4.00.SUP.01 FOH Store 5 m²
4.00.COR.01 Corridor 332 m²
4.00.BOH.02 FOH Store 6 m²
4.00.SHA.02 Pressurisation Shaft 1 m²
4.00.VEC.02 Lift 12 Technical 7 m²
4.00.VEC.03 Egress Stairs 06 16 m²
4.00.COR.02 Corridor 30 m²
4.00.COR.06 Sound Lock 10 m²
4.00.LTS.05 Back stage 265 m²
3.00.LOA.05 F&B Temporary Bay 23 m²
3.00.LOA.04 Waste Storage 84 m²
4.00.COR.03 Egress Corridor 55 m²
4.00.VEC.08 Lift 15 F&B 9 m²
4.00.VEC.09 Lift 16 Waste 9 m²
4.B2.SHA.03 Mechanical Riser 6 m²
4.B2.SHA.01 Pressurisation Shaft 2 m²
4.00.VEC.01 Egress Stairs 07 20 m²
4.00.COR.04 Corridor 19 m²
4.00.COR.05 Egress Corridor 19 m²
4.00.BOH.01 LT Storage 33 m²
4.00.PER.02 Accessible DR LT 22 m²
4.00.LTS.04 Stage left 163 m²
Stage right 171 m²
4.00.COR.07 Corridor 11 m²
4.00.ADM.01 SM Office 12 m²
5.00.COR.13 5 m²
5.00.COR Corridor 2 m²
5.00.VEC.02 Egress Stairs 08 29 m²
Storage 26 m²