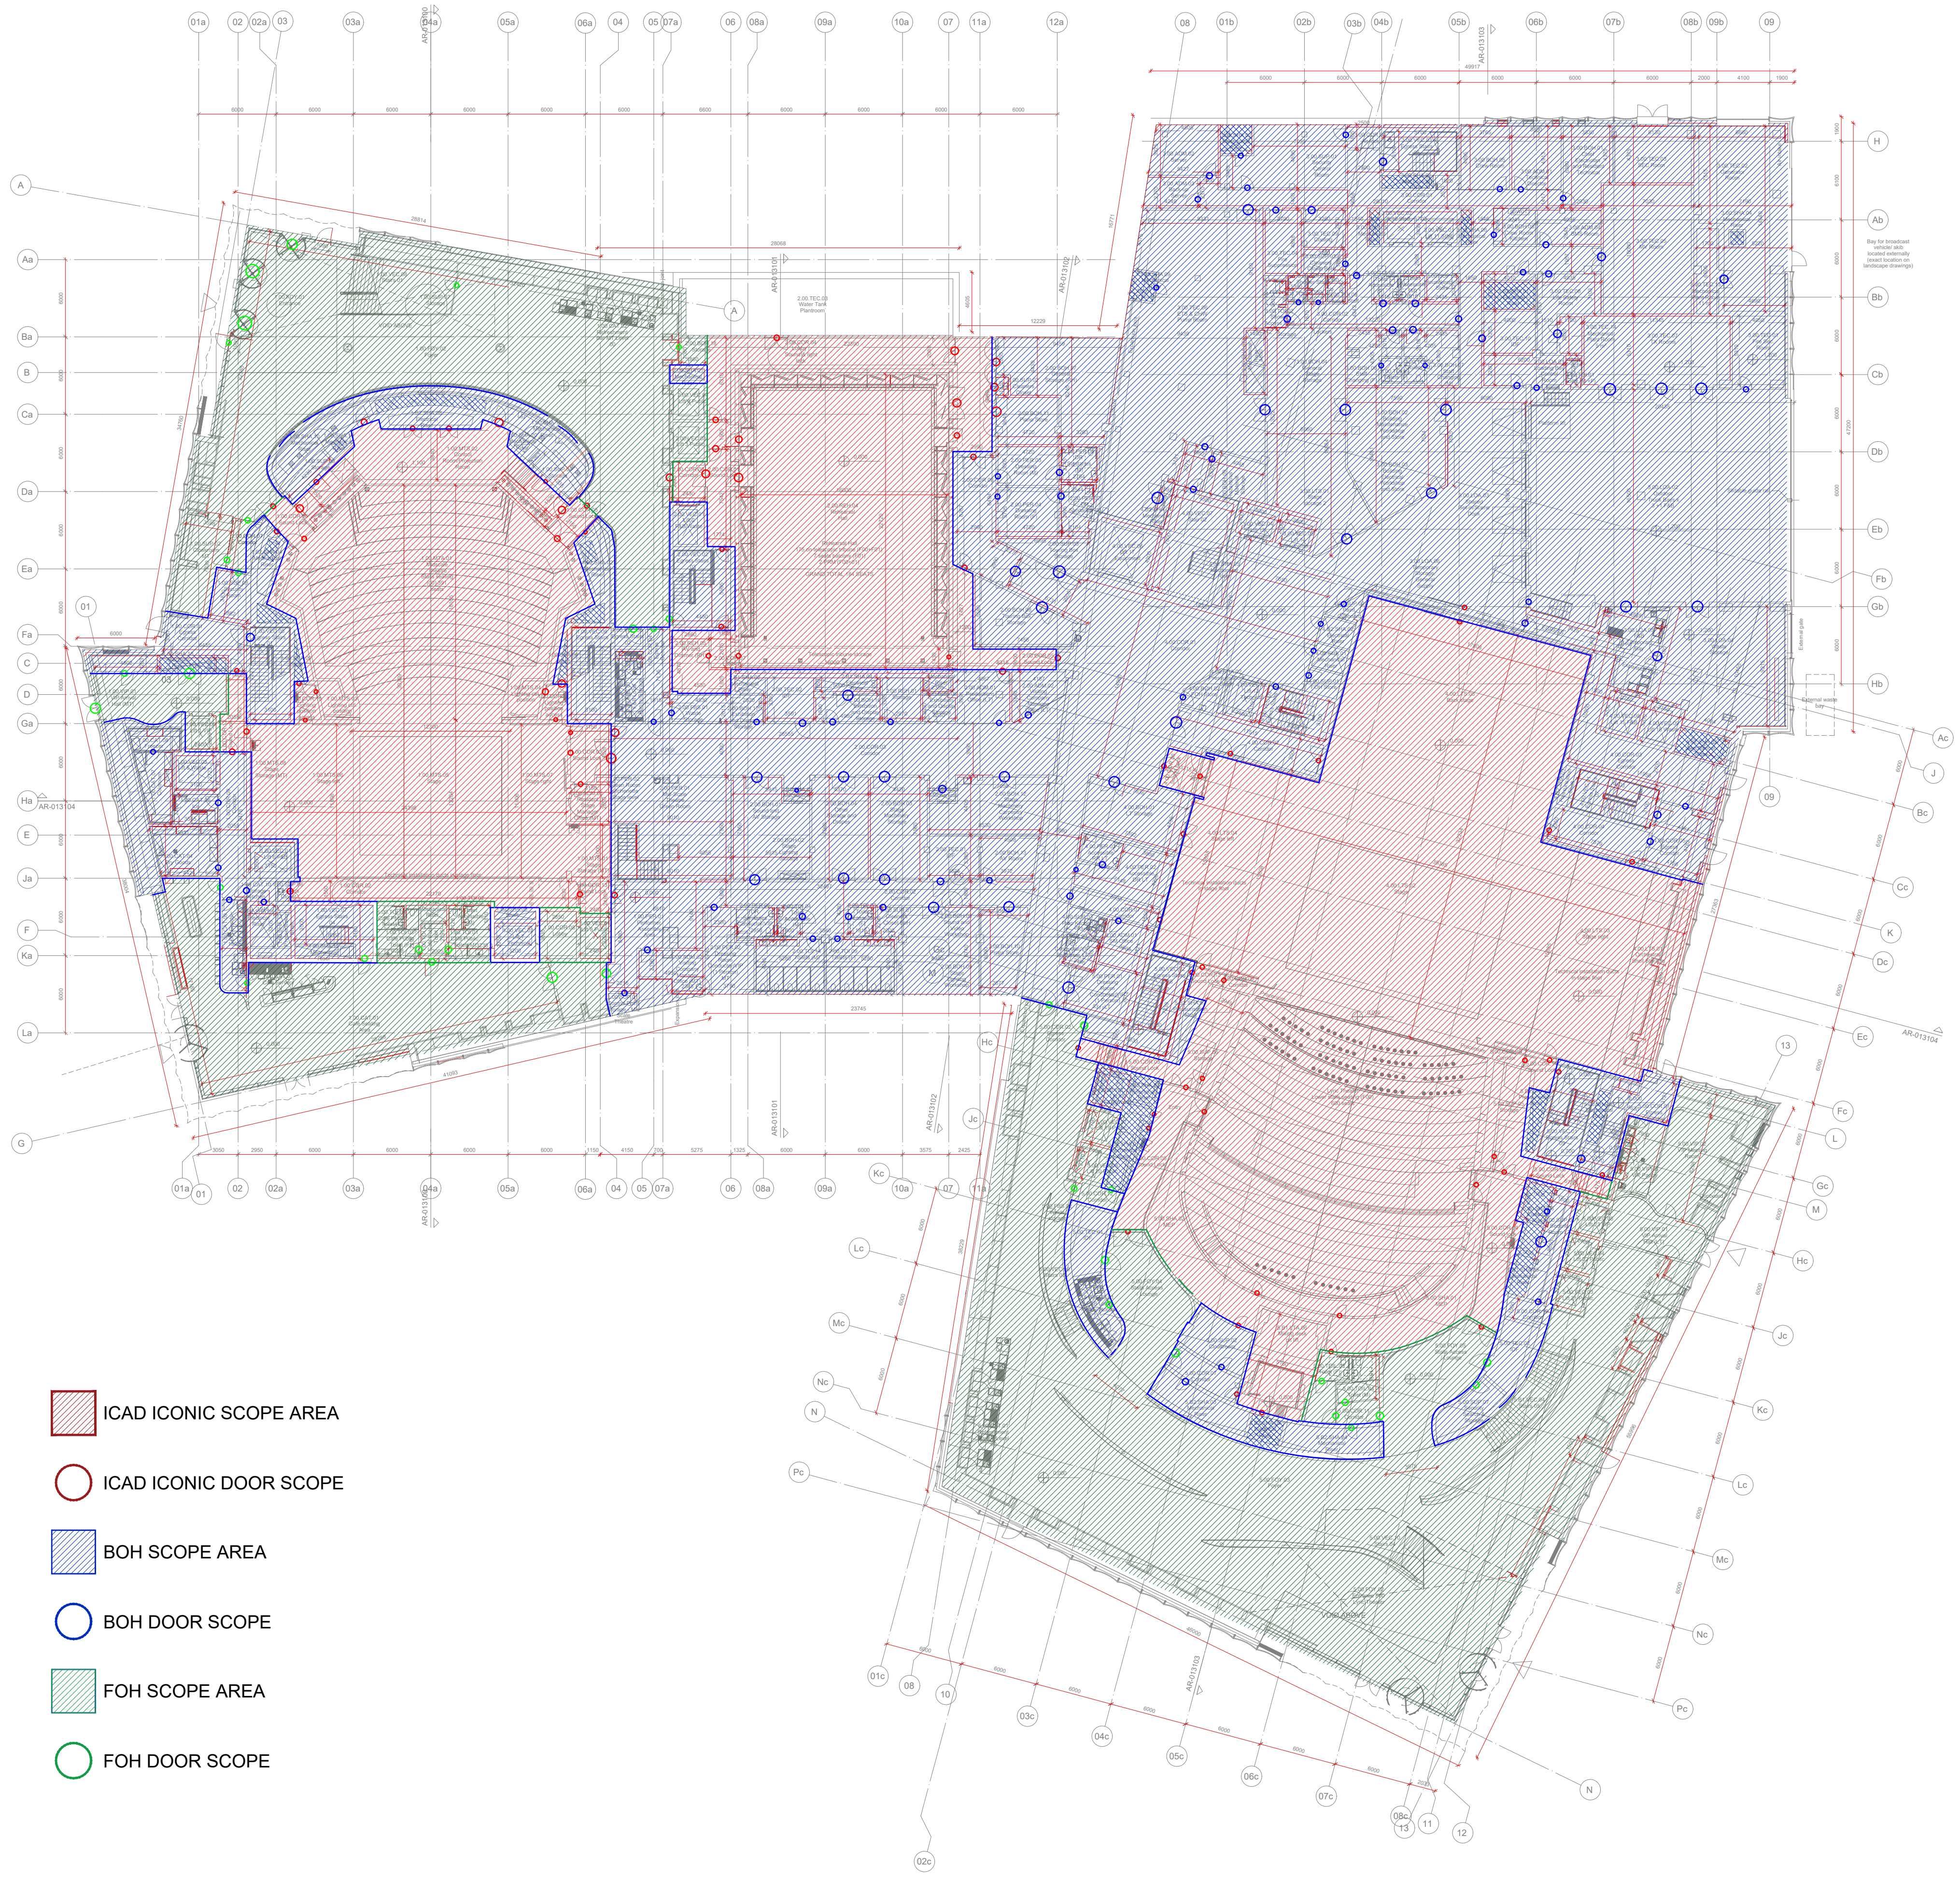

▨ ICAD ICONIC SCOPE AREA

○ ICAD ICONIC DOOR SCOPE

▨ BOH SCOPE AREA

○ BOH DOOR SCOPE

▨ FOH SCOPE AREA

○ FOH DOOR SCOPE

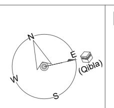

DO NOT SCALE

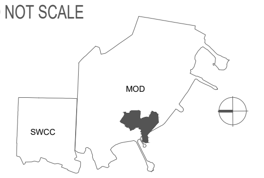

INDEX PLAN

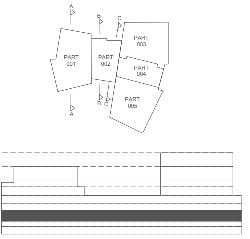

BUILDING KEY PLAN

GENERAL NOTES:

LEGEND & ABBREVIATIONS:

REV	DATE	BY	DESCRIPTION	CHK	APR
F00	31-01-2024	BB	Issued for Construction	LFN	NF

DRAWING STATUS:
Issued for Construction

CLIENT:
C:\Users\TZKA\OneDrive - Ramboll\Desktop\Temp\JOH-HLA-S4-01-056-XXX-ZZ-M3-AR-019300-JCDCLogo-26987616.jpg

LEAD DESIGN CONSULTANTS:
C:\Users\TZKA\OneDrive - Ramboll\Desktop\Temp\JOH-HLA-S4-01-056-XXX-ZZ-M3-AR-019300-HLLogoBlackRGB-26987618.jpg

LEAD ENGINEERING CONSULTANT:
C:\Users\TZKA\OneDrive - Ramboll\Desktop\Temp\JOH-HLA-S4-01-056-XXX-ZZ-M3-AR-019300-BHLogo-26987620.png

GENERAL CONTRACTOR:
GENERAL CONTRACTOR

PROJECT:
JEDDAH OPERA HOUSE

TITLE:
ARCHITECT
PLAN
LEVEL 00

SCALE A0 (841x1189)	CHECKED	APPROVED	MODEL FILE REF
1:200	LFN	NF	JOH-HLA-S4-01-056-XXX-ZZ-M3-AR-019300
PROJECT No:	DESIGNED	DRAWN	DATE:
1960020123	HLA	VCS	31-01-2024

DRAWING NO.: JOH-HLA-S4-01-056-XXX-00-DR-AR-011100
REV: F00

©JCDC