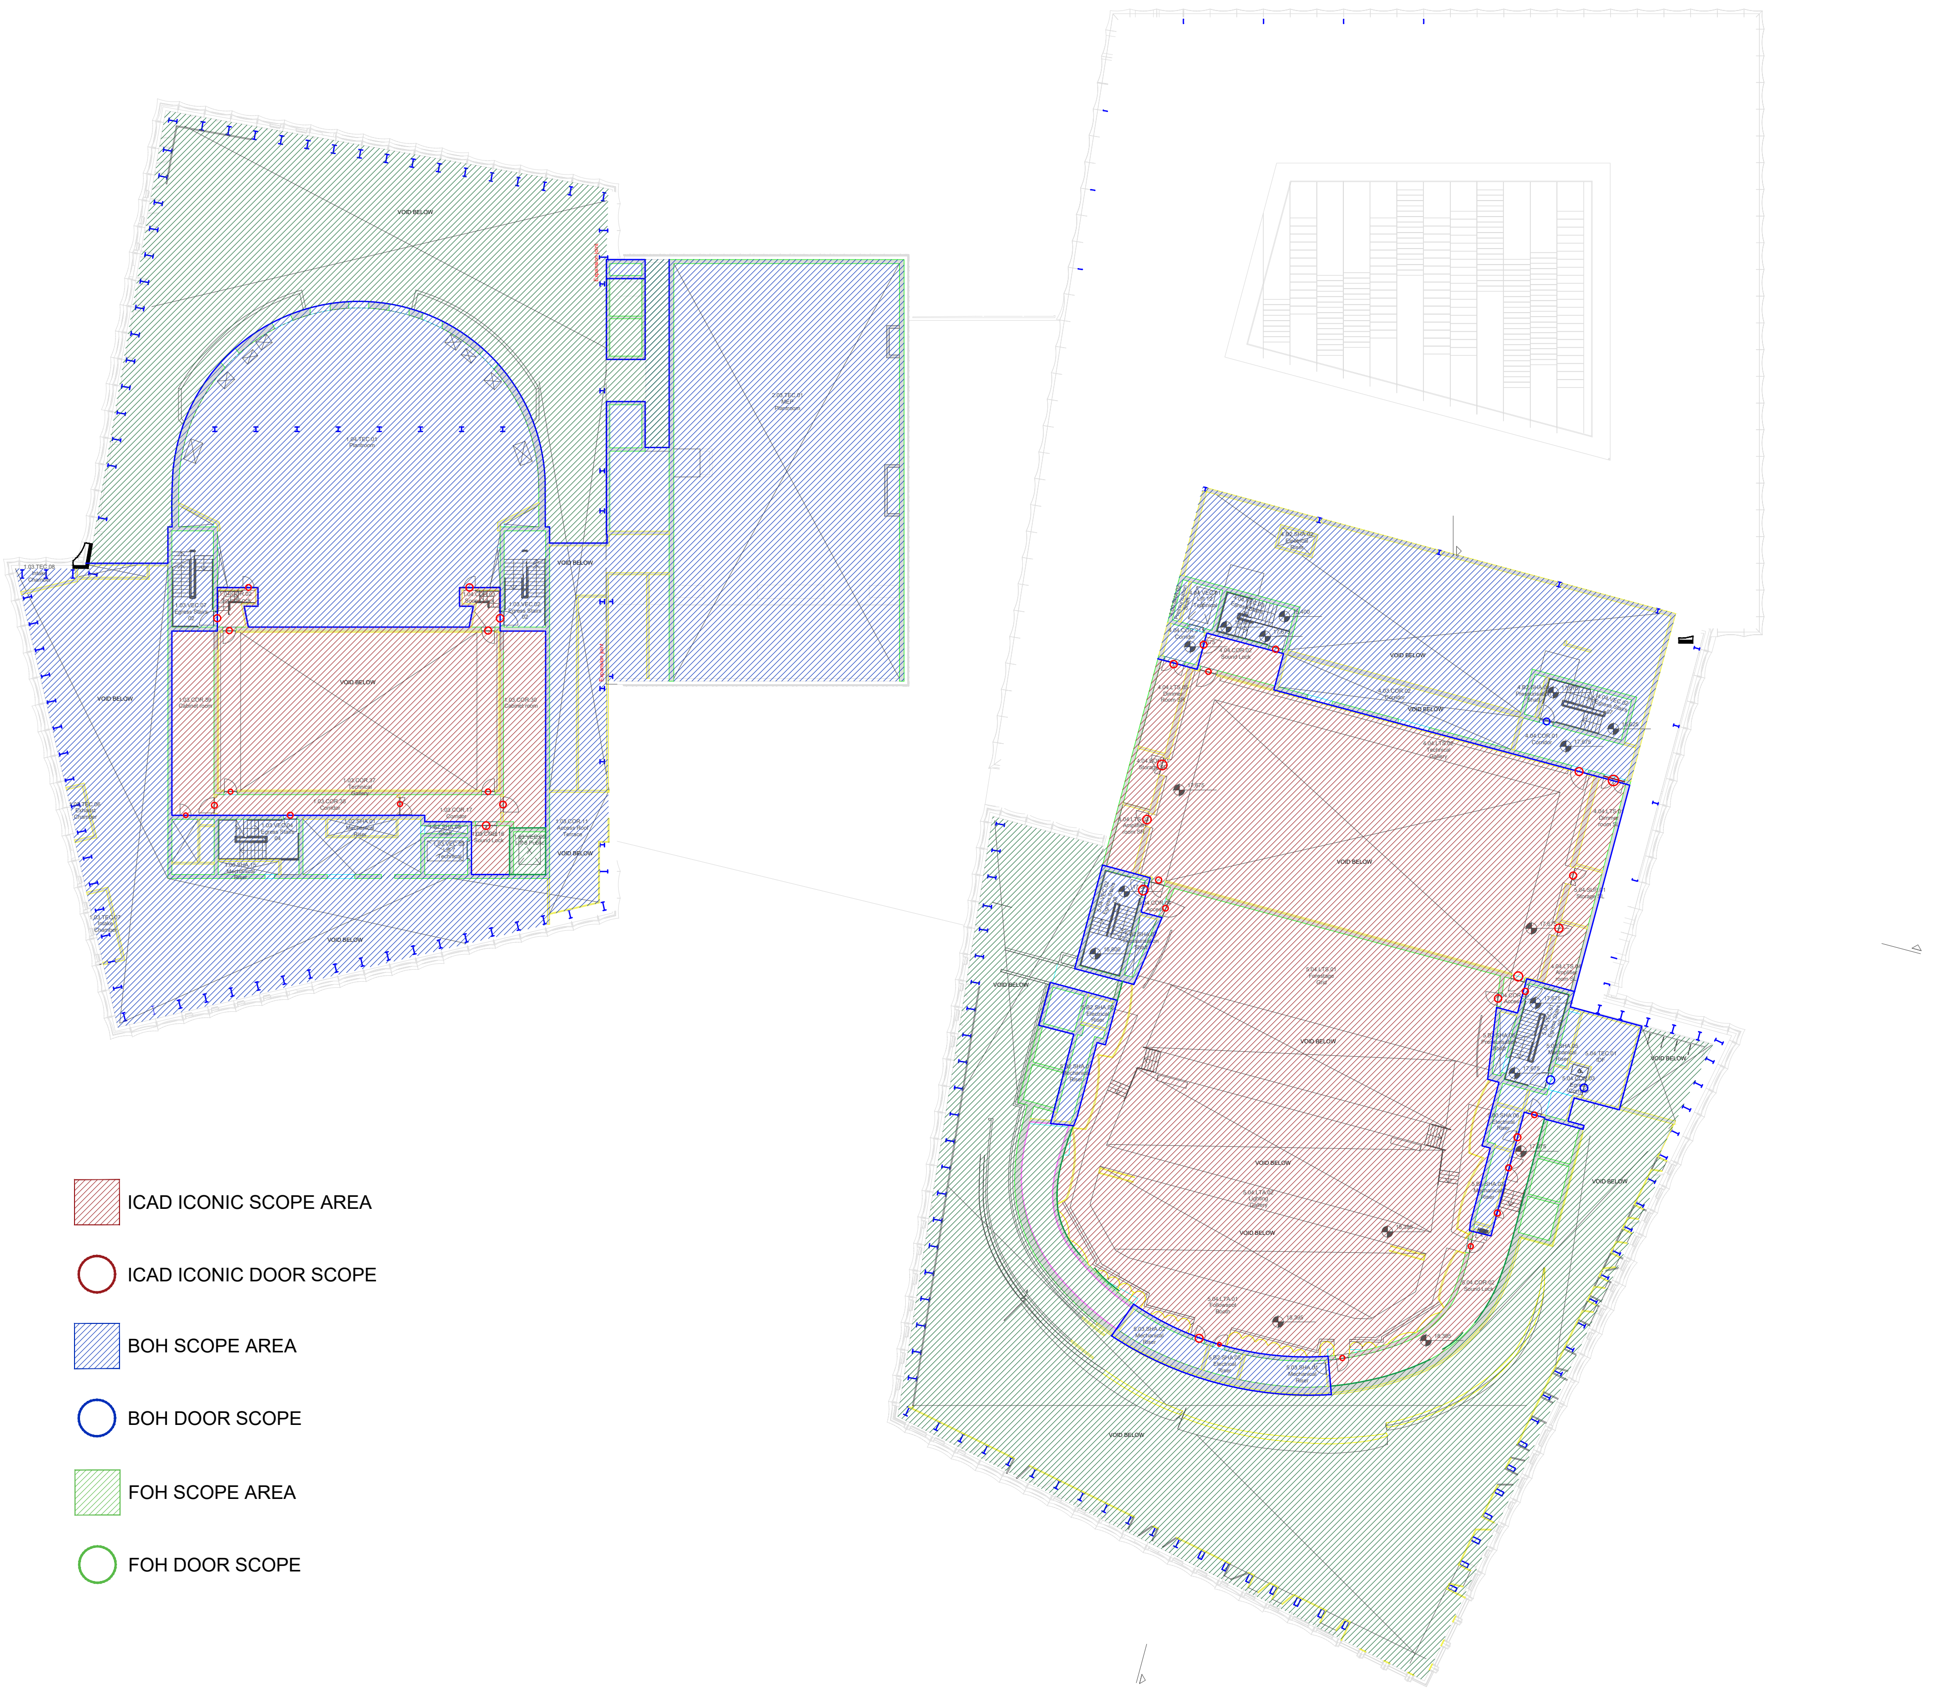

🟥 ICAD ICONIC SCOPE AREA

○ ICAD ICONIC DOOR SCOPE

🟦 BOH SCOPE AREA

○ BOH DOOR SCOPE

🟩 FOH SCOPE AREA

○ FOH DOOR SCOPE

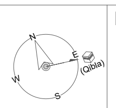

DO NOT SCALE

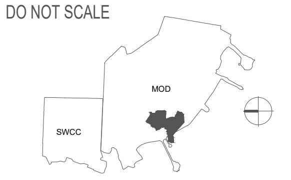

INDEX PLAN

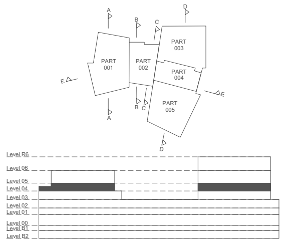

BUILDING KEY PLAN

GENERAL NOTES:

LEGEND & ABBREVIATIONS:

— · — Strutural Floor Expansion Joint

Interior Joint Details:
- JOH-HLA-S4-01-056-XXX-ZZ-DR-AR-015800

See facade detail package for exterior joints

- The line serves as an indicative guide, and the partial plans should be used for accurately establishing the joint line in the finishes.

REV	DATE	BY	DESCRIPTION	CHK	APR
F00	31-01-2024	BB	Issued for Construction	LFN	NF

DRAWING STATUS:
Issued for Construction

CLIENT:
C:\Users\TZKA\OneDrive - Ramboll\Desktop\Temp\JOH-HLA-S4-01-056-XXX-ZZ-M3-AR-019300-JCDCLogo-26987616.jpg

LEAD DESIGN CONSULTANTS:
C:\Users\TZKA\OneDrive - Ramboll\Desktop\Temp\JOH-HLA-S4-01-056-XXX-ZZ-M3-AR-019300-HLLogoBlackRGB-26987618.jpg

LEAD ENGINEERING CONSULTANT:
C:\Users\TZKA\OneDrive - Ramboll\Desktop\Temp\JOH-HLA-S4-01-056-XXX-ZZ-M3-AR-019300-BHlogo-26987620.png

GENERAL CONTRACTOR:
GENERAL CONTRACTOR

PROJECT:
JEDDAH OPERA HOUSE

TITLE:
ARCHITECT
PLAN
LEVEL 04

SCALE A0 (841x1189)	CHECKED	APPROVED	MODEL FILE REF
1:200	LFN	NF	JOH-HLA-S4-01-056-XXX-ZZ-M3-AR-019300
PROJECT No:	DESIGNED	DRAWN	DATE:
1960020123	HLA	VCS	31-01-2024

DRAWING NO.
JOH-HLA-S4-01-056-XXX-04-DR-AR-011140

REV:
F00

©JCDC