

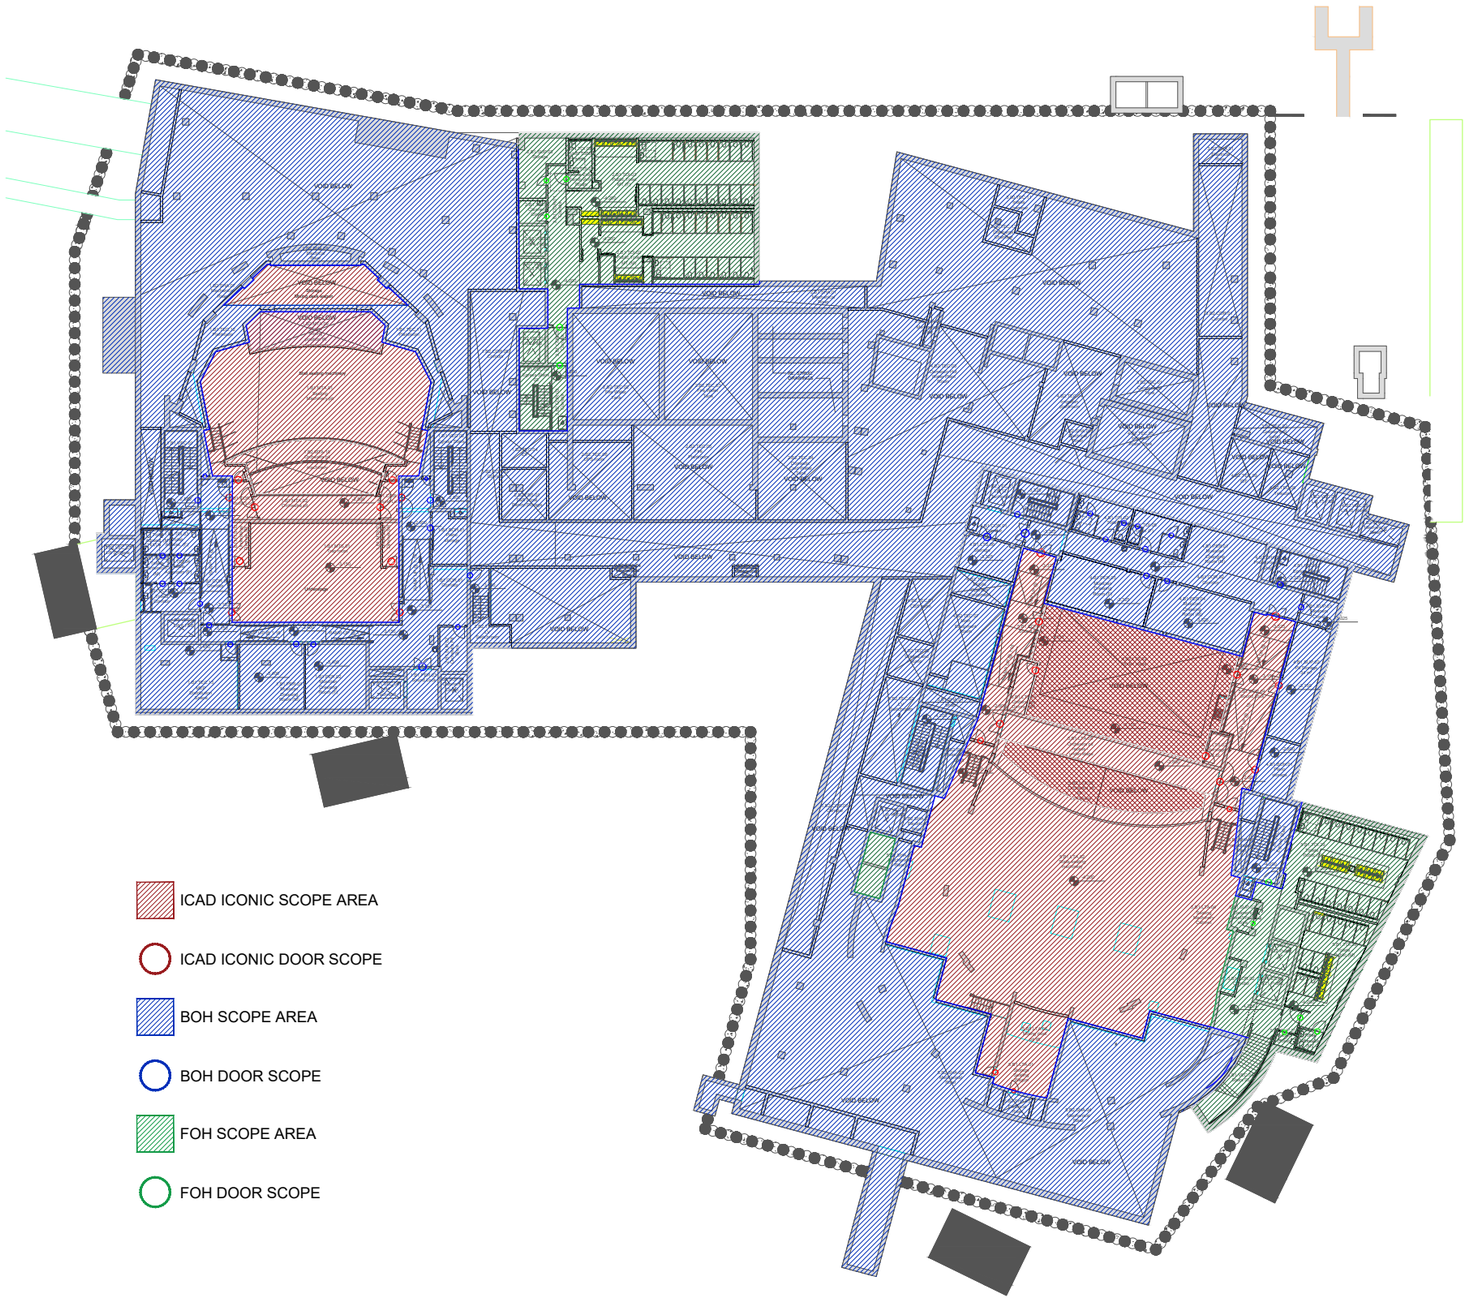


DO NOT SCALE

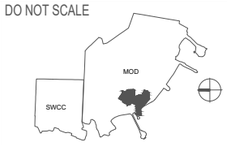

INDEX PLAN

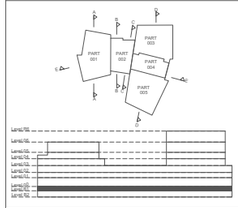

BUILDING KEY PLAN

GENERAL NOTES:

LEGEND & ABBREVIATIONS

Structural Floor Expansion Joint

Interior Joint Details:
- JOH-HLA-S4-01-056-XXX-ZZ-DR-AR-015800

See facade detail package for exterior joints

- The line serves as an indicative guide, and the partial plans should be used for accurately establishing the joint line in the finishes.

REV	DATE	BY	DESCRIPTION	CHK	APR
F00	31-01-2024	BB	Issued for Construction	LFN	NF

DRAWING STATUS: Issued for Construction

CLIENT:

LEAD DESIGN CONSULTANTS:

LEAD ENGINEERING CONSULTANT:

GENERAL CONTRACTOR: GENERAL CONTRACTOR

PROJECT: JEDDAH OPERA HOUSE

TITLE: ARCHITECT PLAN LEVEL B1

SCALE A0 (841x1189)	CHECKED	APPROVED	MODEL FILE REF
1:200	LFN	NF	JOH-HLA-S4-01-056-XXX-ZZ-M3-AR-015000
PROJECT No:	DESIGNED	DRAWN	DATE:
1960020123	HLA	VCS	31-01-2024

DRAWING NO: JOH-HLA-S4-01-056-XXX-B1-DR-AR-011180 REV: F00

©JCDC