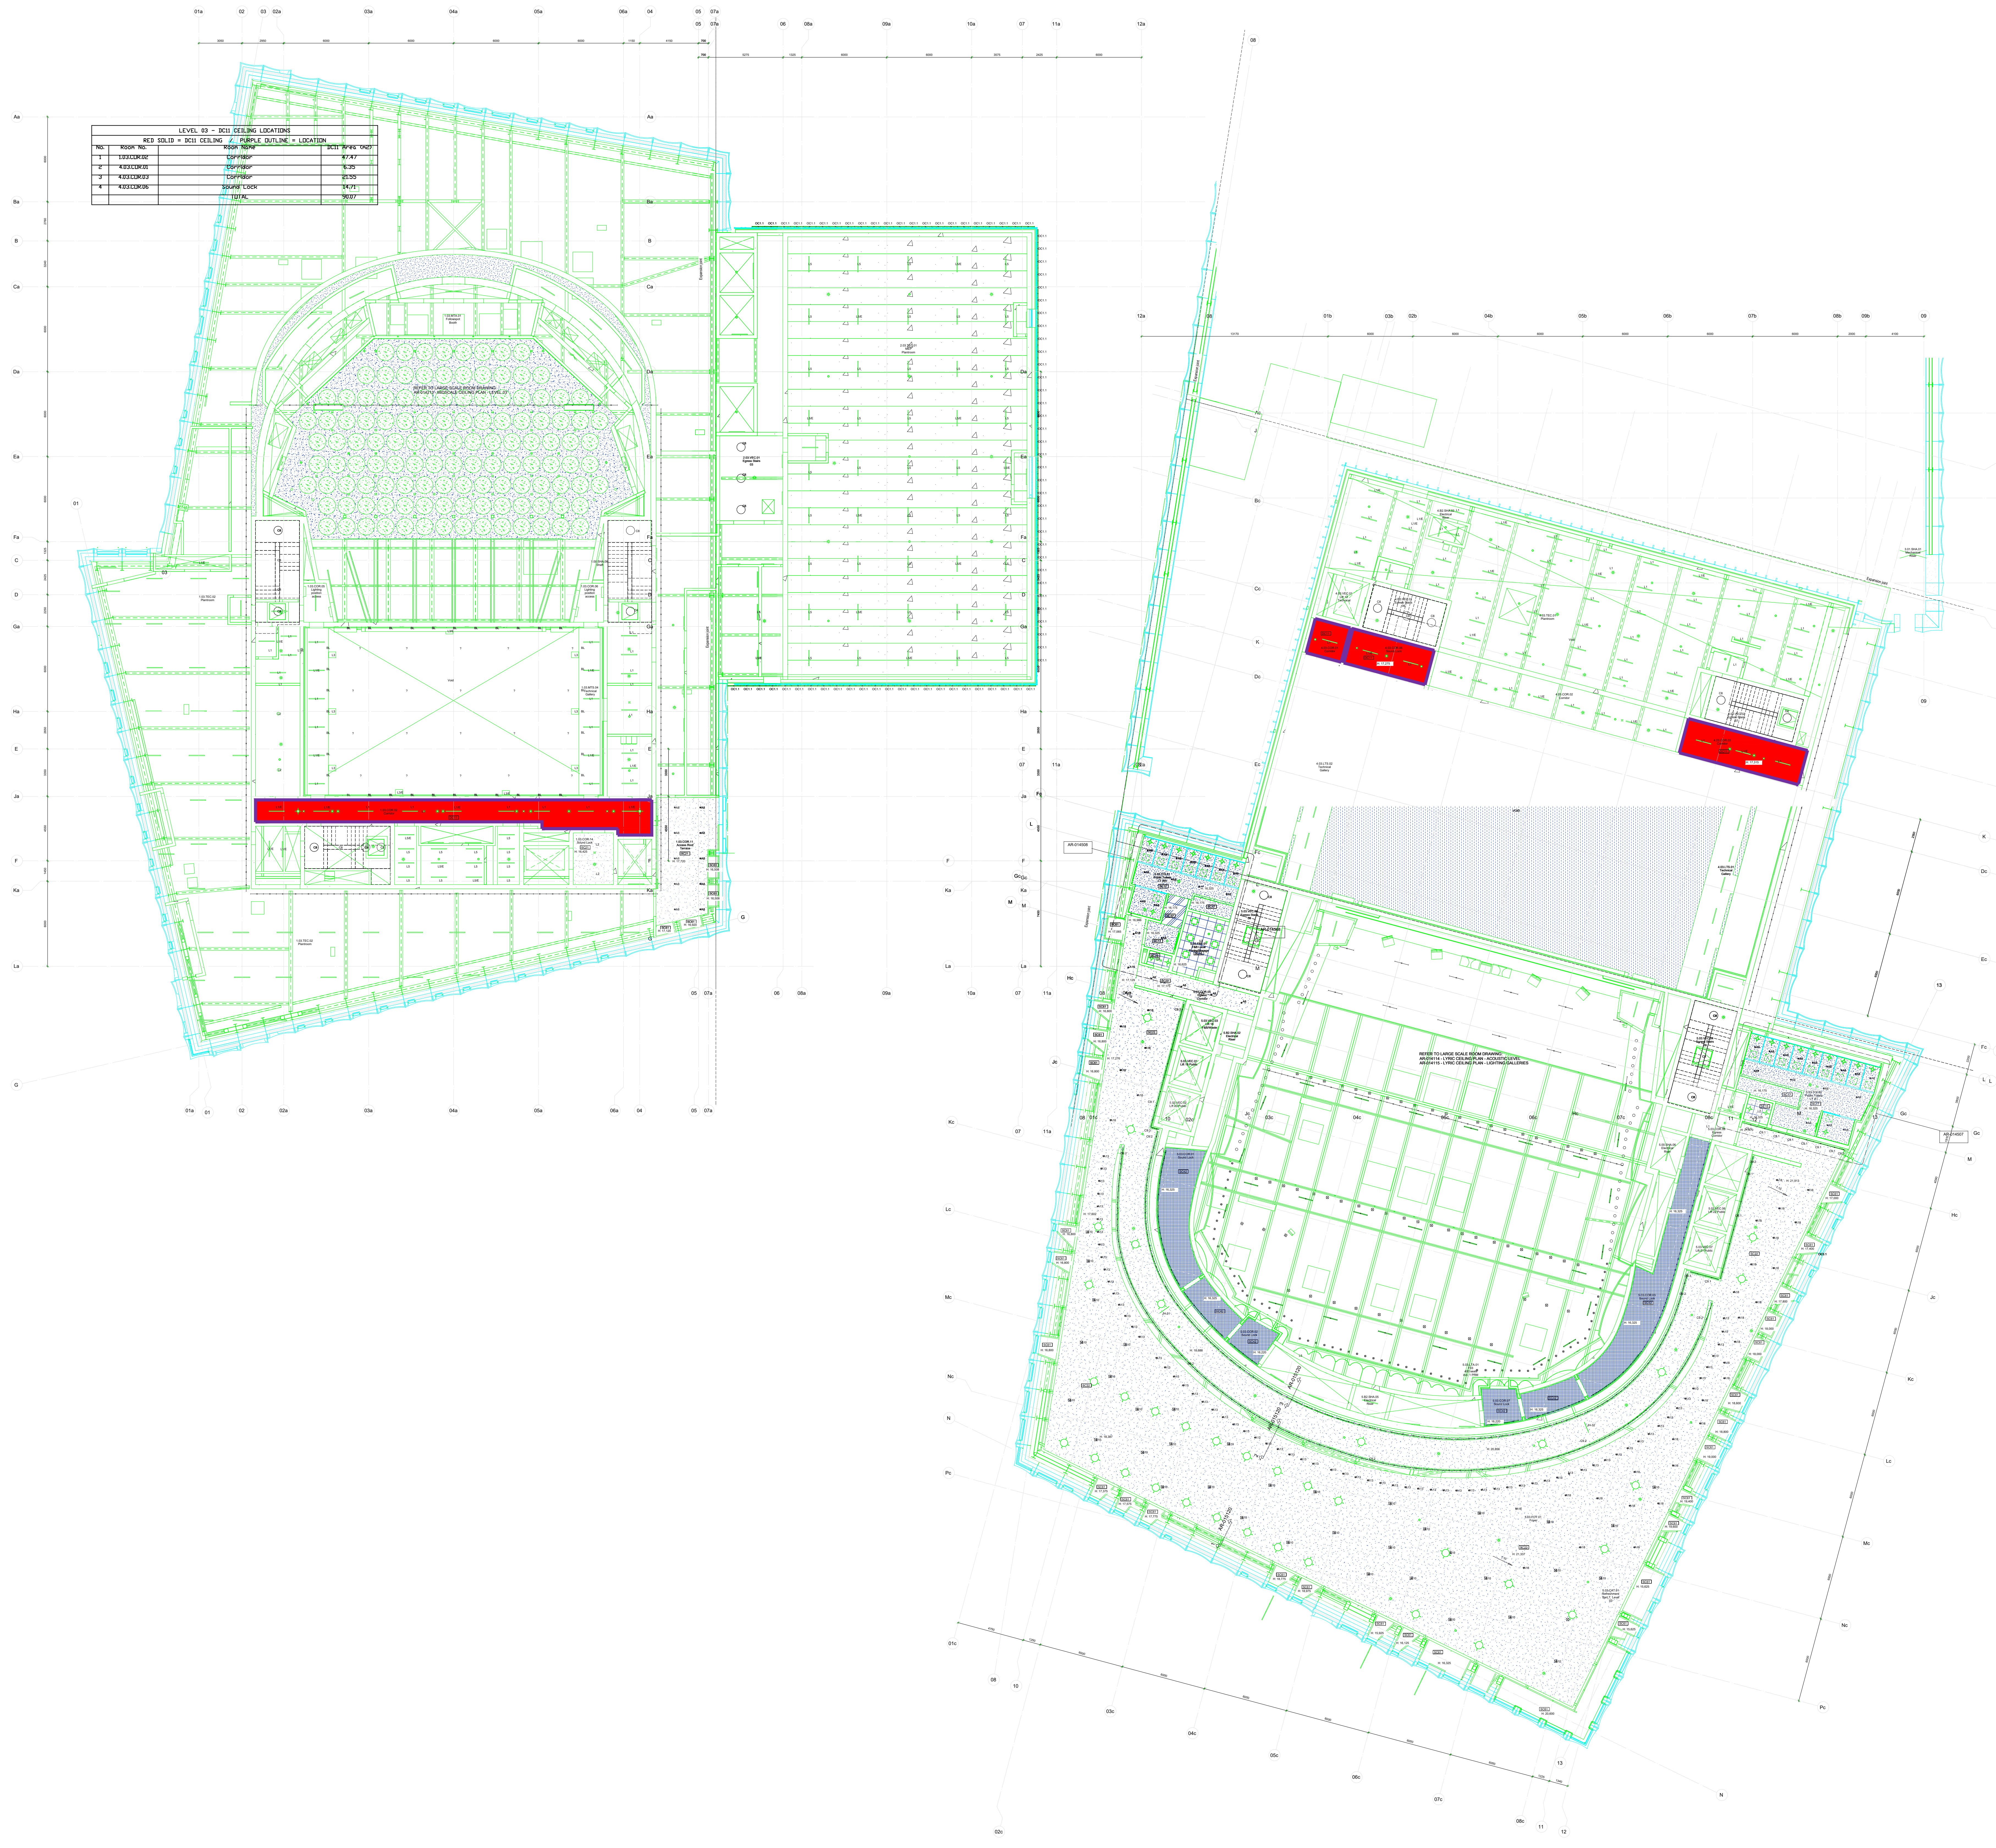

LEVEL 03 - DC11 CEILING LOCATIONS			
RED SOLID = DC11 CEILING / PURPLE OUTLINE = LOCATION			
No.	Room No.	Room Name	DC11 Area (m2)
1	1.03.COR.02	Corridor	47.47
2	4.03.COR.01	Corridor	6.35
3	4.03.COR.03	Corridor	21.55
4	4.03.COR.06	Sound Lock	14.71
		TOTAL	90.07

CEILING SYMBOLS

H: X,XXX CEILING HEIGHT, PROJECT BASE POINT

SIGNAGE - HANGING JUNCTION

SPRINKLER

SMOKE DETECTOR

LIGHTING FIXTURES

⊠ Ceiling recessed (Type A1, A2)

⊗ Ceiling recessed (Type A3)

▪ Ceiling recessed (Type A4, A7)

▭ Ceiling recessed (Type A5, A6, A19)

CEILING SYMBOLS

H: X,XXX CEILING HEIGHT, PROJECT BASE POINT

SIGNAGE - HANGING JUNCTION

SPRINKLER

SMOKE DETECTOR

LIGHTING FIXTURES

⊠ Ceiling recessed (Type A1, A2)

⊗ Ceiling recessed (Type A3)

▪ Ceiling recessed (Type A4, A7)

▭ Ceiling recessed (Type A5, A6, A19)