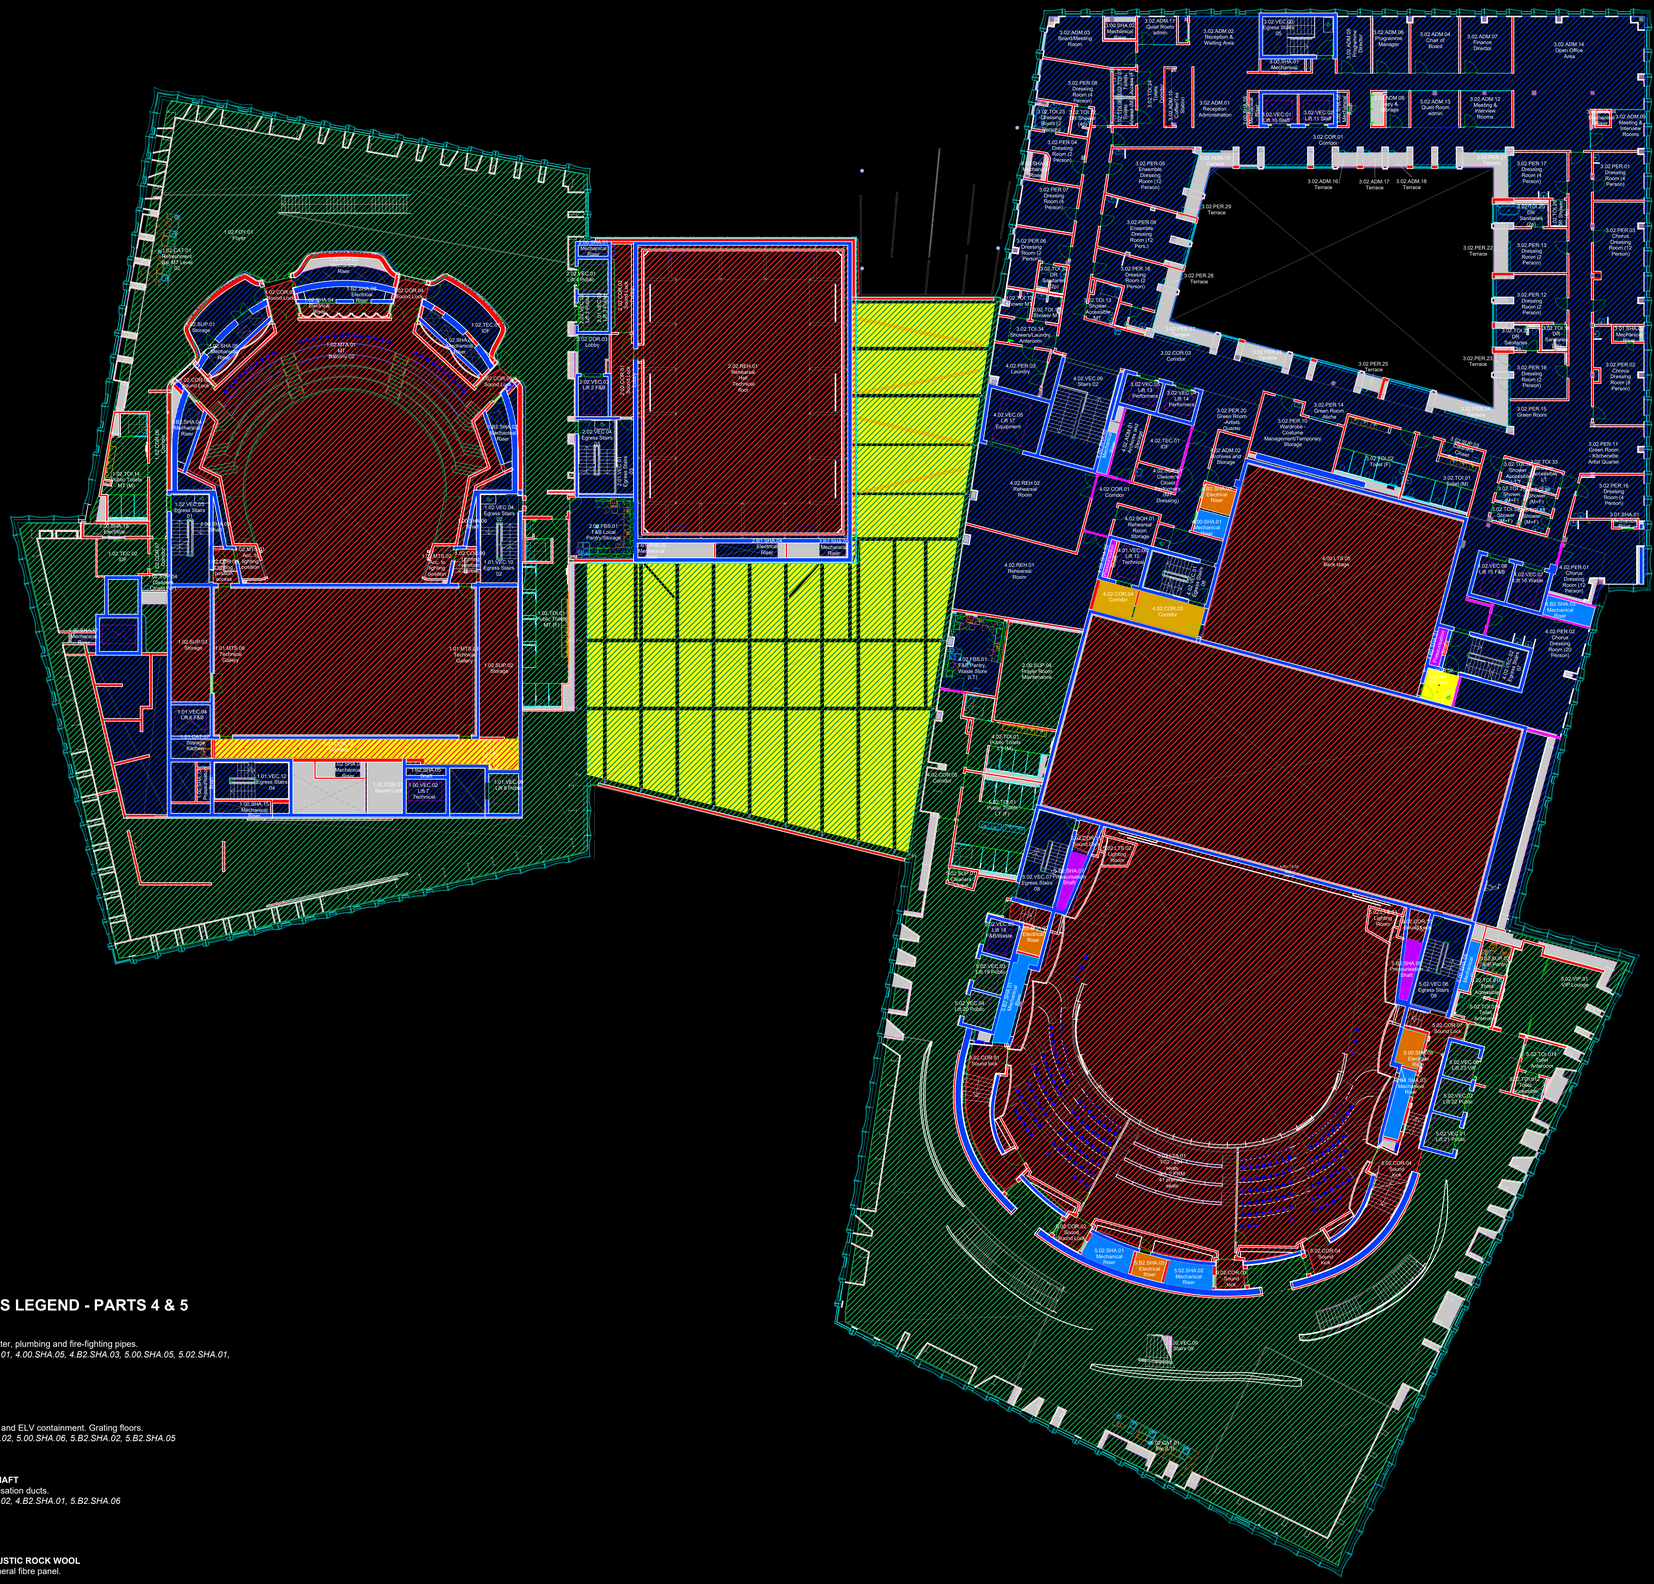


SHAFTS & RISERS LEGEND - PARTS 4 & 5

MECHANICAL RISER
HVAC ducts, chilled water, plumbing and fire-fighting pipes.
On this plan: 4.00.SHA.01, 4.00.SHA.05, 4.B2.SHA.03, 5.00.SHA.05, 5.02.SHA.01,

ELECTRICAL RISER
LV trays, busbars, DBs and ELV containment. Grating floors.
On this plan: 4.B2.SHA.02, 5.00.SHA.06, 5.B2.SHA.02, 5.B2.SHA.05

PRESSURISATION SHAFT
Stair / lift lobby pressurisation ducts.
On this plan: 4.00.SHA.02, 4.B2.SHA.01, 5.B2.SHA.06

DC11 CEILING - ACOUSTIC ROCK WOOL
Acoustic rock wool, mineral fibre panel.

JOH-HLA-S4-01-056-XXX-02-DR-AR-011120