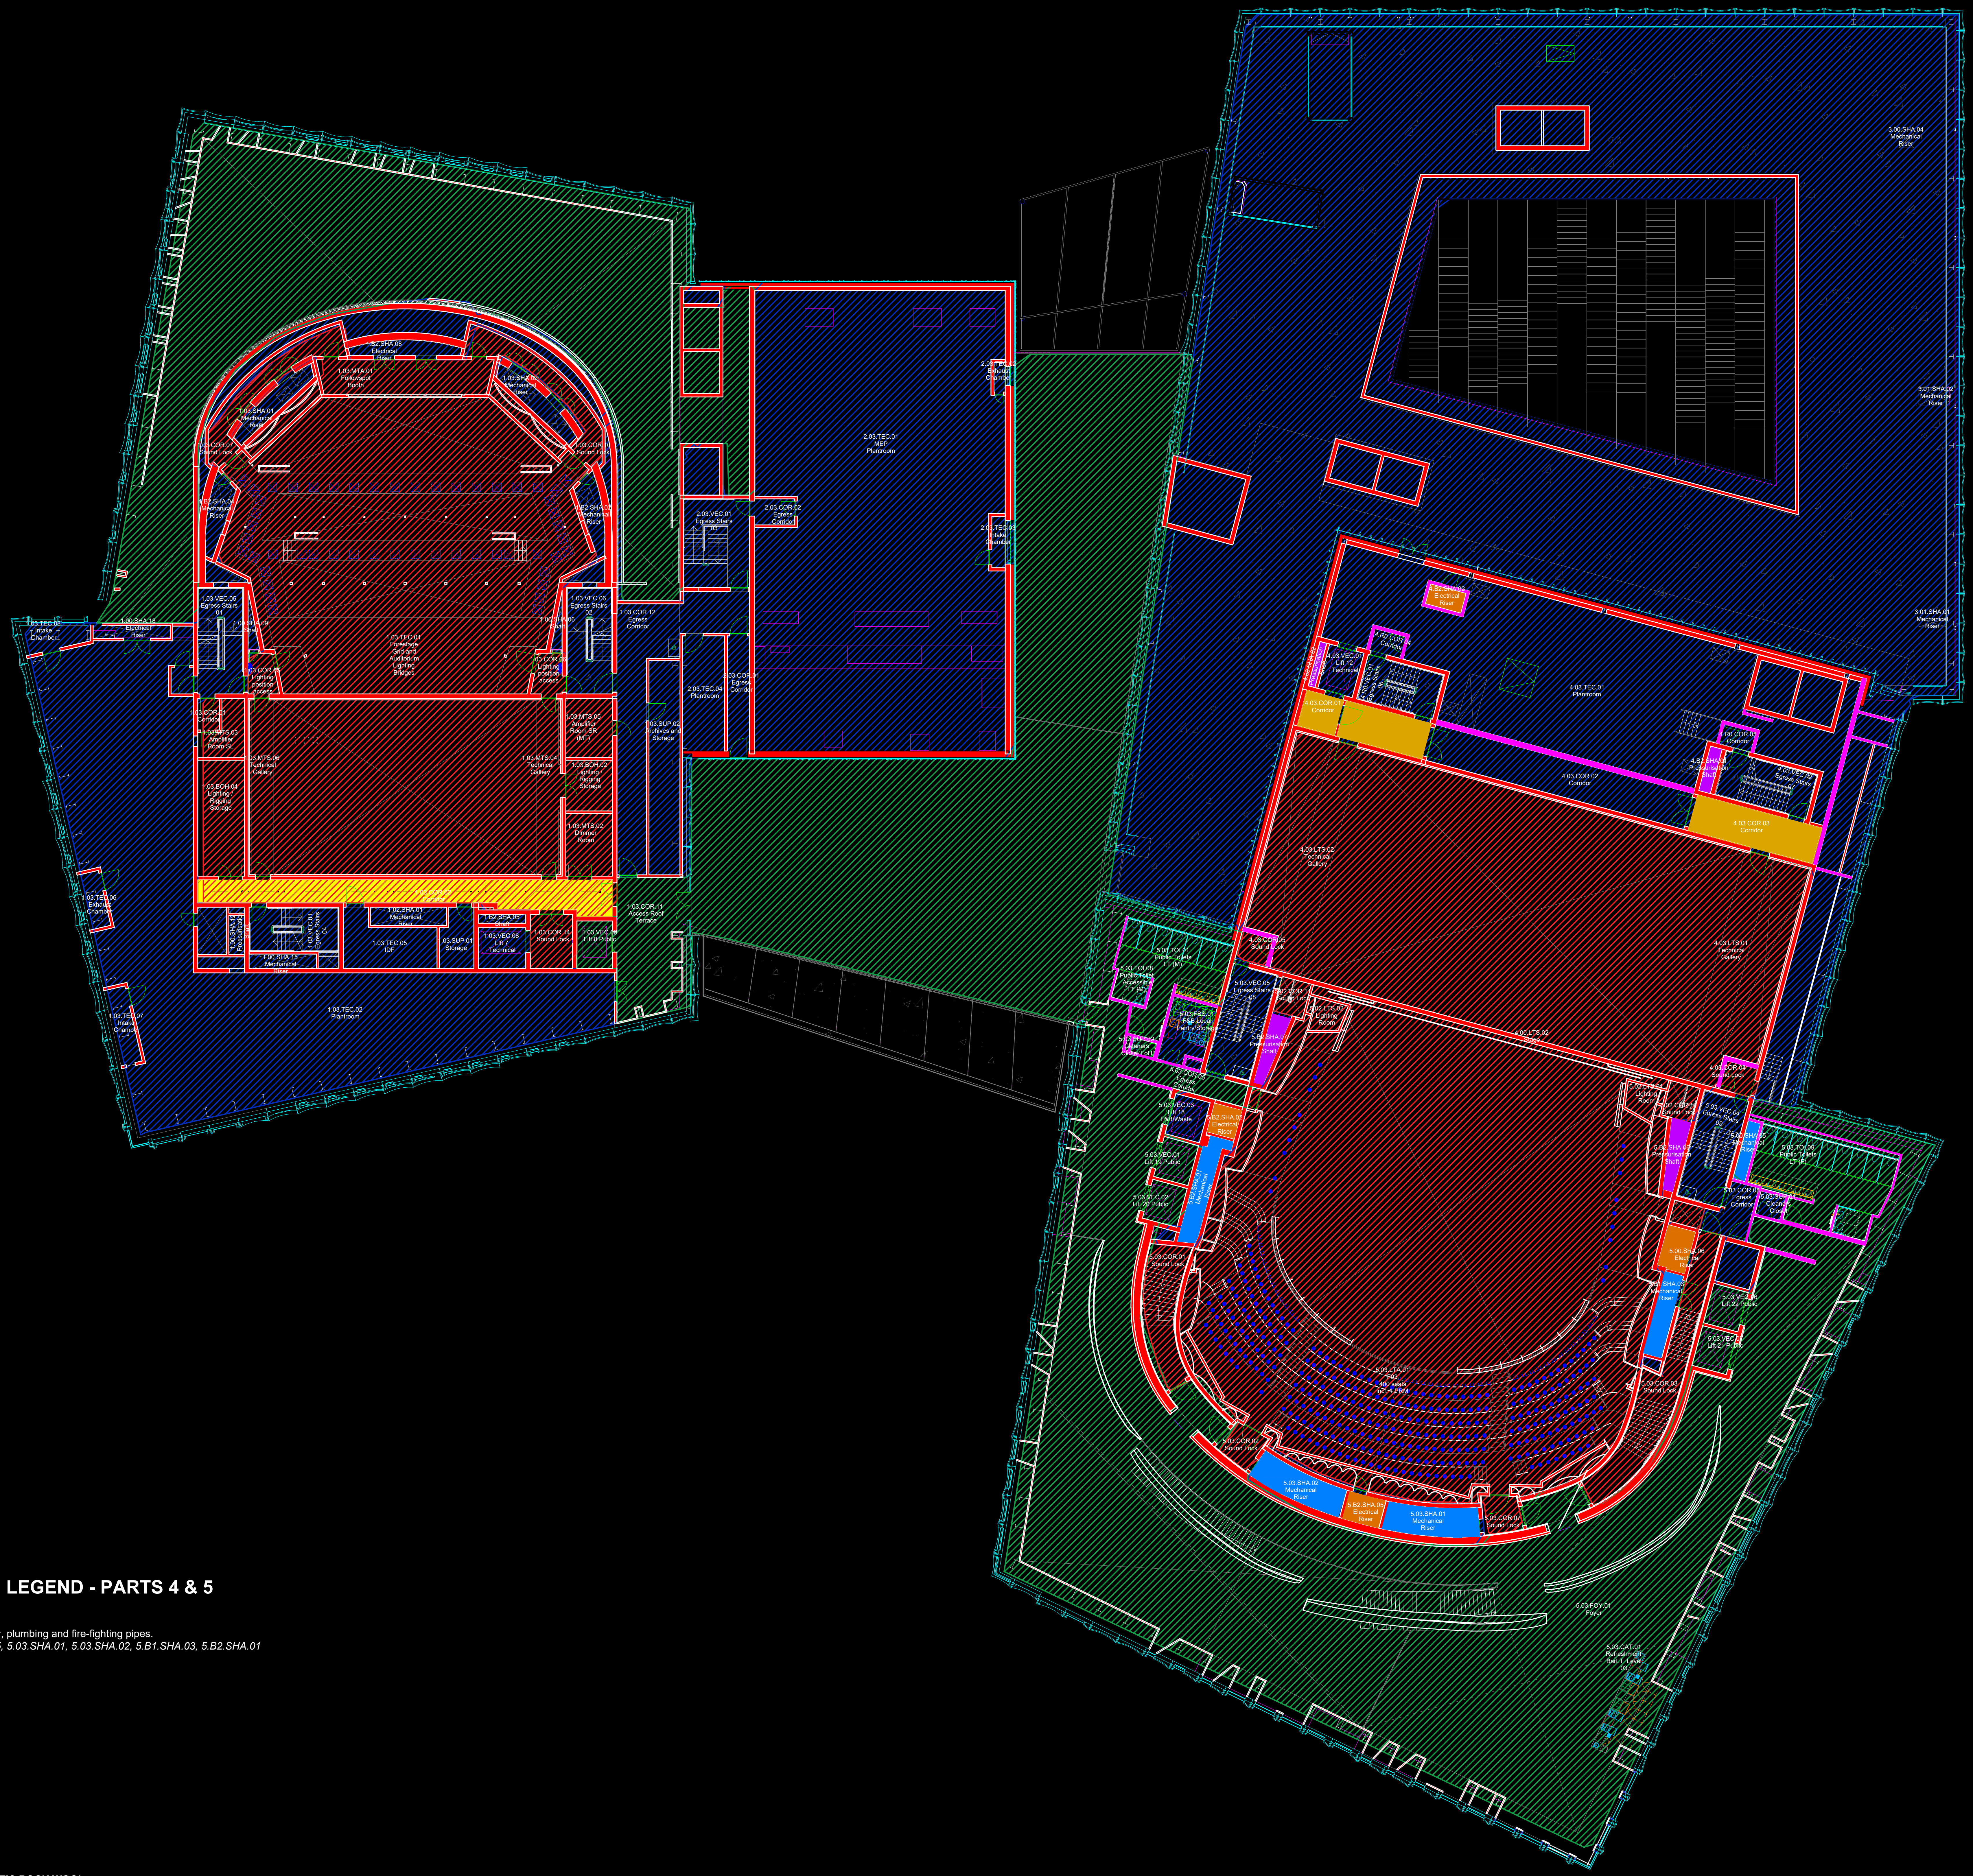
1.B2.SHA.08 Electrical Riser
1.03.MTA.01 Followspot Booth
1.03.SHA.01 Mechanical Riser
1.03.SHA.02 Mechanical Riser
1.03.COR.07 Sound Lock
1.03.COR.10 Sound Lock
1.B2.SHA.04 Mechanical Riser
1.B2.SHA.02 Mechanical Riser
1.03.VEC.05 Egress Stairs 01
1.03.VEC.06 Egress Stairs 02
1.00.SHA.09 Shaft
1.00.SHA.06 Shaft
1.03.TEC.08 Intake Chamber
1.00.SHA.18 Electrical Riser
1.03.TEC.01 Forestage Grid and Auditorium Lighting Bridges
1.03.COR.05 Lighting position access
1.03.COR.06 Lighting position access
1.03.COR.12 Egress Corridor
1.03.COR.01 Corridor
1.03.MTS.03 Amplifier Room SL
1.03.MTS.05 Amplifier Room SR (MT)
1.03.MTS.06 Technical Gallery
1.03.MTS.04 Technical Gallery
1.03.BOH.04 Lighting / Rigging Storage
1.03.BOH.02 Lighting / Rigging Storage
1.03.MTS.02 Dimmer Room
1.03.SUP.02 Archives and Storage
1.03.COR.03 Corridor
1.03.COR.11 Access Roof Terrace
1.00.SHA.12 Pressurisation Shaft
1.03.VEC.01 Egress Stairs 04
1.00.SHA.15 Mechanical Riser
1.02.SHA.01 Mechanical Riser
1.03.TEC.05 IDF
1.03.SUP.01 Storage
1.B2.SHA.05 Shaft
1.03.VEC.08 Lift 7 Technical
1.03.COR.14 Sound Lock
1.03.VEC.09 Lift 8 Public
1.03.TEC.06 Exhaust Chamber
1.03.TEC.07 Intake Chamber
1.03.TEC.02 Plantroom
2.03.TEC.01 MEP Plantroom
2.03.TEC.02 Exhaust Chamber
2.03.TEC.03 Intake Chamber
2.03.VEC.01 Egress Stairs 03
2.03.COR.02 Egress Corridor
2.03.TEC.04 Plantroom
2.03.COR.01 Egress Corridor
3.00.SHA.04 Mechanical Riser
3.01.SHA.02 Mechanical Riser
3.01.SHA.01 Mechanical Riser
4.B2.SHA.02 Electrical Riser
4.R0.COR.04 Corridor
4.00.SHA.02 Pressurisation Shaft
4.03.VEC.01 Lift 12 Technical
4.R0.VEC.01 Egress Stairs 06
4.03.TEC.01 Plantroom
4.03.COR.01 Corridor
4.03.COR.02 Corridor
4.R0.COR.05 Corridor
4.B2.SHA.01 Pressurisation Shaft
4.03.VEC.02 Egress Stairs 07
4.03.COR.03 Corridor
4.03.LTS.02 Technical Gallery
4.03.LTS.01 Technical Gallery
4.00.LTS.02 Stage
4.03.COR.05 Sound Lock
4.03.COR.04 Sound Lock
5.03.TOI.01 Public Toilets LT (M)
5.03.TOI.08 Public Toilet Accessible LT (M)
5.03.FBS.01 F&B Local Pantry/Storage
5.03.SUP.02 Cleaners Closet FoH
5.03.VEC.05 Egress Stairs 08
5.02.COR.1 Sound Lock
5.02.LTS.02 Lighting Room
5.B2.SHA.07 Pressurisation Shaft
5.03.COR.05 Egress Corridor
5.03.VEC.03 Lift 18 F&B/Waste
5.B2.SHA.02 Electrical Riser
5.03.VEC.01 Lift 19 Public
5.B2.SHA.01 Mechanical Riser
5.03.VEC.02 Lift 20 Public
5.03.COR.01 Sound Lock
5.02.LTS.01 Lighting Room
5.02.COR.10 Sound Lock
5.03.VEC.04 Egress Stairs 09
5.B2.SHA.06 Pressurisation Shaft
5.00.SHA.05 Mechanical Riser
5.03.TOI.09 Public Toilets LT (F)
5.03.COR.08 Egress Corridor
5.03.SUP.01 Cleaners Closet
5.00.SHA.06 Electrical Riser
5.B1.SHA.03 Mechanical Riser
5.03.VEC.06 Lift 22 Public
5.03.VEC.07 Lift 21 Public
5.03.COR.03 Sound Lock
5.03.LTA.01 F03 400 seats incl. 1 PRM
5.03.COR.02 Sound Lock
5.03.SHA.02 Mechanical Riser
5.B2.SHA.05 Electrical Riser
5.03.SHA.01 Mechanical Riser
5.03.COR.07 Sound Lock
5.03.FOY.01 Foyer
5.03.CAT.01 Refreshment BarLT Level 03

SHAFTS & RISERS LEGEND - PARTS 4 & 5

🟦 **MECHANICAL RISER**
HVAC ducts, chilled water, plumbing and fire-fighting pipes.
On this plan: 5.00.SHA.05, 5.03.SHA.01, 5.03.SHA.02, 5.B1.SHA.03, 5.B2.SHA.01

🟧

🟪

🟨 **DC11 CEILING - ACOUSTIC ROCK WOOL**
Acoustic rock wool, mineral fibre panel.

JOH-HLA-S4-01-056-XXX-03-DR-AR-011130