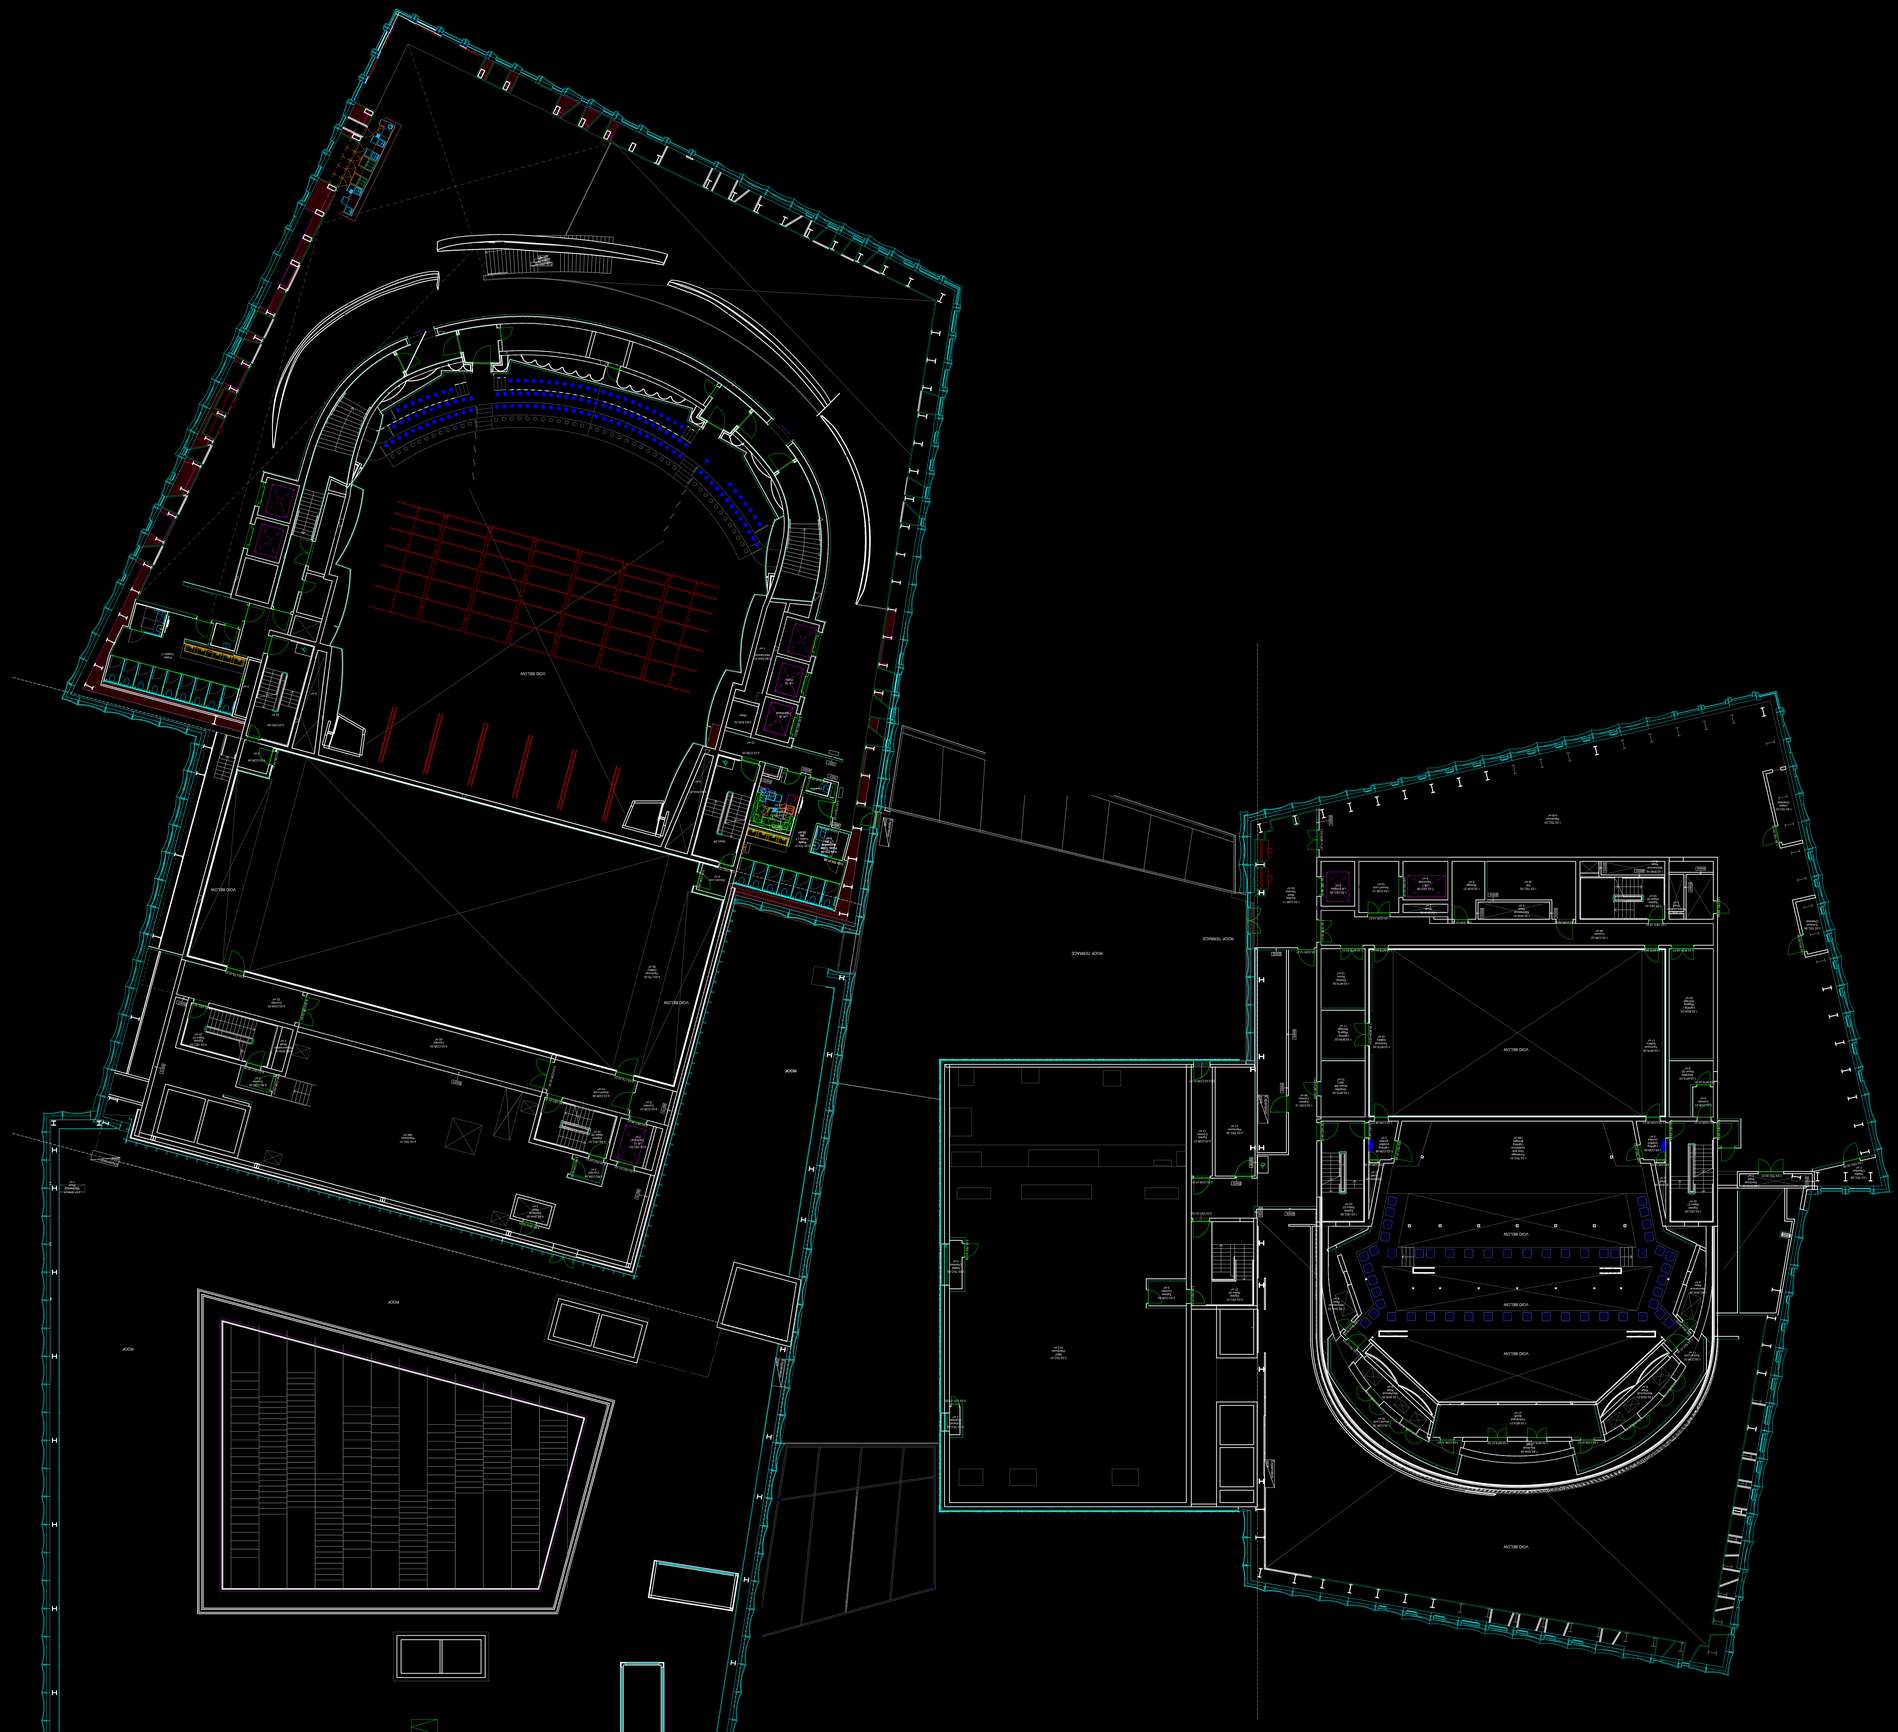

VOID BELOW
ROOF
ROOF TERRACE