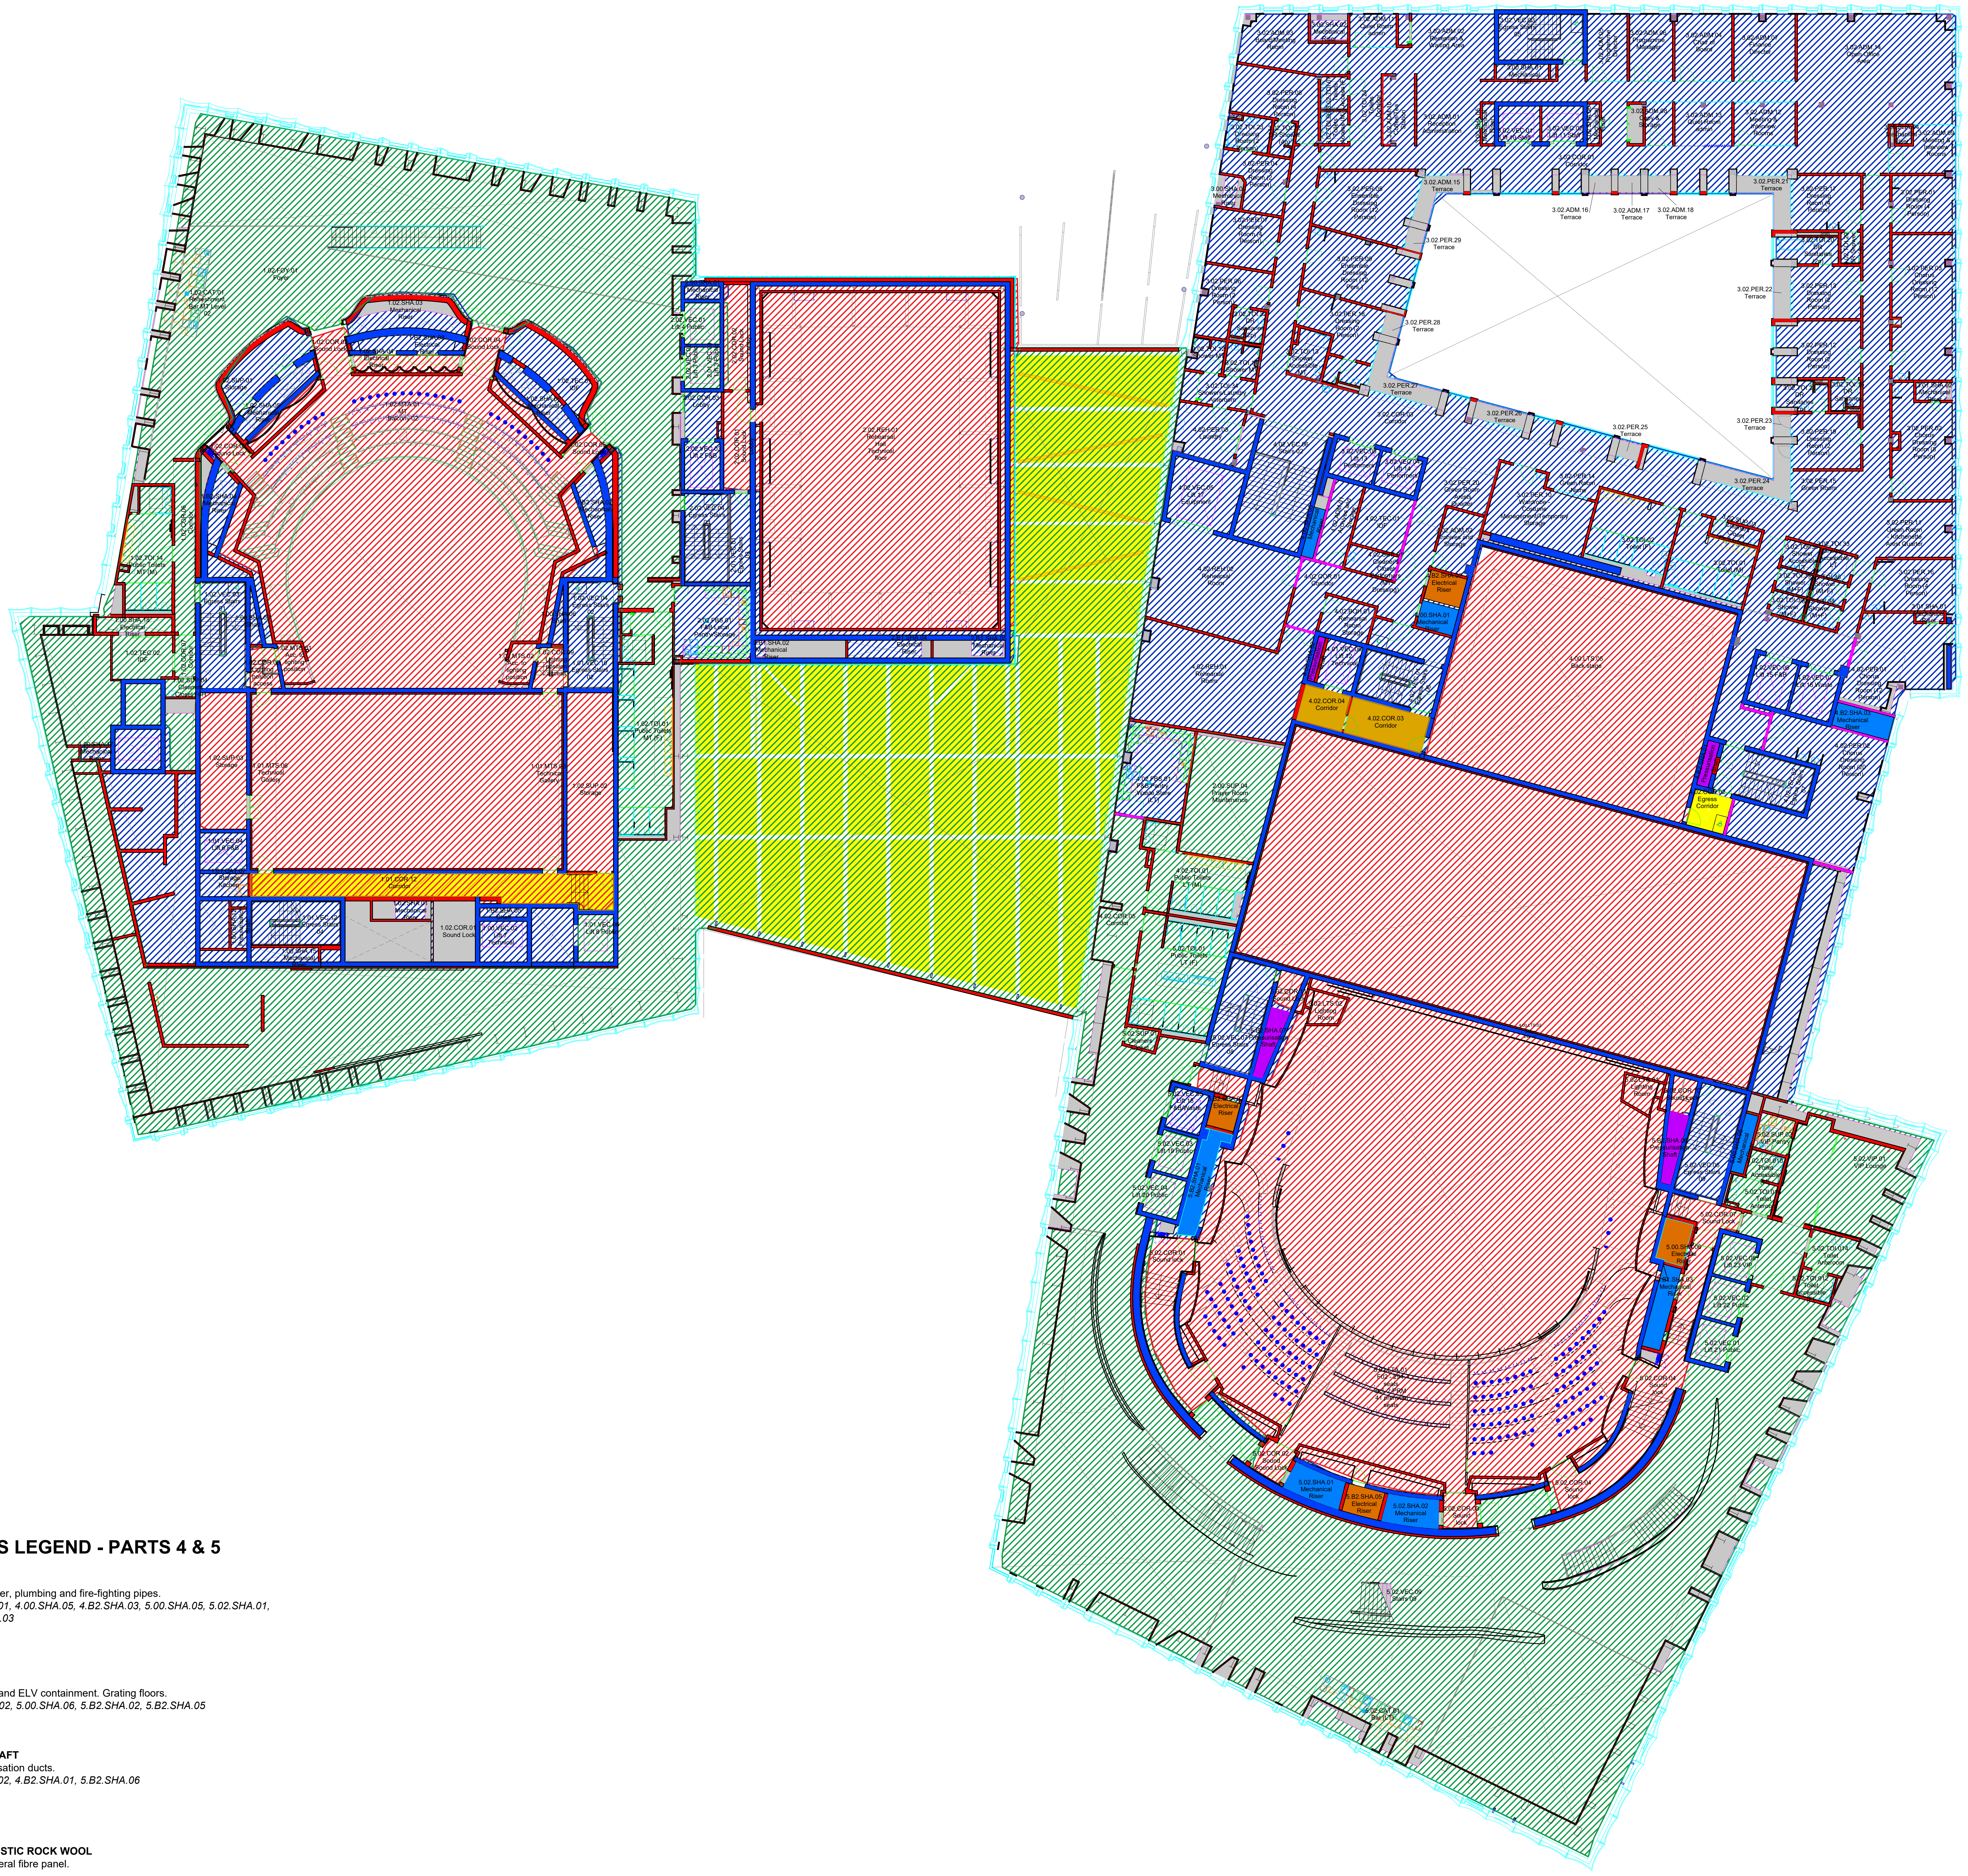
3.00.SHA.01 Mechanical Riser
3.02.ADM.01 Reception Administration
3.02.VEC.01 Lift 10 Staff
3.02.VEC.02 Lift 11 Staff
3.02.ADM.08 Copy & Storage
3.02.ADM.13 Quiet Room admin
3.02.ADM.12 Meeting & Interview Rooms
3.02.COR.01 Corridor
3.02.ADM.15 Terrace
3.02.ADM.16 Terrace
3.02.ADM.17 Terrace
3.02.ADM.18 Terrace
3.02.PER.21 Terrace
3.02.PER.29 Terrace
3.02.PER.22 Terrace
3.02.PER.28 Terrace
3.02.PER.27 Terrace
3.02.PER.26 Terrace
3.02.PER.25 Terrace
3.02.PER.23 Terrace
3.02.PER.24 Terrace
3.02.PER.05 Ensemble Dressing Room (12 Person)
3.02.PER.09 Ensemble Dressing Room (12 Pers.)
3.02.PER.18 Dressing Room (2 Person)
3.02.PER.17 Dressing Room (4 Person)
3.02.PER.13 Dressing Room (2 Person)
3.02.PER.12 Dressing Room (2 Person)
3.02.PER.19 Dressing Room (2 Person)
3.02.PER.15 Green Room
3.02.PER.14 Green Room Niche
3.02.PER.20 Green Room Artists Quarter
3.02.PER.10 Wardrobe - Costume Management/Temporary Storage
3.02.COR.03 Corridor
3.02.VEC.03 Lift 13 Performers
3.02.VEC.04 Lift 14 Performers
4.02.TEC.01 IDF
4.02.ADM.02 Archives and Storage
4.B2.SHA.02 Electrical Riser
3.02.TOI.02 Toilet (F)
3.02.TOI.01 Toilet (M)
3.02.SUP.03 Cleaners Closet
4.02.COR.04 Corridor
4.02.COR.03 Corridor

SHAFTS & RISERS LEGEND - PARTS 4 & 5

🟦 **MECHANICAL RISER**
HVAC ducts, chilled water, plumbing and fire-fighting pipes.
On this plan: 4.00.SHA.01, 4.00.SHA.05, 4.B2.SHA.03, 5.00.SHA.05, 5.02.SHA.01, 5.02.SHA.02, 5.B1.SHA.03

🟧 **ELECTRICAL RISER**
LV trays, busbars, DBs and ELV containment. Grating floors.
On this plan: 4.B2.SHA.02, 5.00.SHA.06, 5.B2.SHA.02, 5.B2.SHA.05

🟪 **PRESSURISATION SHAFT**
Stair / lift lobby pressurisation ducts.
On this plan: 4.00.SHA.02, 4.B2.SHA.01, 5.B2.SHA.06

🟨 **DC11 CEILING - ACOUSTIC ROCK WOOL**
Acoustic rock wool, mineral fibre panel.

JOH-HLA-S4-01-056-XXX-02-DR-AR-011120