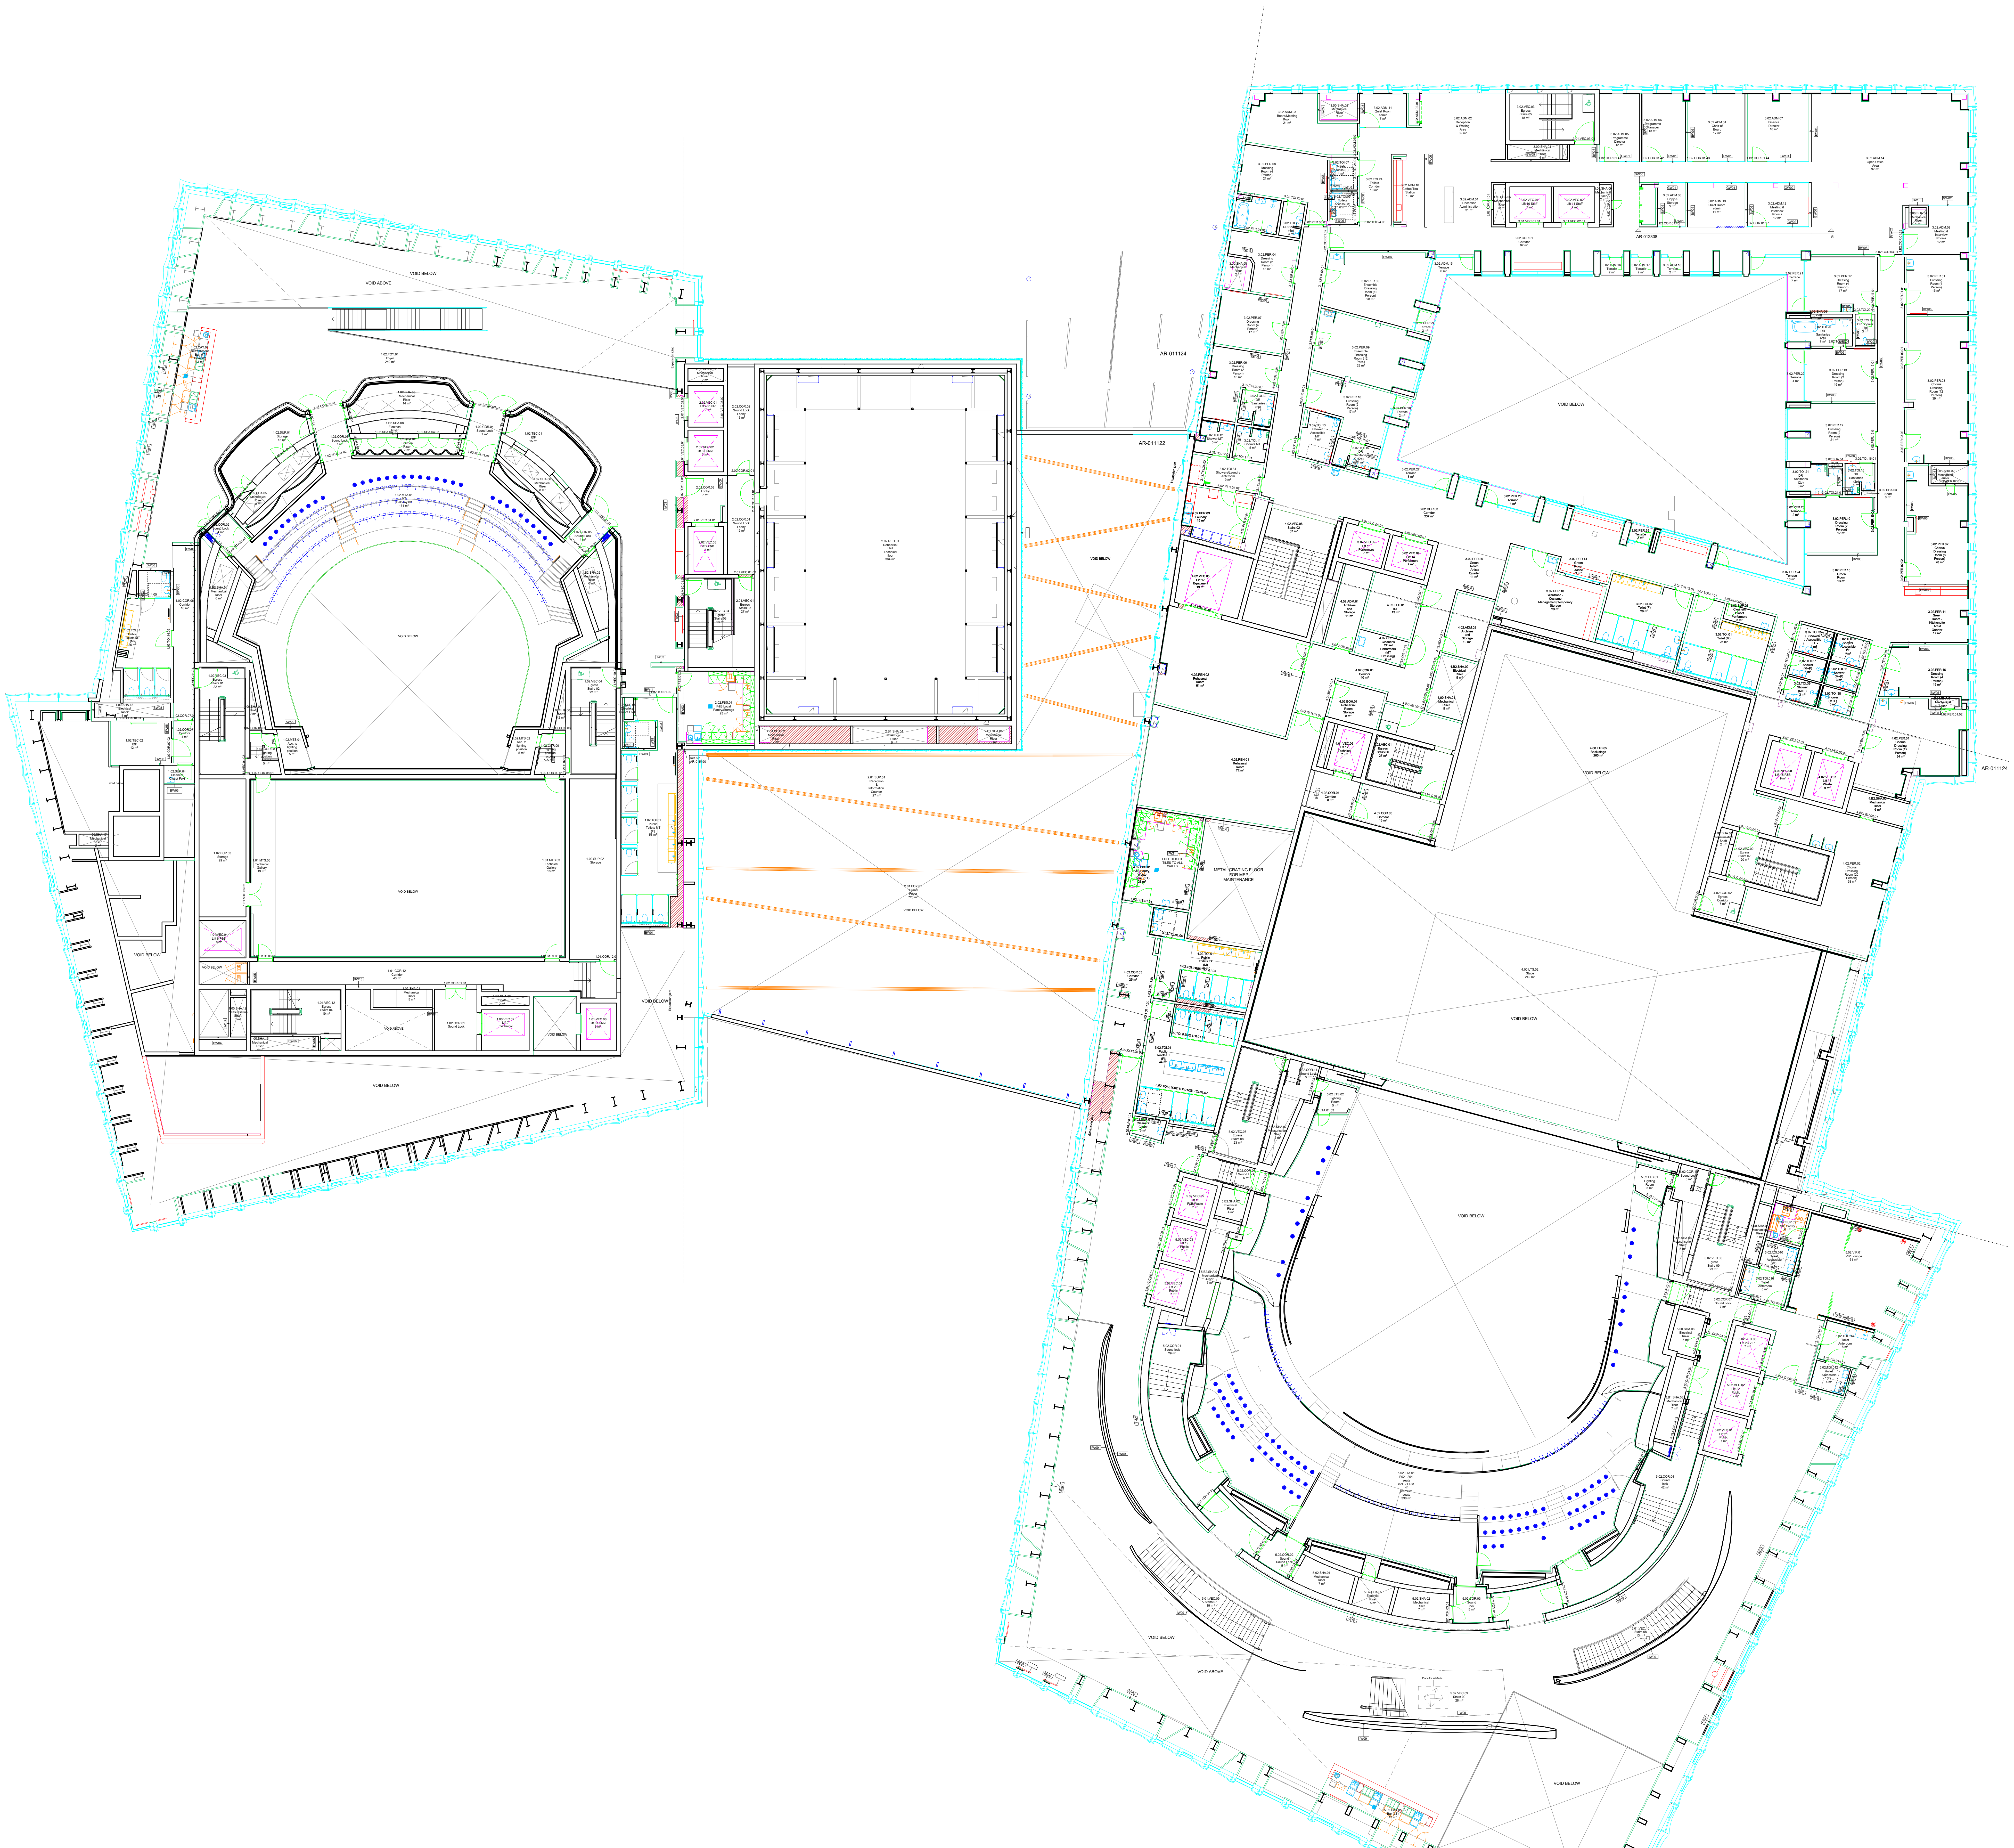
VOID ABOVE
VOID BELOW
AR-011124
AR-011122
AR-012308
3.00.SHA.09 Mechanical Riser 2 m²
3.02.PER.04 Dressing Room (2 Person) 13 m²
3.02.PER.05 Ensemble Dressing Room (12 Person) 28 m²
3.02.PER.07 Dressing Room (4 Person) 17 m²
3.02.PER.06 Dressing Room (2 Person) 16 m²
3.02.PER.09 Ensemble Dressing Room (12 Pers.) 28 m²
3.02.PER.18 Dressing Room (2 Person) 17 m²
3.02.TOI.32 DR Sanitaries (2p) 4 m²
3.02.TOI.12 Shower MT 5 m²
3.02.TOI.11 Shower MT 5 m²
3.02.TOI.13 Shower Accessible MT 7 m²
3.02.TOI.15 DR Sanitaries (2p) 4 m²
3.02.TOI.34 Showers/Laundry Anteroom 9 m²
4.02.PER.03 Laundry 15 m²
4.02.VEC.06 Stairs 02 37 m²
3.02.VEC.05 Lift 13 Performers 7 m²
Expansion joint
4.02.REH.01 Rehearsal Room 72 m²
4.02.COR.04 Corridor 8 m²
IW21
FULL HEIGHT TILES TO ALL WALLS
4.02.FBS.01 F&B Pantry, Waste Store (LT) 28 m²
METAL GRATING FLOOR FOR MEP MAINTENANCE
4.02.TOI.01 Public Toilets LT (M) 29 m²