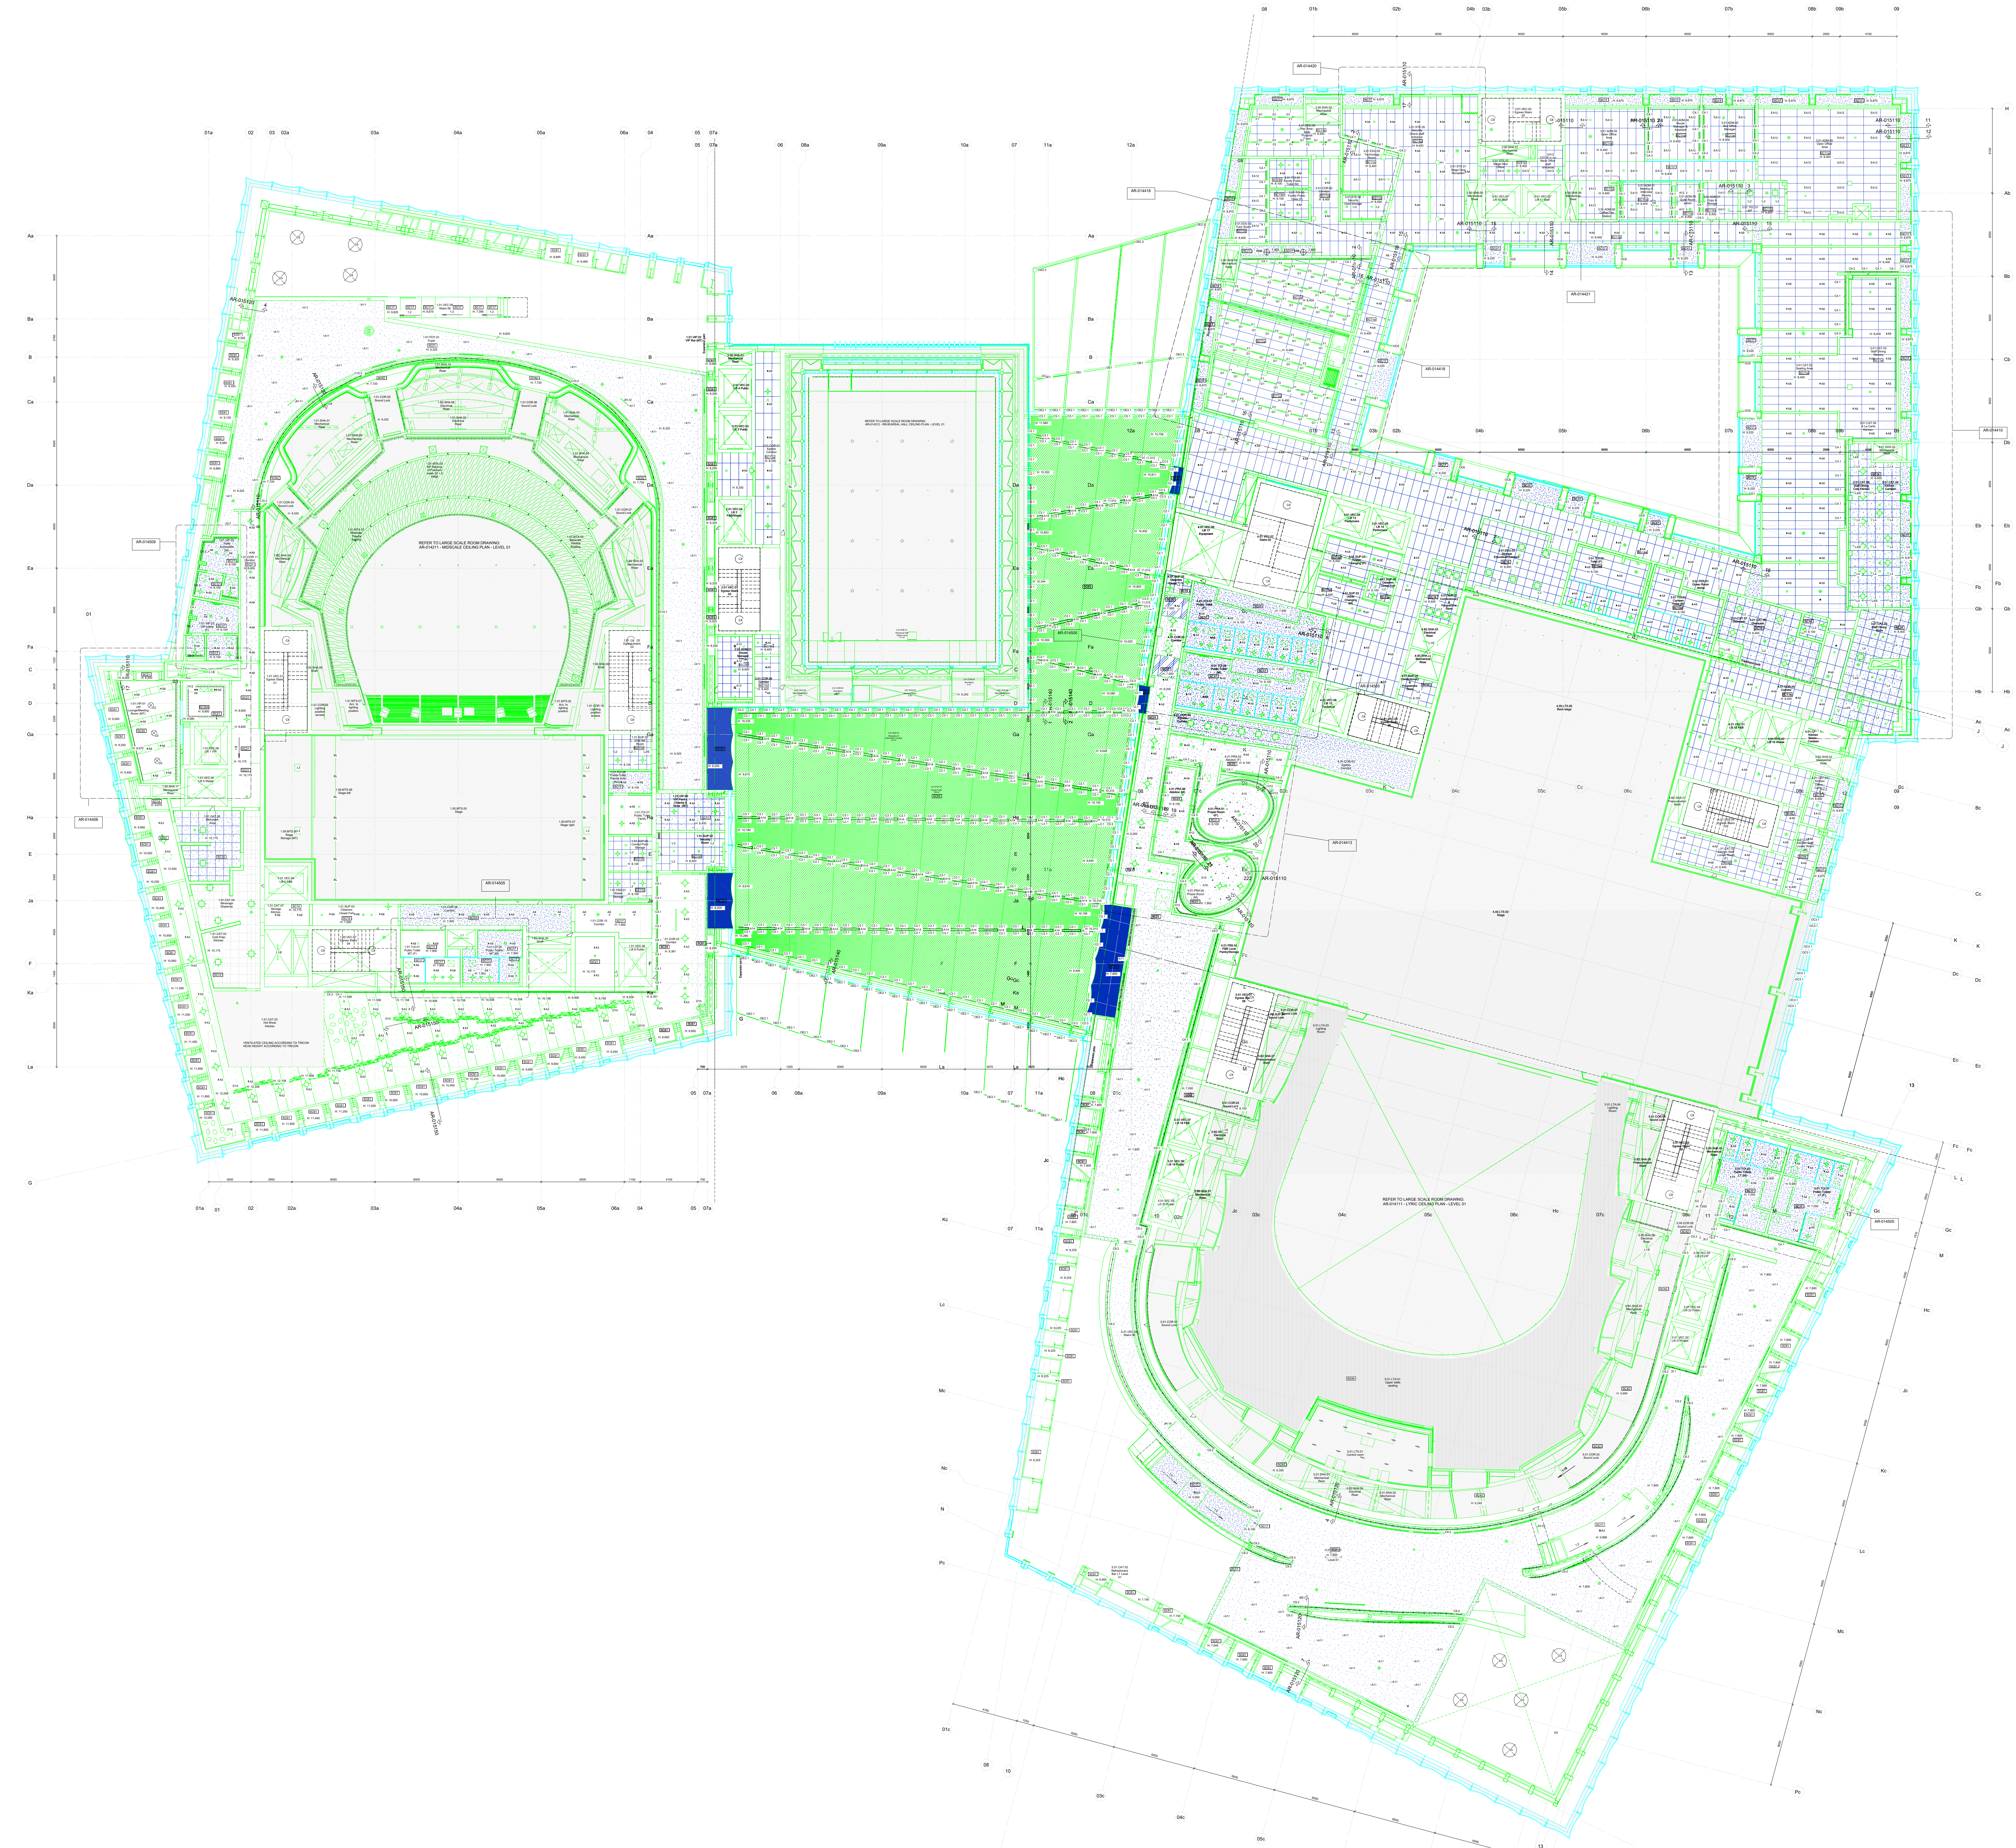

REFER TO LARGE SCALE ROOM DRAWING:
AR-014211 - MIDSCALE CEILING PLAN - LEVEL 01
1.01.MTA.03
MT Balcony
01Premium
seats 32 + 2
PRM
1.01.MTA.01
Midscale
Theatre
Seating
1.01.MTA.02
Midscale
Theatre
Seating
REFER TO LARGE SCALE ROOM DRAWING:
AR-014312 - REHEARSAL HALL CEILING PLAN - LEVEL 01
REFER TO LARGE SCALE ROOM DRAWING:
AR-014111 - LYRIC CEILING PLAN - LEVEL 01
1.01.CAT.02
Hot Show
Kitchen
VENTILATED CEILING ACCORDING TO TRICON
HEAD HEIGHT ACCORDING TO TRICON
1.01.CAT.03
Cold Prep
Kitchen
1.00.VEC.07
Egress Stairs
04