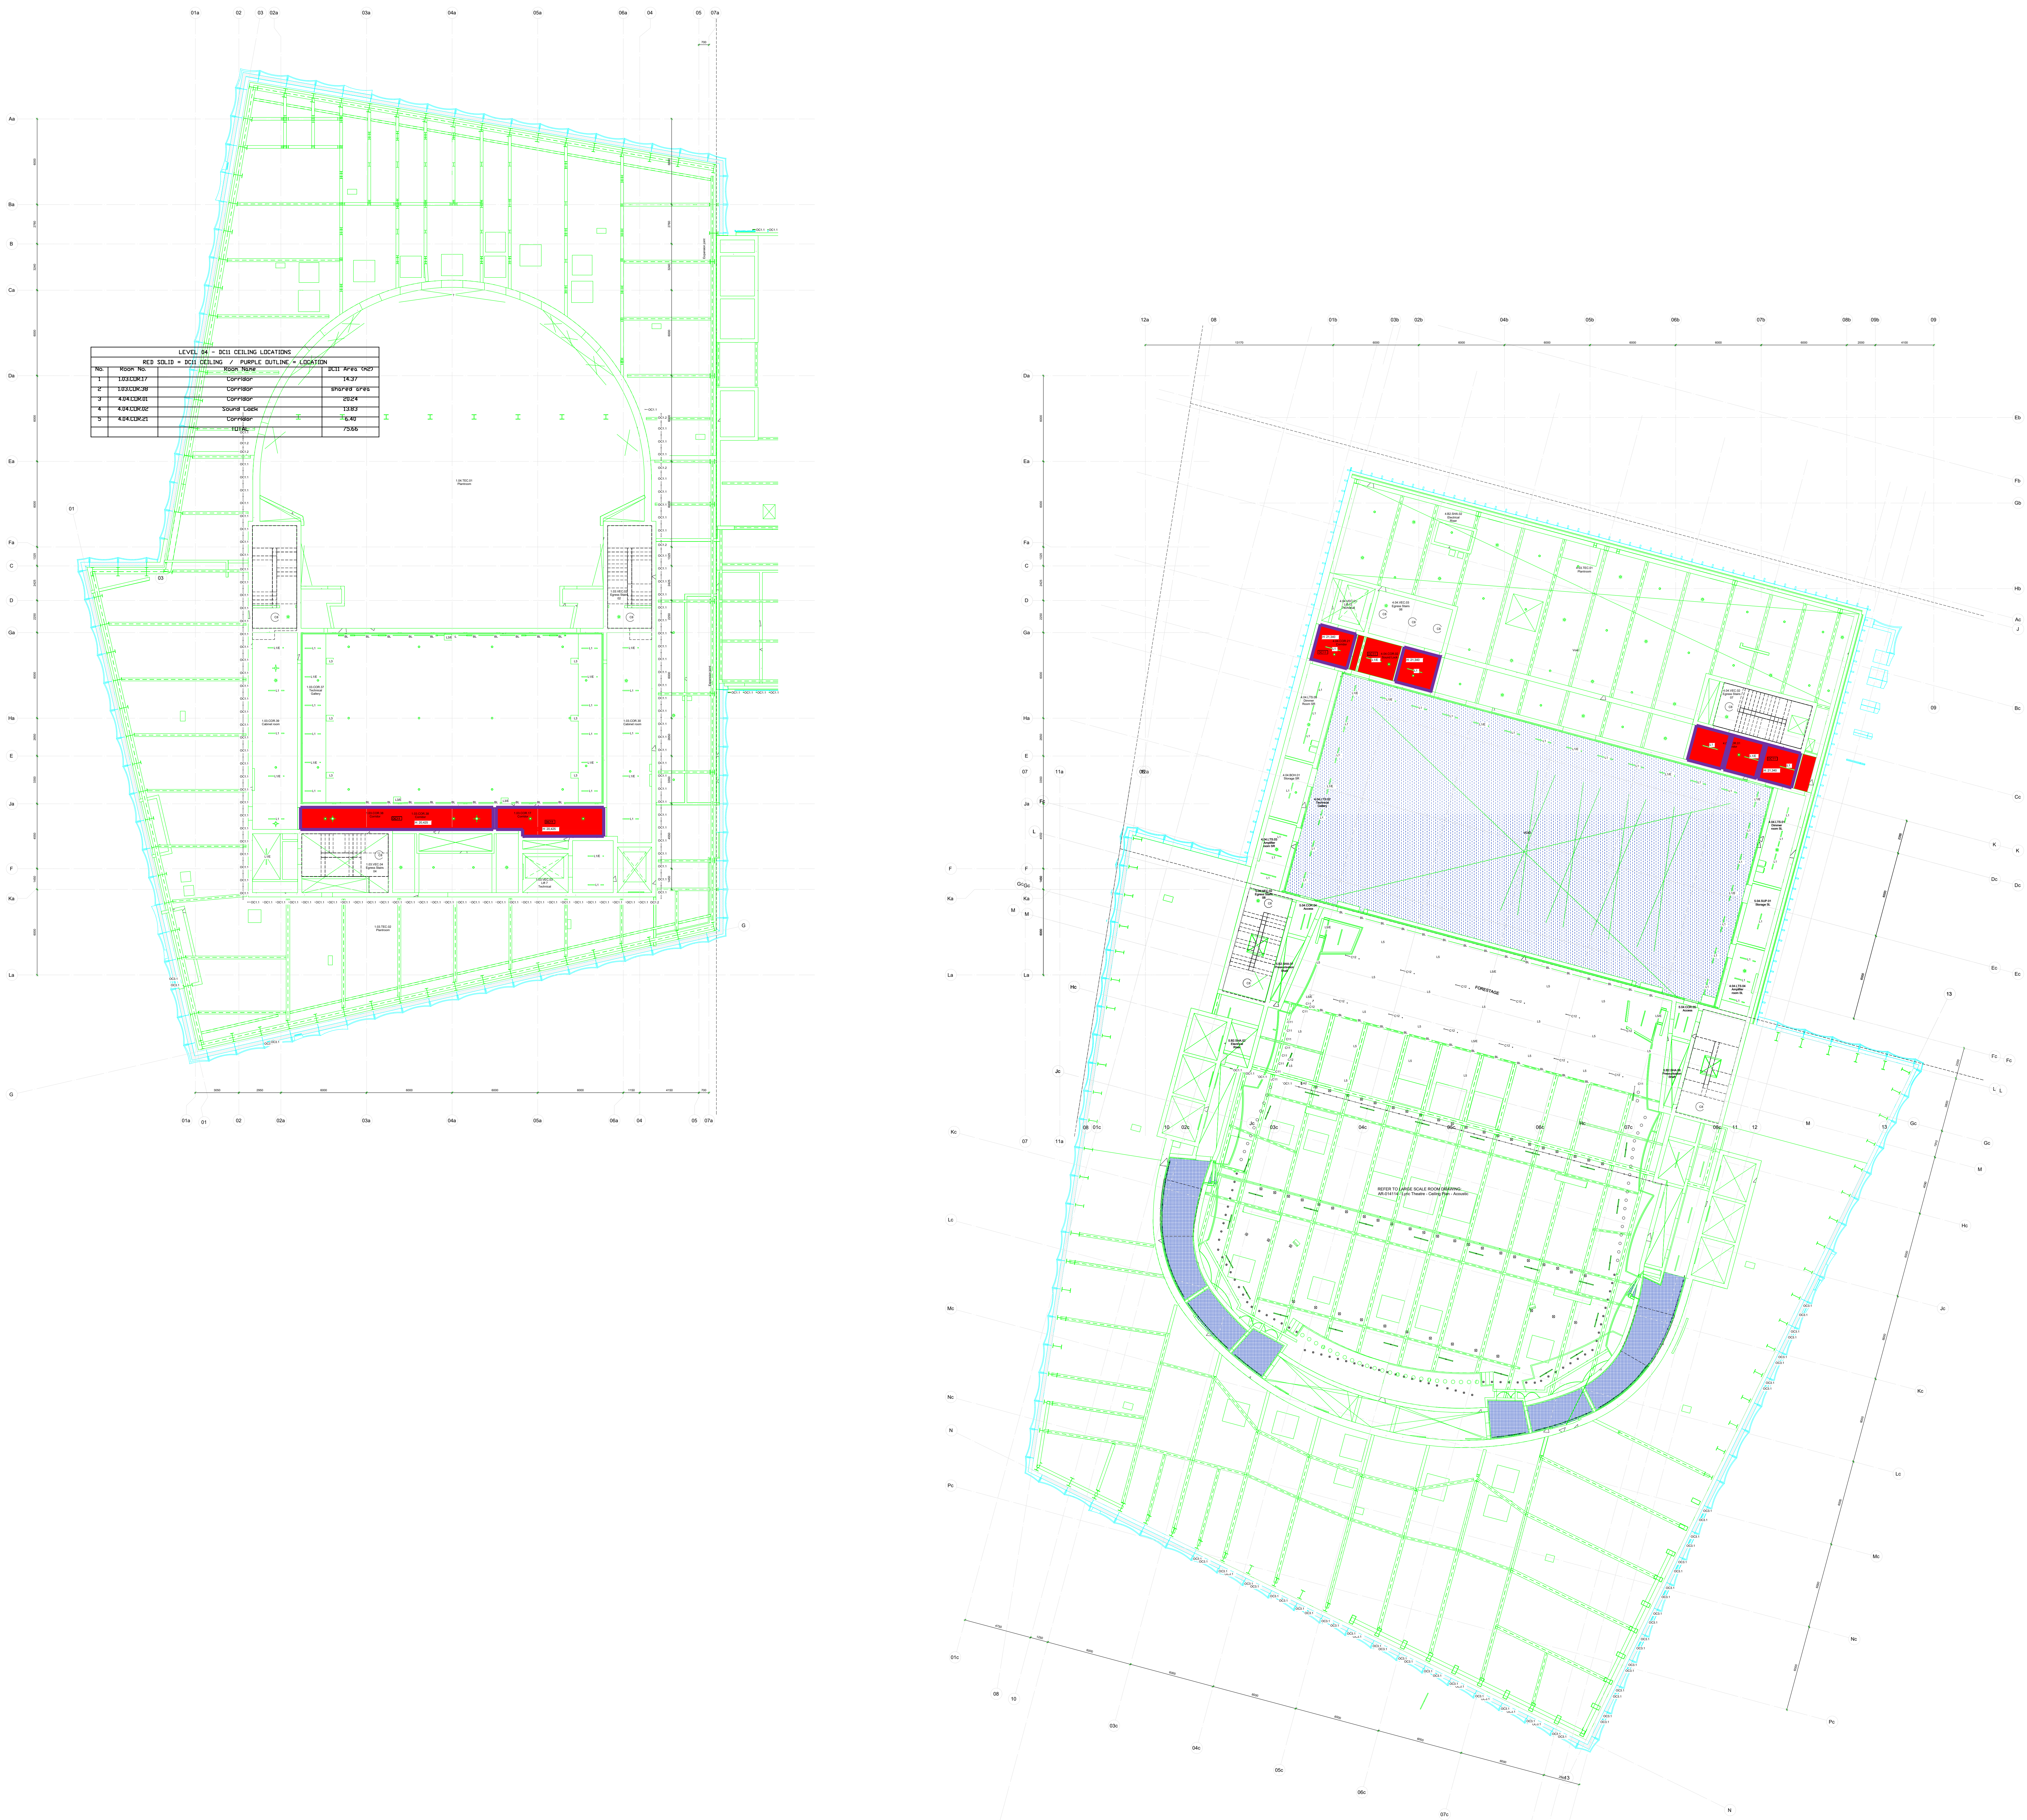

REFER TO LARGE SCALE ROOM DRAWING:
AR-014114 - Lyric Theatre - Ceiling Plan - Acoustic
FORESTAGE

LEVEL 04 - DC11 CEILING LOCATIONS

RED SOLID = DC11 CEILING / PURPLE OUTLINE = LOCATION

No.	Room No.	Room Name	DC11 Area (m2)
1	1.03.COR.17	Corridor	14.37
2	1.03.COR.38	Corridor	shared area
3	4.04.COR.01	Corridor	20.24
4	4.04.COR.02	Sound Lock	13.83
5	4.04.COR.21	Corridor	6.40
		TOTAL	75.66