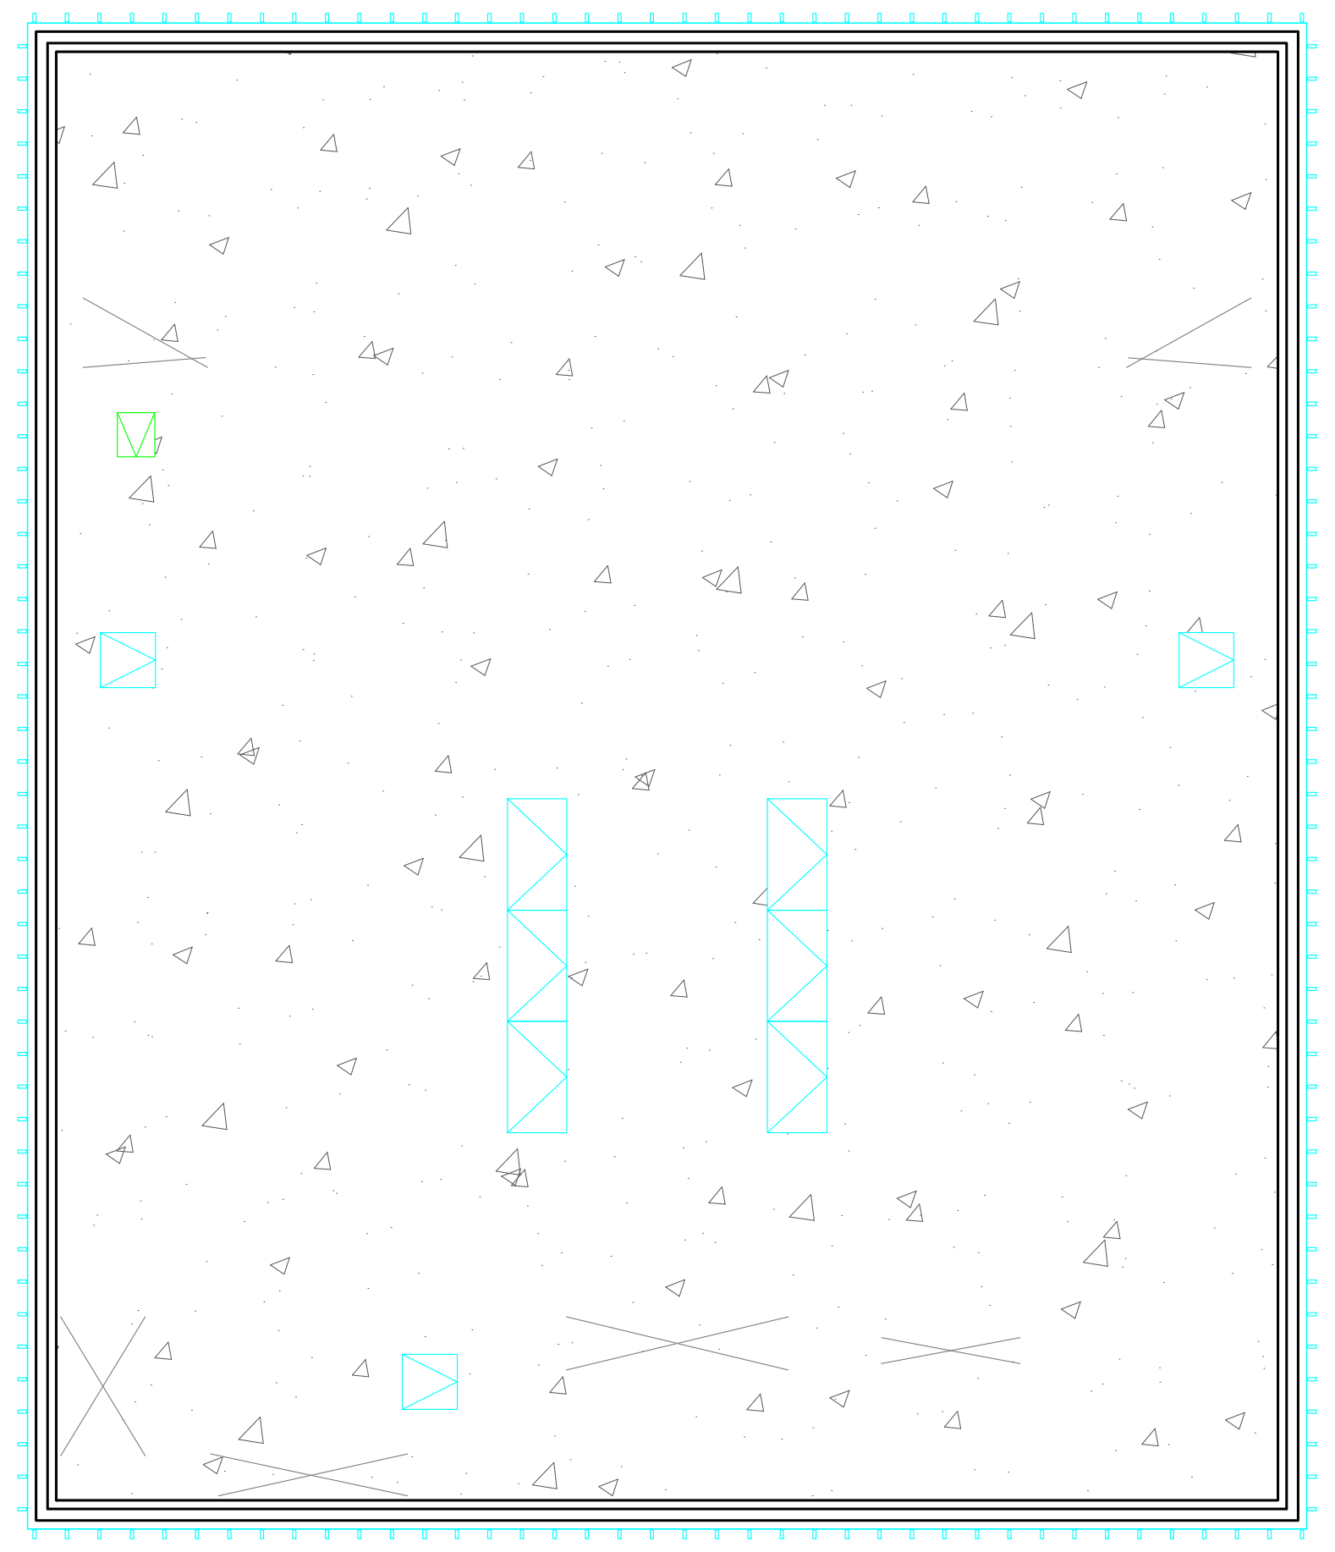

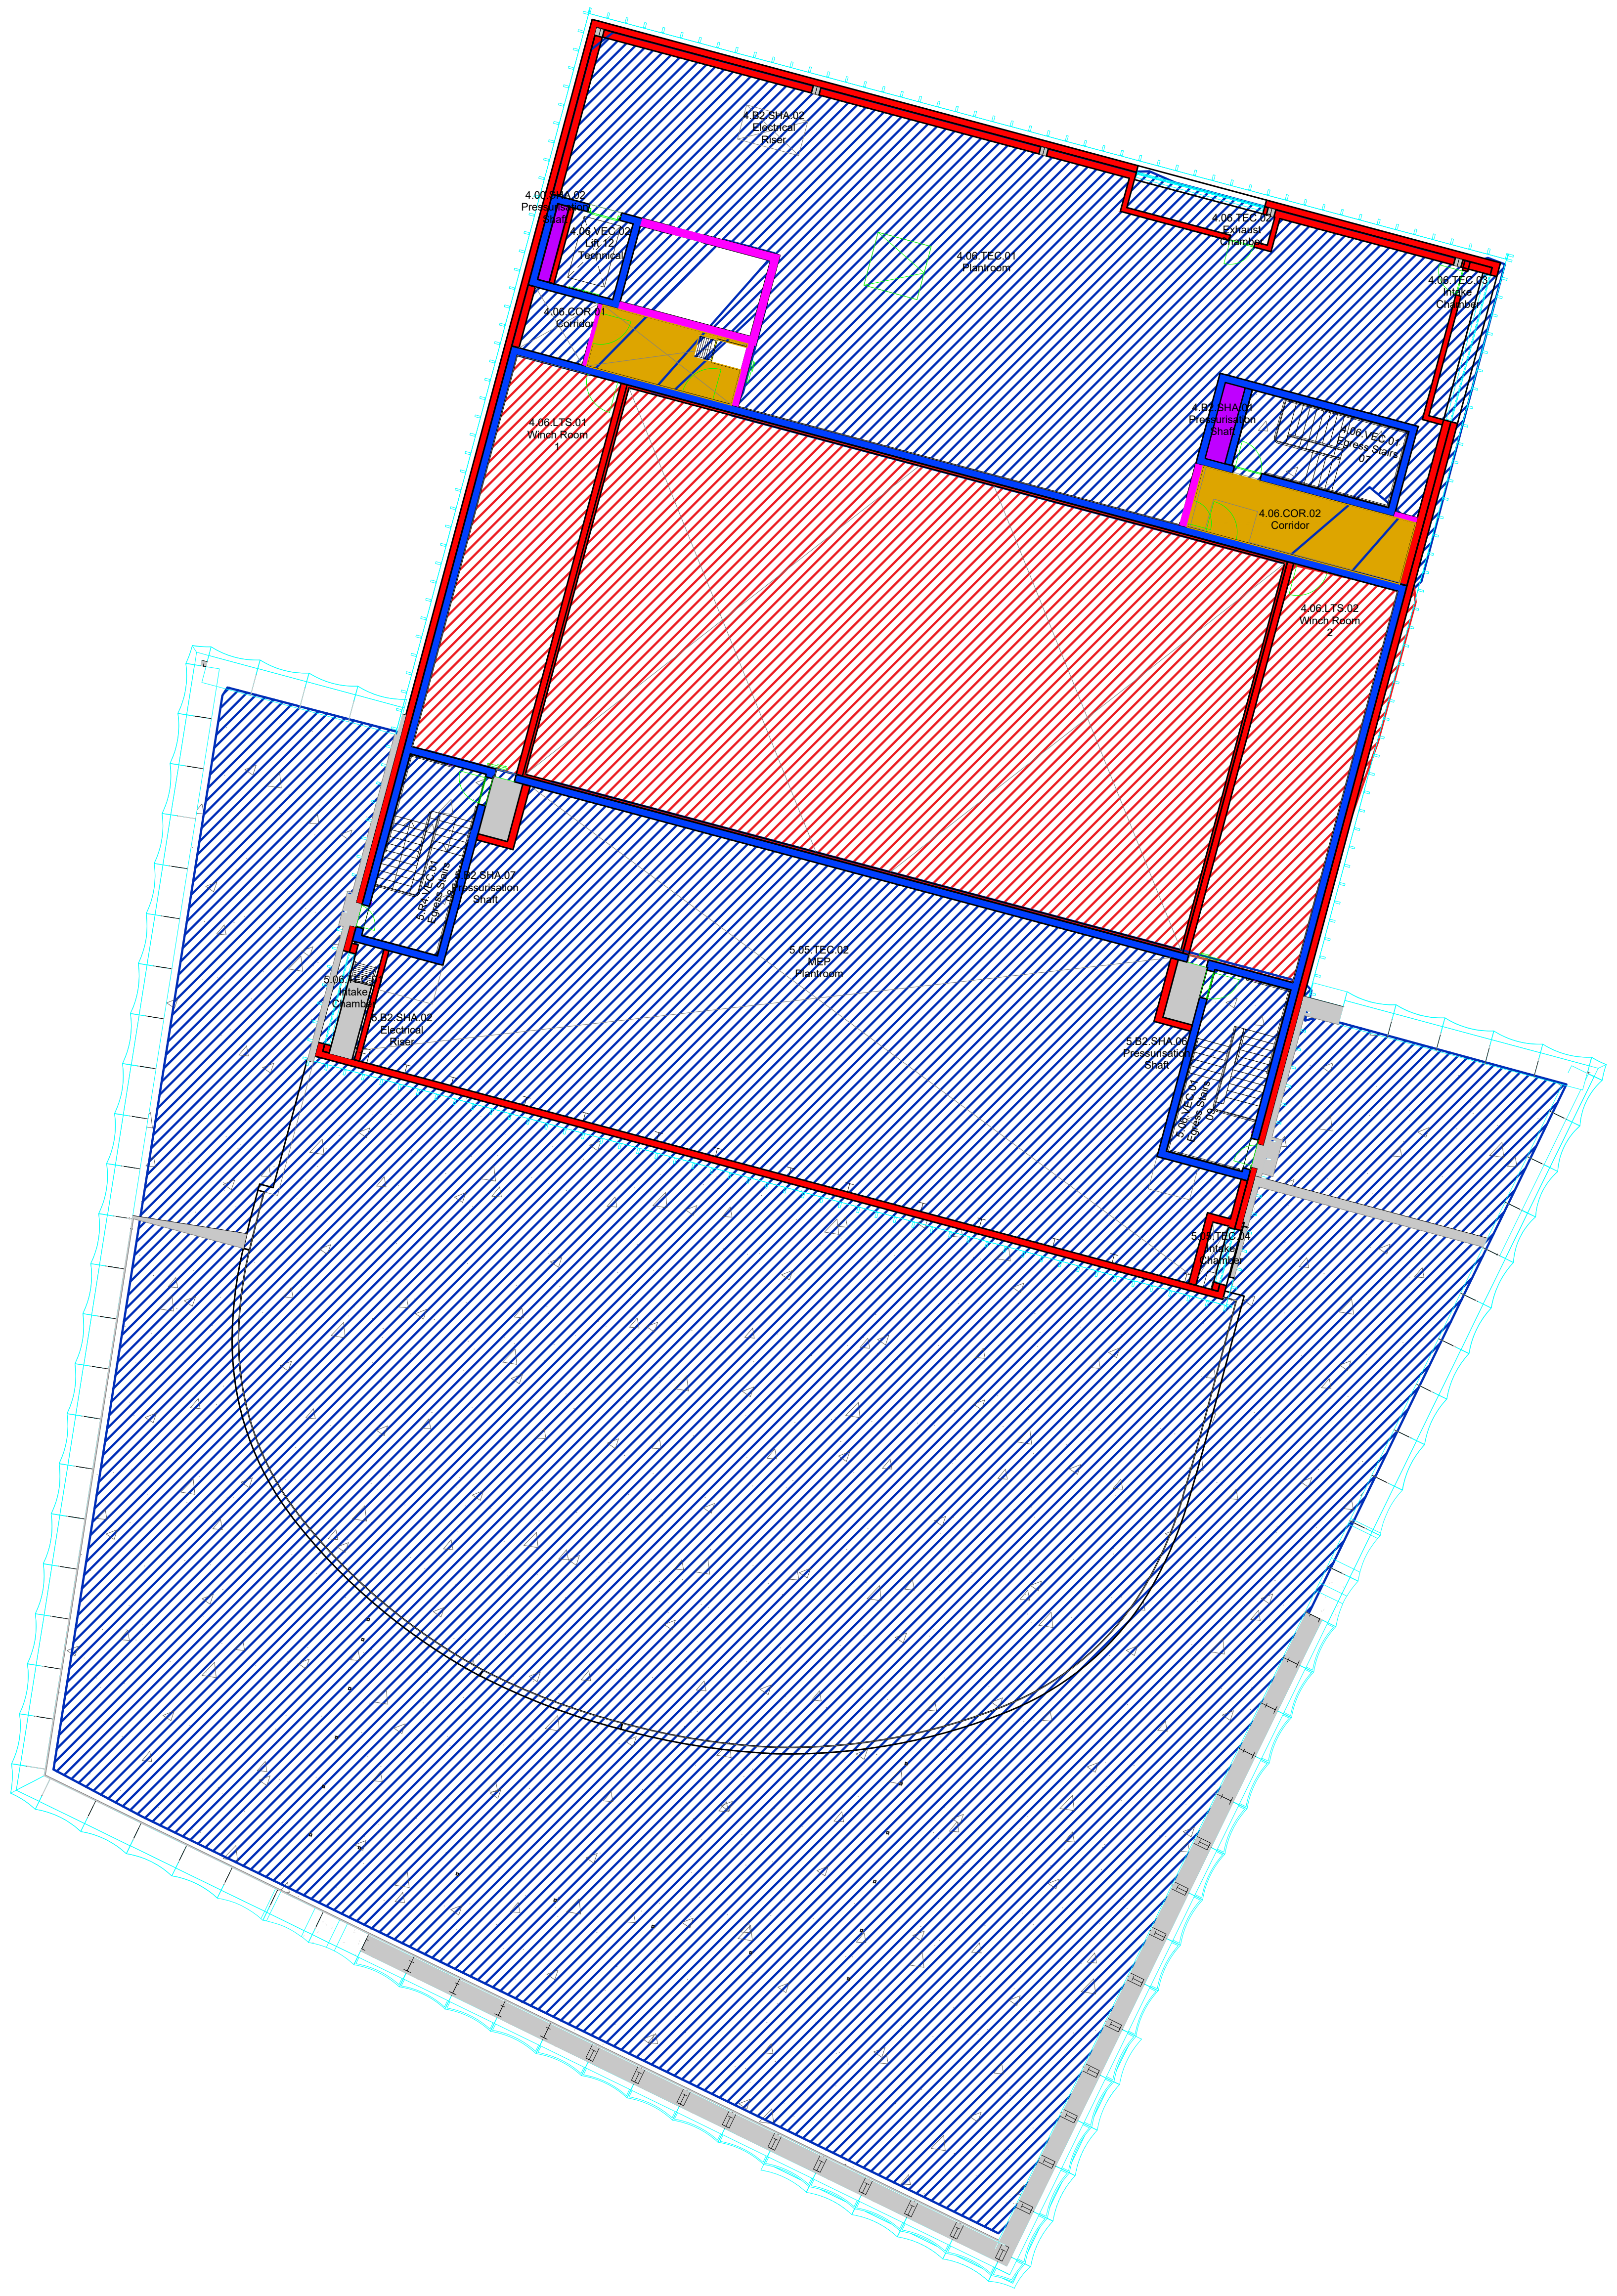
4.B2.SHA.02
Electrical
Riser
4.00.SHA.02
Pressurisation
Shaft
4.06.VEC.02
Lift 12
Technical
4.06.TEC.01
Plantroom
4.06.TEC.02
Exhaust
Chamber
4.06.TEC.03
Intake
Chamber
4.06.COR.01
Corridor
4.B2.SHA.01
Pressurisation
Shaft
4.06.VEC.01
Egress Stairs
07
4.06.COR.02
Corridor
4.06.LTS.01
Winch Room
1
4.06.LTS.02
Winch Room
2
5.R4: VEC.01
Egress Stairs
08
5.B2.SHA.07
Pressurisation
Shaft
5.06.TEC.01
Intake
Chamber
5.B2.SHA.02
Electrical
Riser
5.05.TEC.02
MEP
Plantroom
5.B2.SHA.06
Pressurisation
Shaft
5.06: VEC.01
Egress Stairs
09
5.05.TEC.04
Intake
Chamber

SHAFTS & RISERS LEGEND - PARTS 4 & 5

🟪	**PRESSURISATION SHAFT** Stair / lift lobby pressurisation ducts. *On this plan: 4.00.SHA.02, 4.B2.SHA.01*
🟧	**DC11 CEILING - ACOUSTIC ROCK WOOL** Acoustic rock wool, mineral fibre panel.

JOH-HLA-S4-01-056-XXX-06-DR-AR-011160