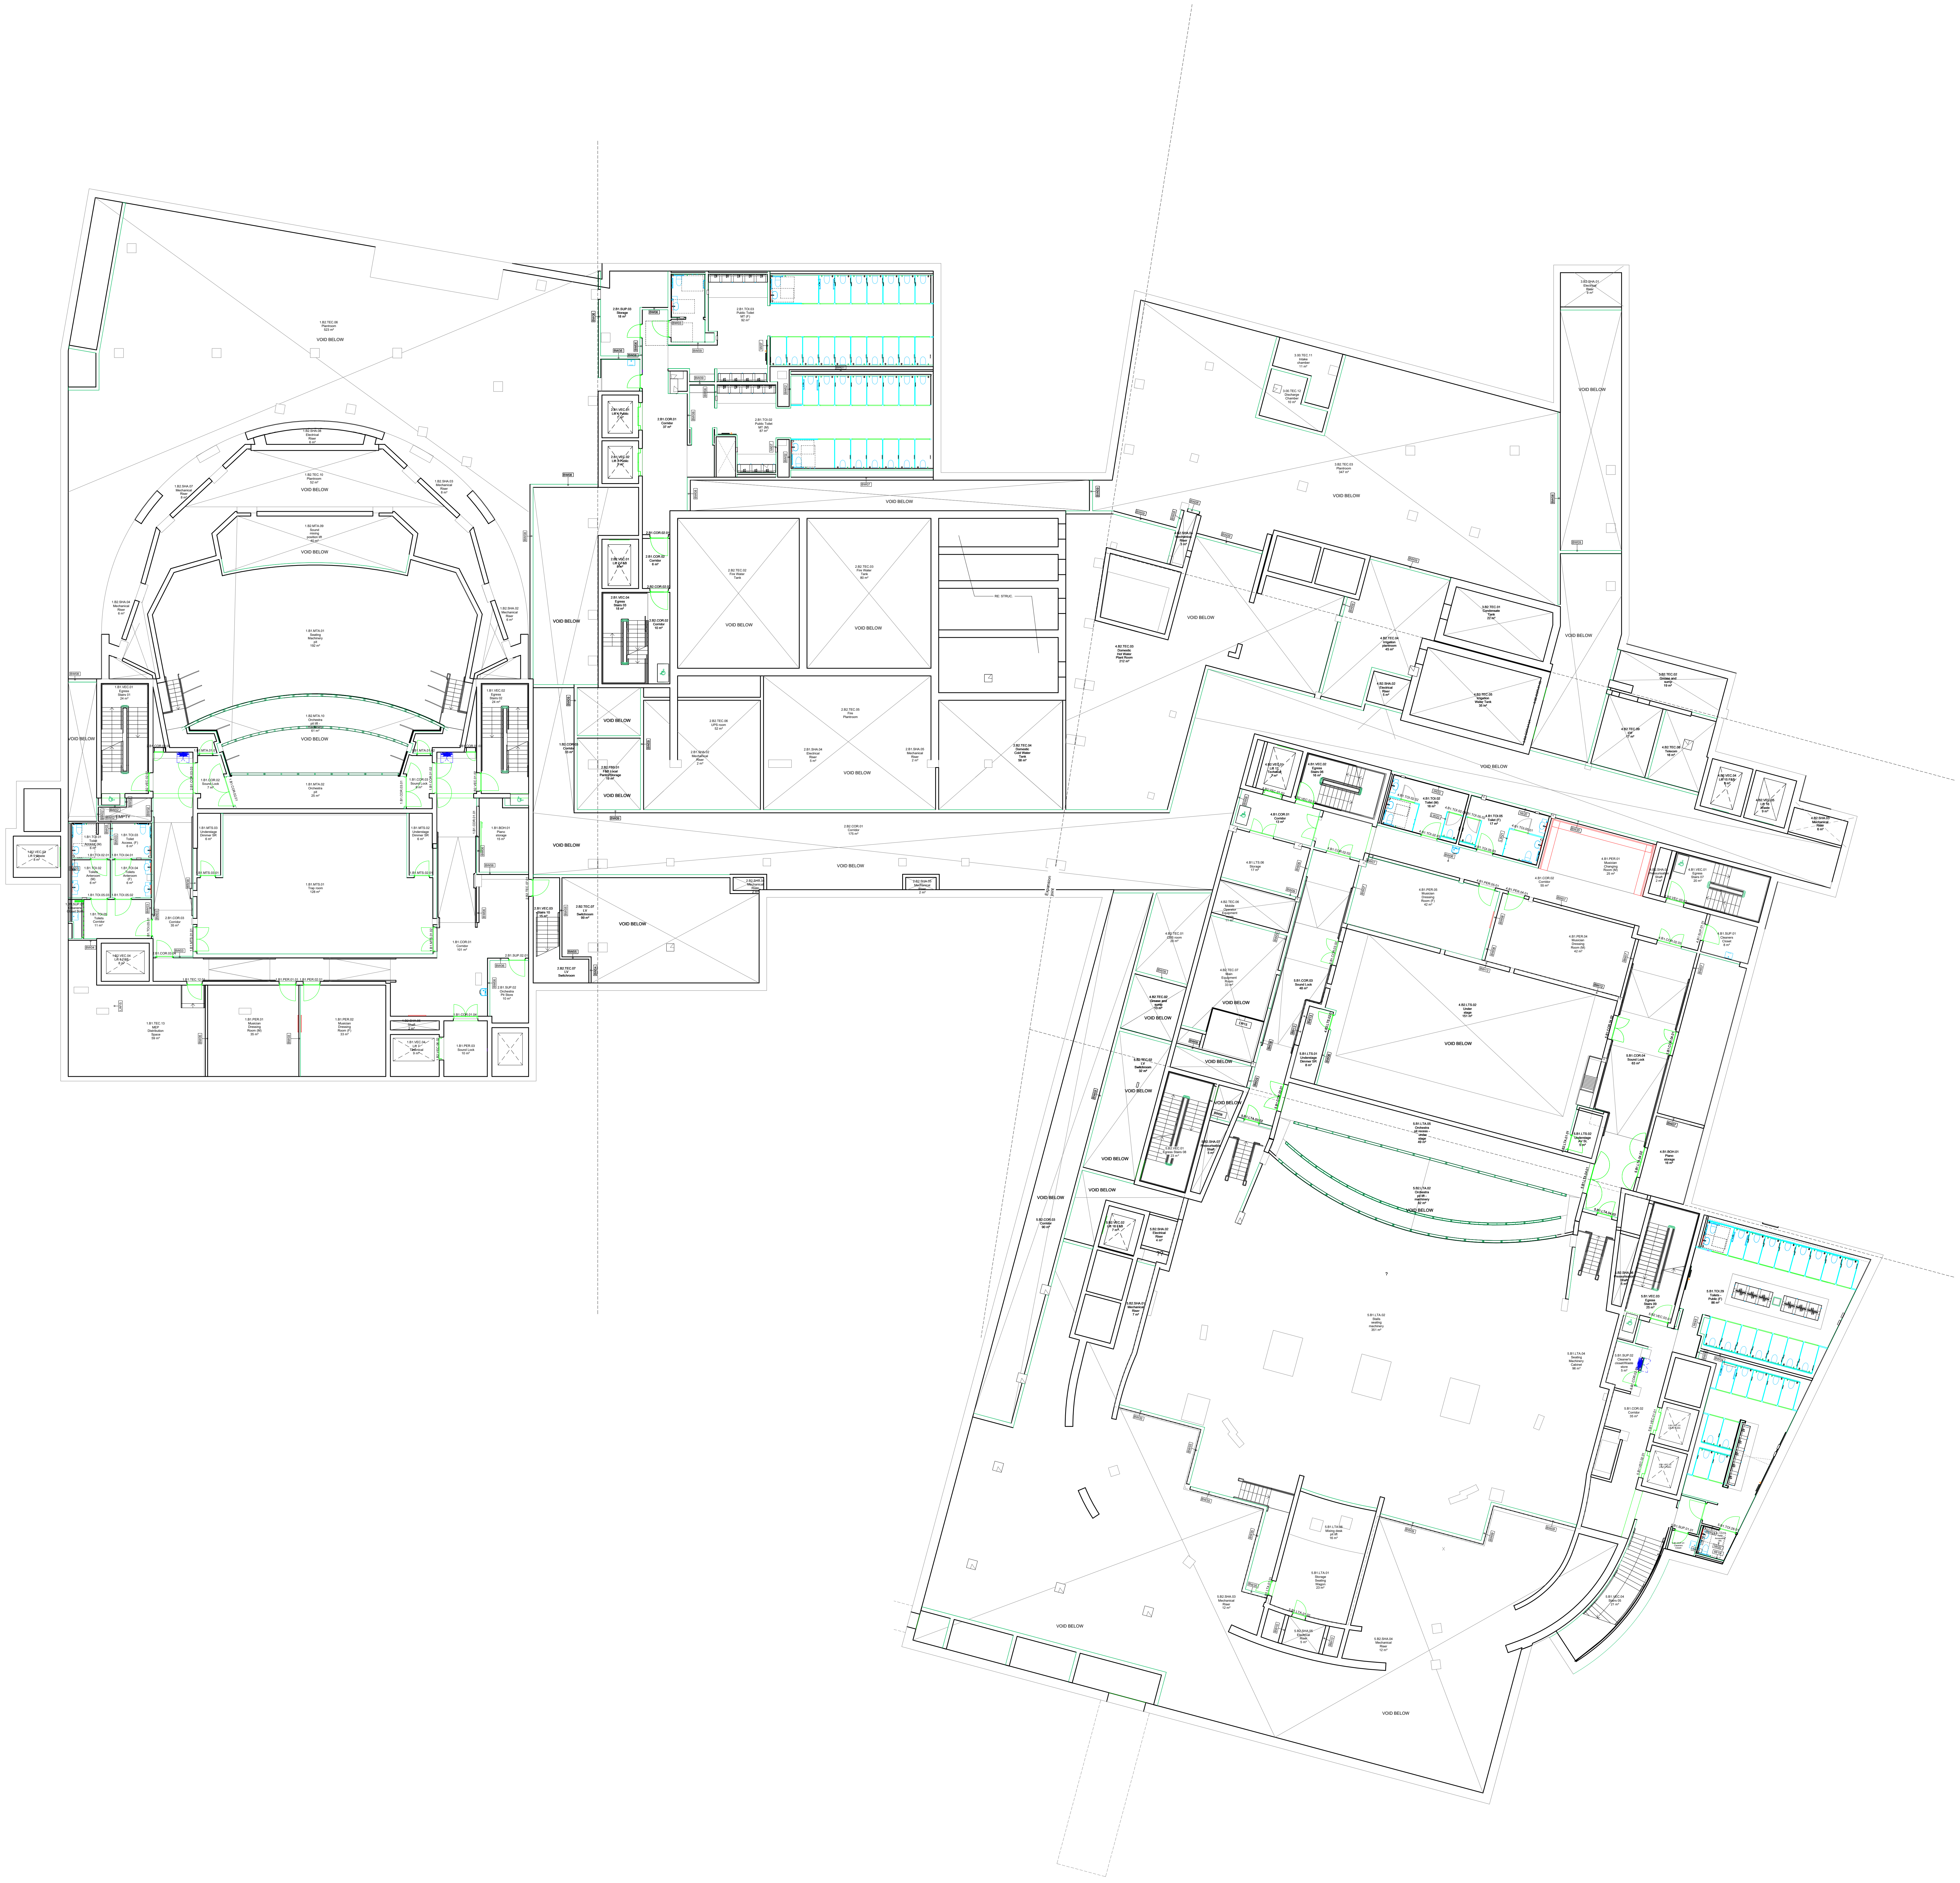
1.B2.TEC.06 Plantroom 523 m²
VOID BELOW
1.B2.SHA.08 Electrical Riser 6 m²
1.B2.TEC.10 Plantroom 52 m²
1.B2.SHA.07 Mechanical Riser 8 m²
1.B2.SHA.03 Mechanical Riser 8 m²
1.B2.MTA.09 Sound mixing position lift 40 m²
1.B2.SHA.04 Mechanical Riser 6 m²
1.B2.SHA.02 Mechanical Riser 6 m²
1.B1.MTA.01 Seating Machinery pit 192 m²
1.B1.VEC.01 Egress Stairs 01 24 m²
1.B1.VEC.02 Egress Stairs 02 24 m²
1.B2.MTA.10 Orchestra pit lift 61 m²
1.B1.COR.02 Sound Lock 7 m²
1.B1.COR.03 Sound Lock 6 m²
1.B1.MTA.02 Orchestra pit 25 m²
EMPTY
1.B1.TOI.01 Toilet Access. (M) 6 m²
1.B1.TOI.03 Toilet Access. (F) 6 m²
1.B1.TOI.02 Toilets Anteroom (M) 6 m²
1.B1.TOI.04 Toilets Anteroom (F) 6 m²
1.B1.TOI.05 Toilets Corridor 11 m²
1.B2.VEC.03 Lift 5 Waste 8 m²
1.B1.MTS.03 Understage Dimmer SR 6 m²
1.B1.MTS.02 Understage Dimmer SR 6 m²
1.B1.BOH.01 Piano storage 15 m²
1.B1.MTS.01 Trap room 128 m²
2.B1.COR.03 Corridor 35 m²
1.B2.VEC.04 Lift 6 F&B 8 m²
1.B1.COR.01 Corridor 101 m²
2.B1.SUP.02 Orchestra Pit Store 10 m²
1.B1.TEC.13 MEP Distribution Space 59 m²
1.B1.PER.01 Musician Dressing Room (M) 35 m²
1.B1.PER.02 Musician Dressing Room (F) 33 m²
1.B2.SHA.06 Shaft 2 m²
1.B1.VEC.04 Lift 7 Technical 9 m²
1.B1.PER.03 Sound Lock 10 m²
2.B1.SUP.03 Storage 18 m²
2.B1.TOI.03 Public Toilet MT (F) 92 m²
2.B1.VEC.01 Lift 4 Public 7 m²
2.B1.VEC.02 Lift 3 Public 7 m²
2.B1.COR.01 Corridor 37 m²
2.B1.TOI.02 Public Toilet MT (M) 87 m²
2.B2.VEC.01 Lift 2 F&B 8 m²
2.B1.COR.02 Corridor 6 m²
2.B1.VEC.04 Egress Stairs 03 18 m²
2.B2.COR.02 Corridor 10 m²
2.B2.TEC.02 Fire Water Tank
2.B2.TEC.03 Fire Water Tank 80 m²
RE: STRUC.
1.B2.COR.03 Corridor 33 m²
2.B2.FBS.01 F&B Local Pantry/Storage 19 m²
2.B2.TEC.06 UPS room 52 m²
2.B1.SHA.02 Mechanical Riser 2 m²
2.B2.TEC.05 Fire Plantroom
2.B1.SHA.04 Electrical Riser 5 m²
2.B1.SHA.05 Mechanical Riser 2 m²
2.B2.TEC.04 Domestic Cold Water Tank 58 m²
2.B2.COR.01 Corridor 175 m²
2.B1.VEC.03 Stairs 10 15 m²
2.B2.TEC.07 LV Switchroom 99 m²
2.B2.SHA.04 Mechanical Riser 2 m²
2.B2.SHA.05 Mechanical Riser 2 m²
3.00.TEC.11 Intake chamber 11 m²
3.00.TEC.12 Discharge Chamber 10 m²
3.B2.SHA.01 Electrical Riser 9 m²
3.B2.TEC.03 Plantroom 347 m²
4.B2.SHA.04 Mechanical Riser 3 m²
4.B2.TEC.03 Domestic Hot Water Plant Room 212 m²
4.B2.TEC.04 Irrigation plantroom 45 m²
3.B2.TEC.01 Condensate Tank 22 m²
4.B2.SHA.02 Electrical Riser 5 m²
4.B2.TEC.05 Irrigation Water Tank 35 m²
3.B2.TEC.02 Grease and sump 19 m²
4.B2.TEC.09 IDF 17 m²
4.B2.TEC.08 Telecom 16 m²
4.B2.VEC.04 Lift 15 F&B 9 m²
4.B2.VEC.05 Lift 16 Waste 9 m²
4.B2.SHA.03 Mechanical Riser 6 m²
4.B2.VEC.01 Lift 12 Technical 7 m²
4.B1.VEC.02 Egress Stairs 06 16 m²
4.B1.TOI.02 Toilet (M) 16 m²
4.B1.TOI.05 Toilet (F) 17 m²
4.B1.PER.01 Musician Changing Room (M) 25 m²
4.B2.SHA.01 Pressurisation Shaft 2 m²
4.B1.VEC.01 Egress Stairs 07 20 m²
4.B1.COR.01 Corridor 13 m²
4.B1.COR.02 Corridor 55 m²
4.B1.LTS.06 Storage 17 m²
4.B1.PER.05 Musician Dressing Room (F) 42 m²
4.B1.PER.04 Musician Dressing Room (M) 42 m²
4.B1.SUP.01 Cleaners Closet 8 m²
Expansion joint
4.B2.TEC.06 Mobile Operator Equipment Room 11 m²
4.B2.TEC.01 CBS room 20 m²
4.B2.TEC.07 Main Equipment Room 33 m²
5.B1.COR.03 Sound Lock 48 m²
4.B2.LTS.02 Under stage 151 m²
4.B2.TEC.02 Grease and sump 13 m²
5.B1.LTS.01 Understage Dimmer SR 8 m²
5.B1.COR.04 Sound Lock 63 m²
5.B2.TEC.02 LV Switchroom 32 m²
5.B1.LTA.05 Orchestra pit recess - under stage 49 m²
5.B1.LTS.02 Understage AV SL 5 m²
4.B1.BOH.01 Piano storage 16 m²
5.B2.VEC.01 Egress Stairs 08 23 m²
5.B2.SHA.07 Pressurisation Shaft 5 m²
5.B2.LTA.02 Orchestra pit lift - machinery 82 m²
5.B2.COR.03 Corridor 90 m²
5.B2.VEC.02 Lift 18 F&B 7 m²
5.B2.SHA.02 Electrical Riser 4 m²
??
5.B2.SHA.01 Mechanical Riser 7 m²
?
5.B1.LTA.02 Stalls seating machinery 351 m²
5.B2.SHA.06 Pressurisation Shaft 5 m²
5.B1.VEC.03 Egress Stairs 09 25 m²
5.B1.TOI.29 Toilets - Public (F) 86 m²
5.B1.LTA.04 Seating Machinery Cabinet 96 m²
5.B1.SUP.02 Cleaner's closet/Waste store 5 m²
5.B1.COR.02 Corridor 35 m²
5.B1.LTA.06 Mixing desk pit lift 16 m²
5.B1.LTA.01 Storage Seating Wagon 23 m²
5.B2.SHA.03 Mechanical Riser 12 m²
5.B2.SHA.05 Electrical Riser 5 m²
5.B2.SHA.04 Mechanical Riser 12 m²
5.B1.VEC.04 Stairs 05 21 m²
VOID BELOW