

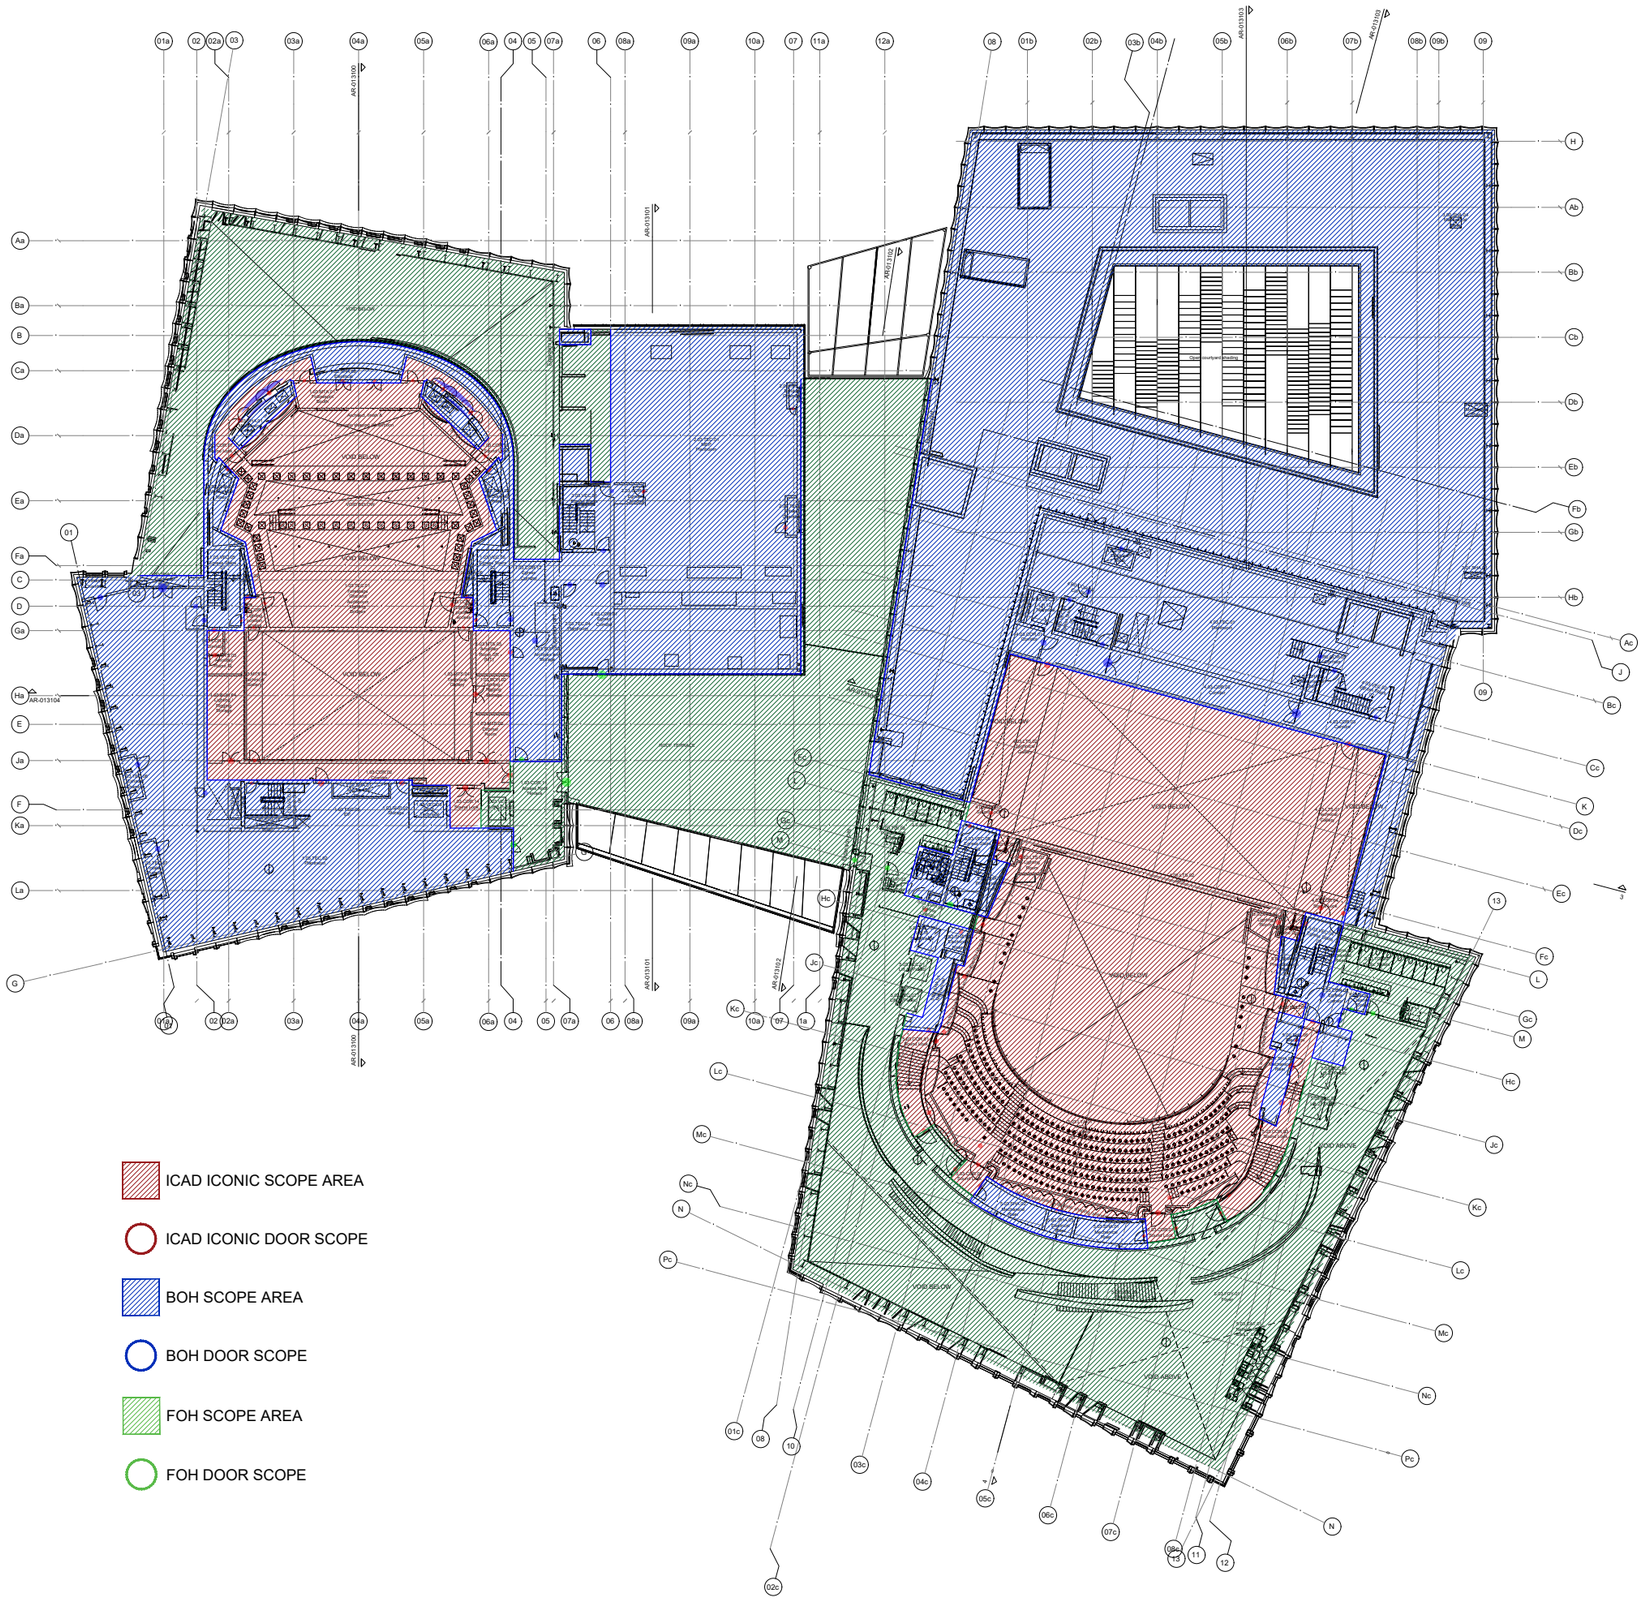


DO NOT SCALE

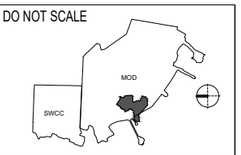

INDEX PLAN

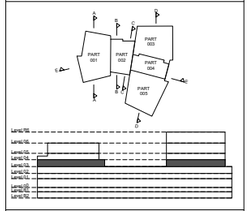

BUILDING KEY PLAN

GENERAL NOTES:

LEGEND & ABBREVIATIONS:

REV	DATE	BY	DESCRIPTION	CHK	APR
F00	31-01-2024	BB	Issued for Construction	LTN	NF

DRAWING STATUS: Issued for Construction

CLIENT:

LEAD DESIGN CONSULTANTS:

LEAD ENGINEERING CONSULTANT:

GENERAL CONTRACTOR: GENERAL CONTRACTOR

PROJECT: JEDDAH OPERA HOUSE

TITLE: ARCHITECT PLAN LEVEL 03

SCALE A0 (841x1189)	CHECKED	APPROVED	MODEL FILE REF
1:200	LTN	NF	JOH-HLA-S4-01-056-XXX-ZZ-M0-AR-010000
PROJECT No:	DESIGNED	DRAWN	DATE:
1960020123	HLA	VCS	31-01-2024
DRAWING NO.			REV:
JOH-HLA-S4-01-056-XXX-03-DR-AR-011130			F00

©JCDC