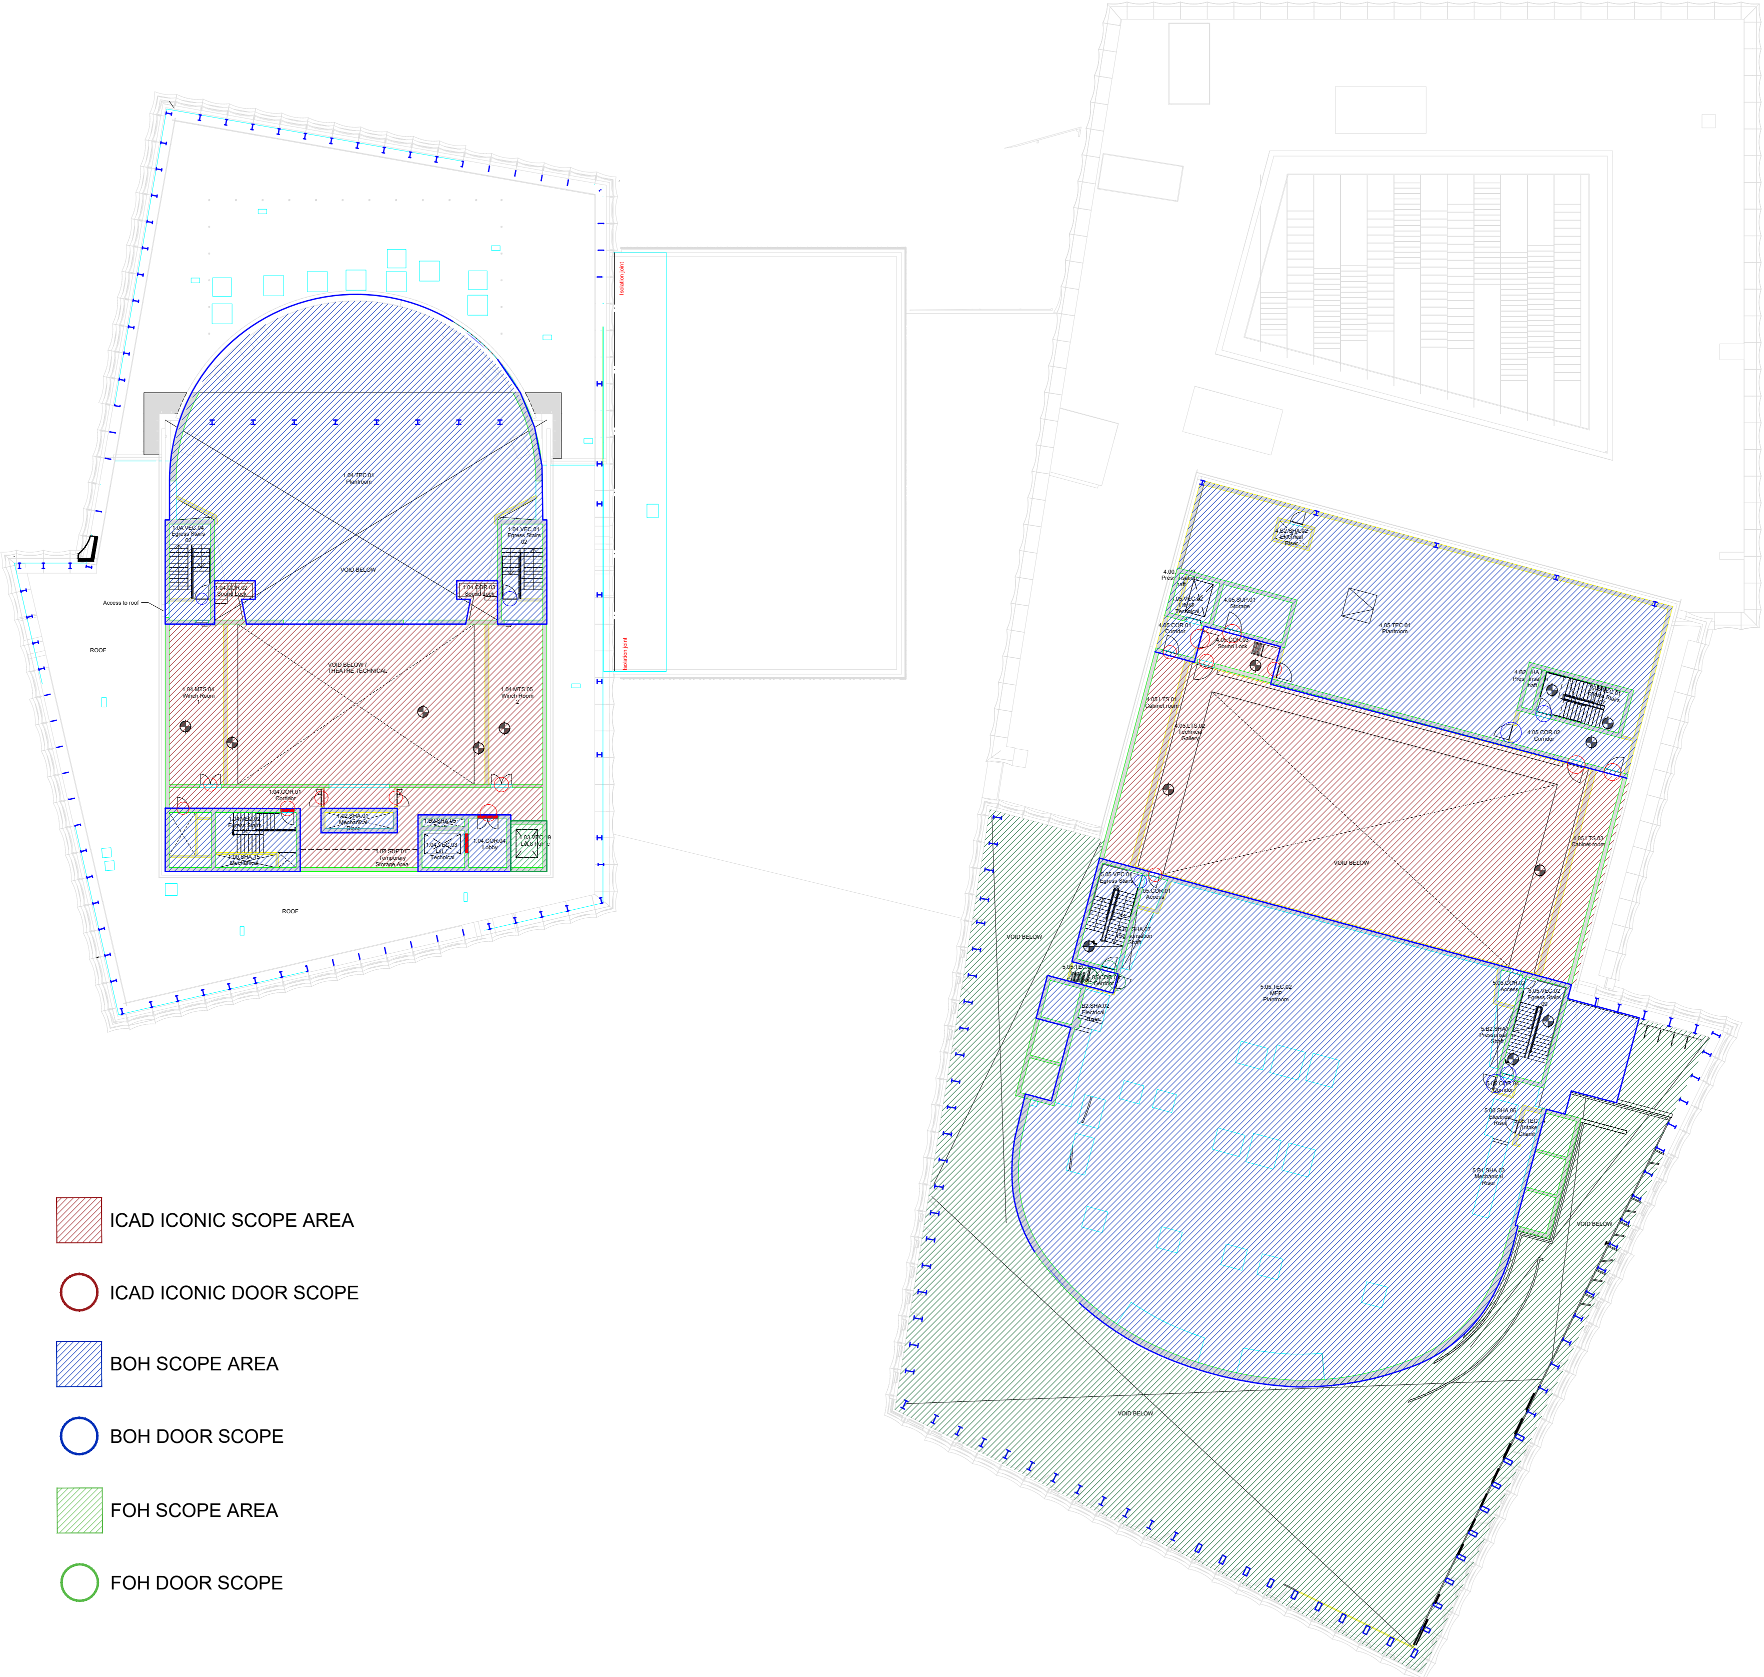

▨ ICAD ICONIC SCOPE AREA

○ ICAD ICONIC DOOR SCOPE

▨ BOH SCOPE AREA

○ BOH DOOR SCOPE

▨ FOH SCOPE AREA

○ FOH DOOR SCOPE

DO NOT SCALE

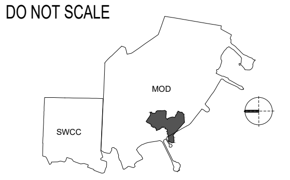

INDEX PLAN

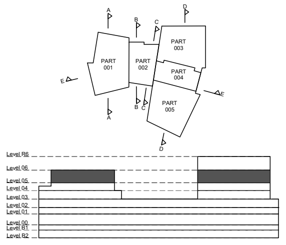

BUILDING KEY PLAN

GENERAL NOTES:

LEGEND & ABBREVIATIONS:

Strutural Floor Expansion Joint

Interior Joint Details:
- JOH-HLA-S4-01-056-XXX-ZZ-DR-AR-015800

See facade detail package for exterior joints

- The line serves as an indicative guide, and the partial plans should be used for accurately establishing the joint line in the finishes.

F00	31-01-2024	BB	Issued for Construction	LFN	NF
REV	**DATE**	**BY**	**DESCRIPTION**	**CHK**	**APR**

DRAWING STATUS:
Issued for Construction

CLIENT:
C:\Users\TZKA\OneDrive - Ramboll\Desktop\Temp\JOH-HLA-S4-01-056-XXX-ZZ-M3-AR-019300-JCDCLogo-26987616.jpg

LEAD DESIGN CONSULTANTS:
C:\Users\TZKA\OneDrive - Ramboll\Desktop\Temp\JOH-HLA-S4-01-056-XXX-ZZ-M3-AR-019300-HLLogoBlackRGB-26987618.jpg

LEAD ENGINEERING CONSULTANT:
C:\Users\TZKA\OneDrive - Ramboll\Desktop\Temp\JOH-HLA-S4-01-056-XXX-ZZ-M3-AR-019300-BHlogo-26987620.png

GENERAL CONTRACTOR:
GENERAL CONTRACTOR

PROJECT:
JEDDAH OPERA HOUSE

TITLE:
ARCHITECT
PLAN
LEVEL 05

SCALE A0 (841x1189)	CHECKED	APPROVED	MODEL FILE REF
1:200	LFN	NF	JOH-HLA-S4-01-056-XXX-ZZ-M3-AR-019300
PROJECT No:	DESIGNED	DRAWN	DATE:
1960020123	HLA	VCS	31-01-2024

DRAWING NO.
JOH-HLA-S4-01-056-XXX-05-DR-AR-011150

REV:
F00

©JCDC