

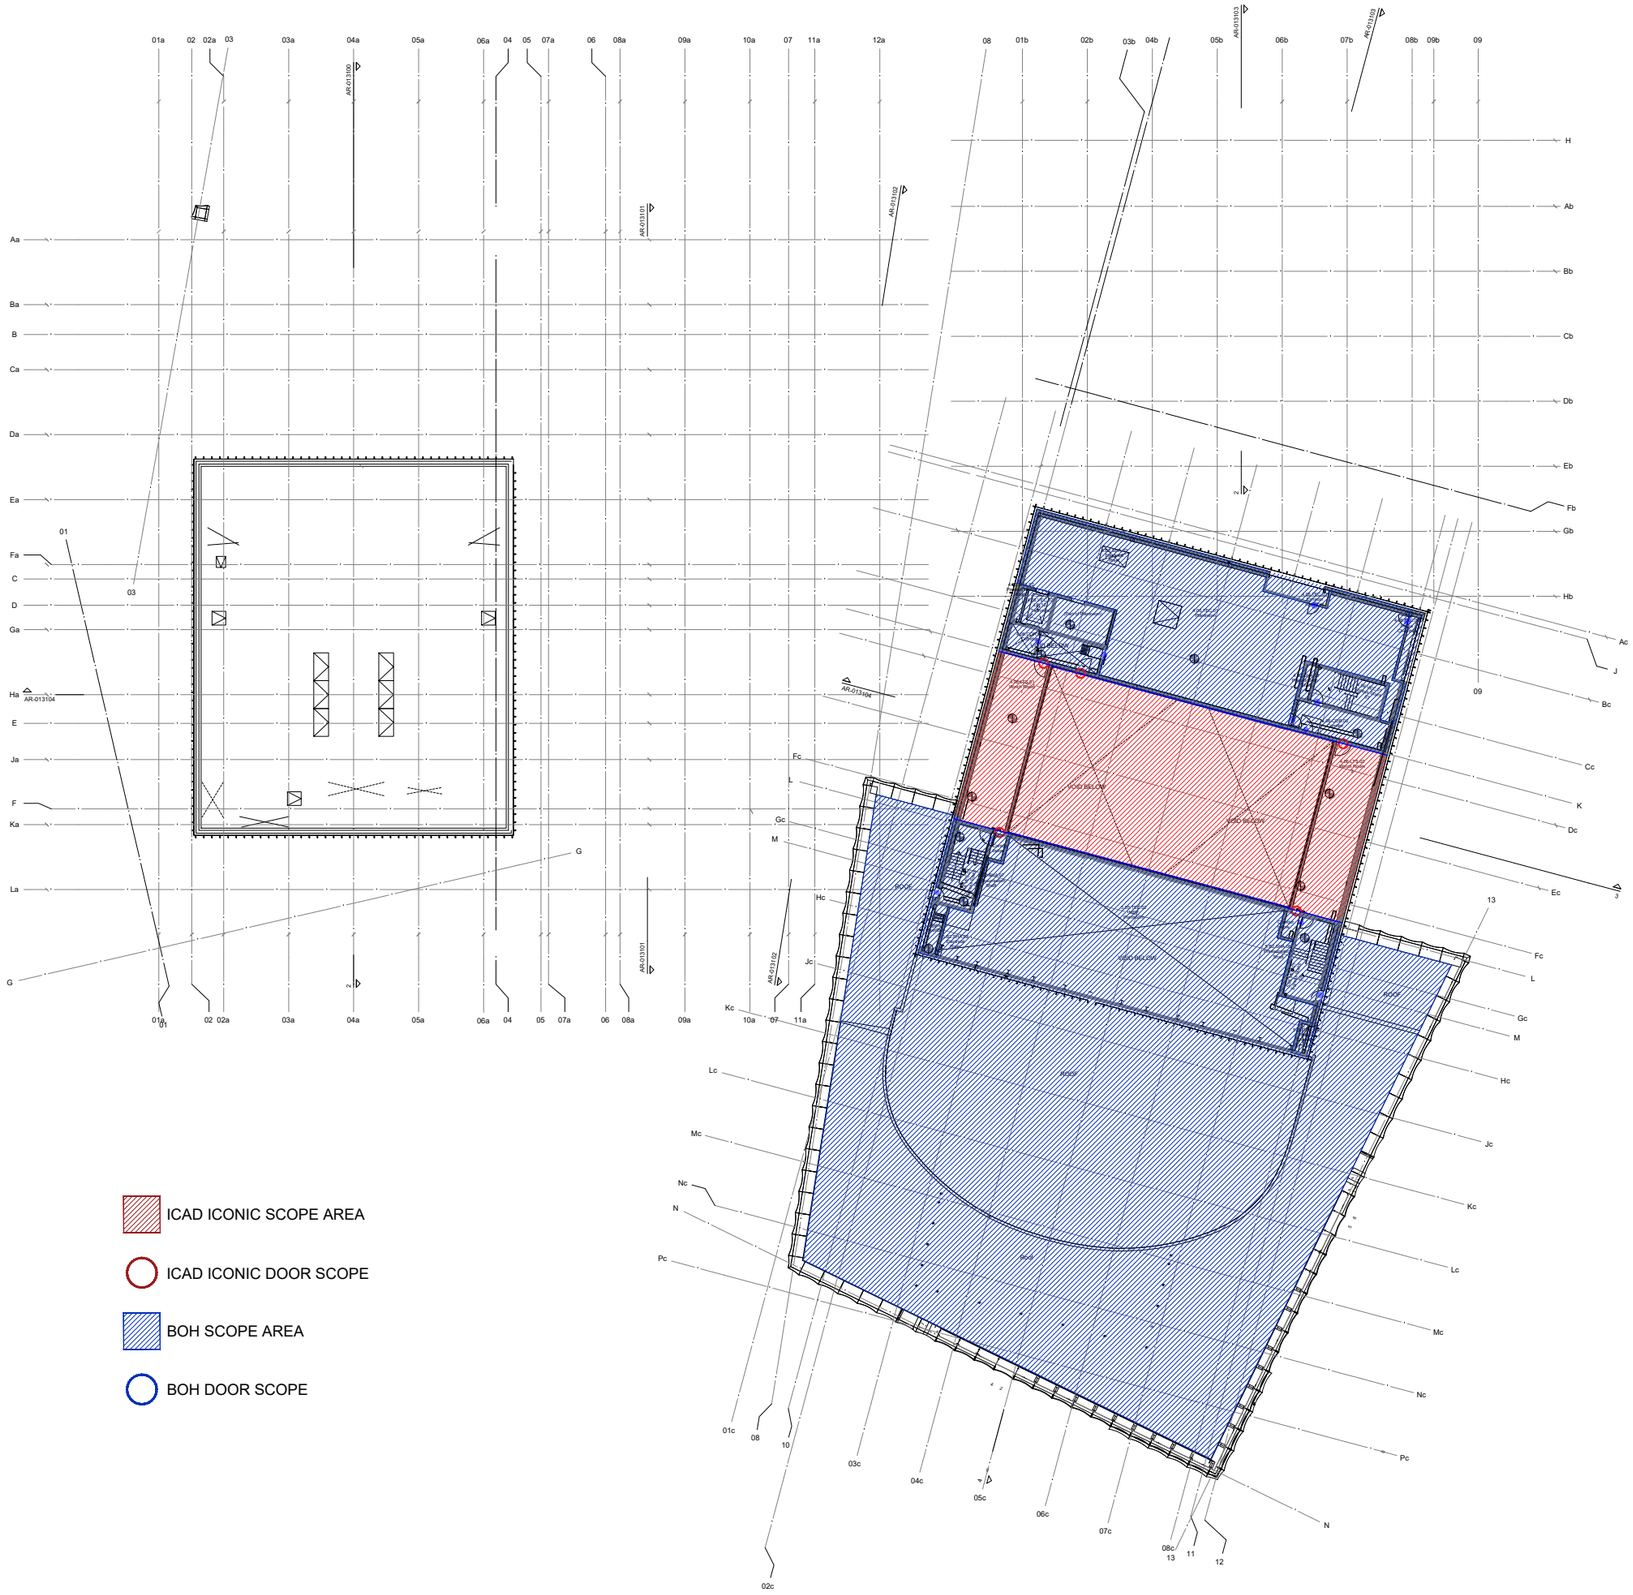


DO NOT SCALE

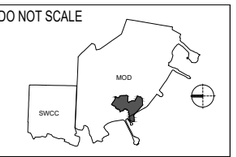

INDEX PLAN

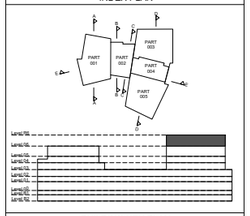

BUILDING KEY PLAN

GENERAL NOTES:

For the Lyric Theatre - Level - 06 (Stage) floor plan, please refer to the drawing number - JHO-HLA-S4-01-056-005-ZZ-DR-AR-014103

LEGEND & ABBREVIATIONS

REV	DATE	BY	DESCRIPTION	CHK	APR
P00	31-01-2024	BB	Issued for Construction	LFN	NF

DRAWING STATUS: Issued for Construction

CLIENT:

LEAD DESIGN CONSULTANTS:

LEAD ENGINEERING CONSULTANT:

GENERAL CONTRACTOR: GENERAL CONTRACTOR

PROJECT: JEDDAH OPERA HOUSE

TITLE: ARCHITECT PLAN LEVEL 06

SCALE A0 (841x1189)	CHECKED	APPROVED	MODEL FILE REF
1:200	LFN	NF	JOH-HLA-S4-01-056-XXX-ZZ-M3-AR-010000
PROJECT No:	DESIGNED:	DRAWN:	DATE:
196000123	HLA	VCS	31-01-2024

DRAWING NO: JOH-HLA-S4-01-056-XXX-06-DR-AR-011160 REV: P00

©JCDC